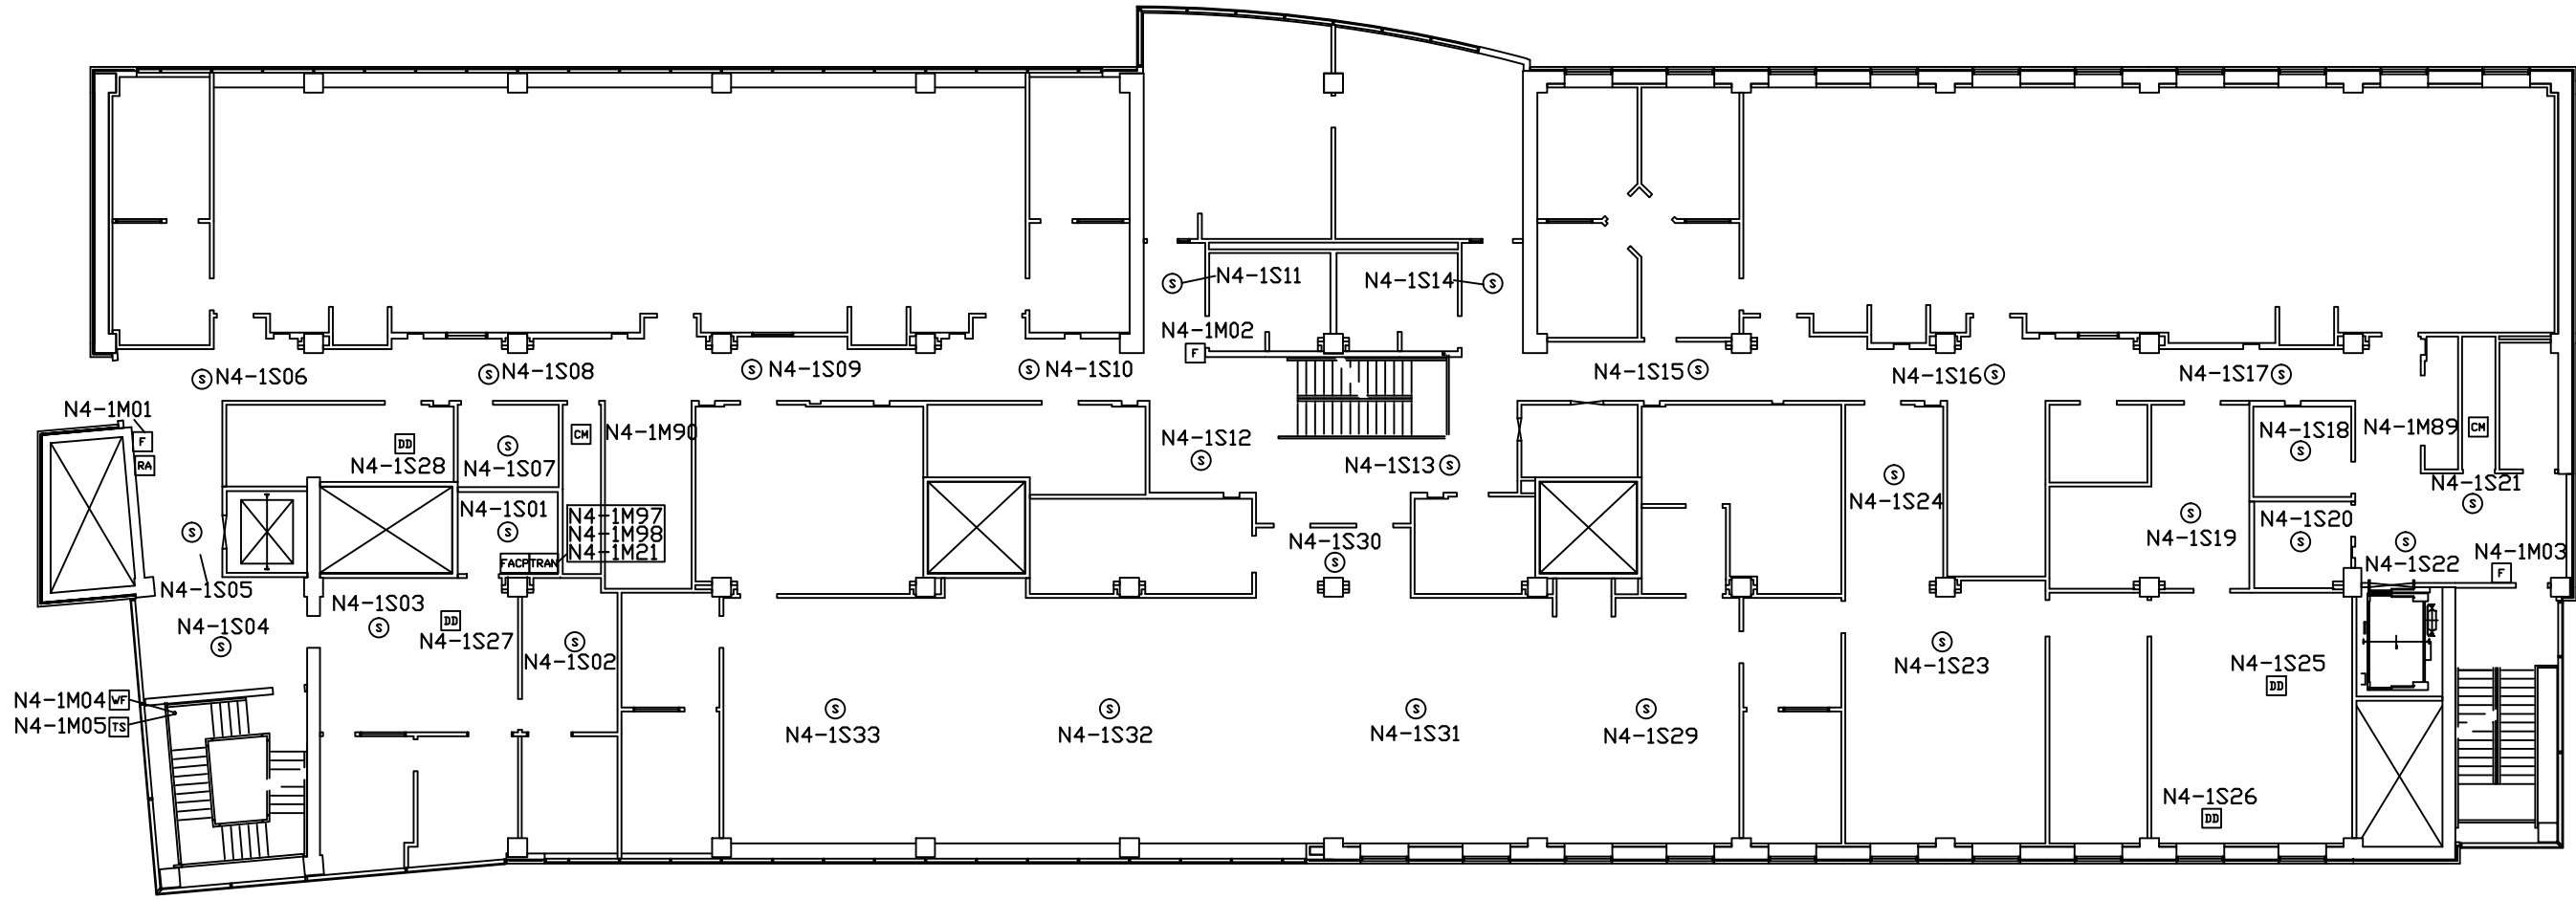


NOTE:
NFS DRAWINGS ARE BASED ON THE PROJECT
ARCHITECT/ENGINEER (A/E) PLANS AND SPECIFICATIONS
FURNISHED TO NFS. A/E IS SOLELY RESPONSIBLE
(NOT NFS) FOR THE TYPE, SIZE, LOCATION, AND
SUITABILITY OF ALL FIRE ALARMS, CONTROL PANELS,
AND OTHER DEVICES SHOWN ON THE A/E PLANS.
NFS DRAWINGS ARE TO SHOW ONLY THE WIRING
DIAGRAMS BETWEEN FIRE ALARM DEVICES AND
CONTROL PANELS. NFS IS NOT RESPONSIBLE FOR
THE INFORMATION SHOWN ON THE A/E PLANS.

EMMA ECCLES JONES
MEDICAL SCIENCES BUILDING
UNIVERSITY OF UTAH HEALTH SCIENCES
SECOND FLOOR
15 NORTH MEDICAL DRIVE EAST
SALT LAKE CITY, UTAH


NFS
NELSON FIRE SYSTEMS
801-468-8300


DRAWN BY:	DS
DESIGNED BY:	XXXX
APPROVED BY:	TCT
DATE:	12/28/2005
SCALE:	N.T.S.
PROJECT NO:	XXXX
REV NO:	XXXX
DRAWING NAME:	MEDSCIENCE2.DWG

FIRE ALARM SYSTEM
SECOND FLOOR
ADDRESSABLE LOOP NUMBERS

NFS
FA-2-04

DEVICE LEGEND	
SYMBOL	DESCRIPTION
Ⓢ	SMOKE DETECTOR W/BASE
F	MANUAL PULL STATION
DD	DUCT SMOKE DETECTOR
WF	WATERFLOW SWITCH MONITOR MODULE
TS	TAMPER SWITCH MONITOR MODULE
CM	CONTROL MODULE
RA	REMOTE ANNUNCIATOR ENCLOSURE
FACP	FIRE ALARM CONTROL PANEL
TRAN	TRANSPONDER PANEL


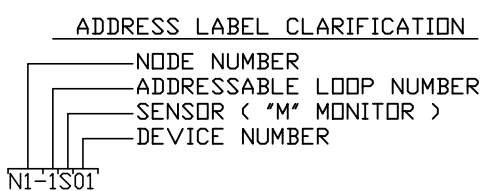


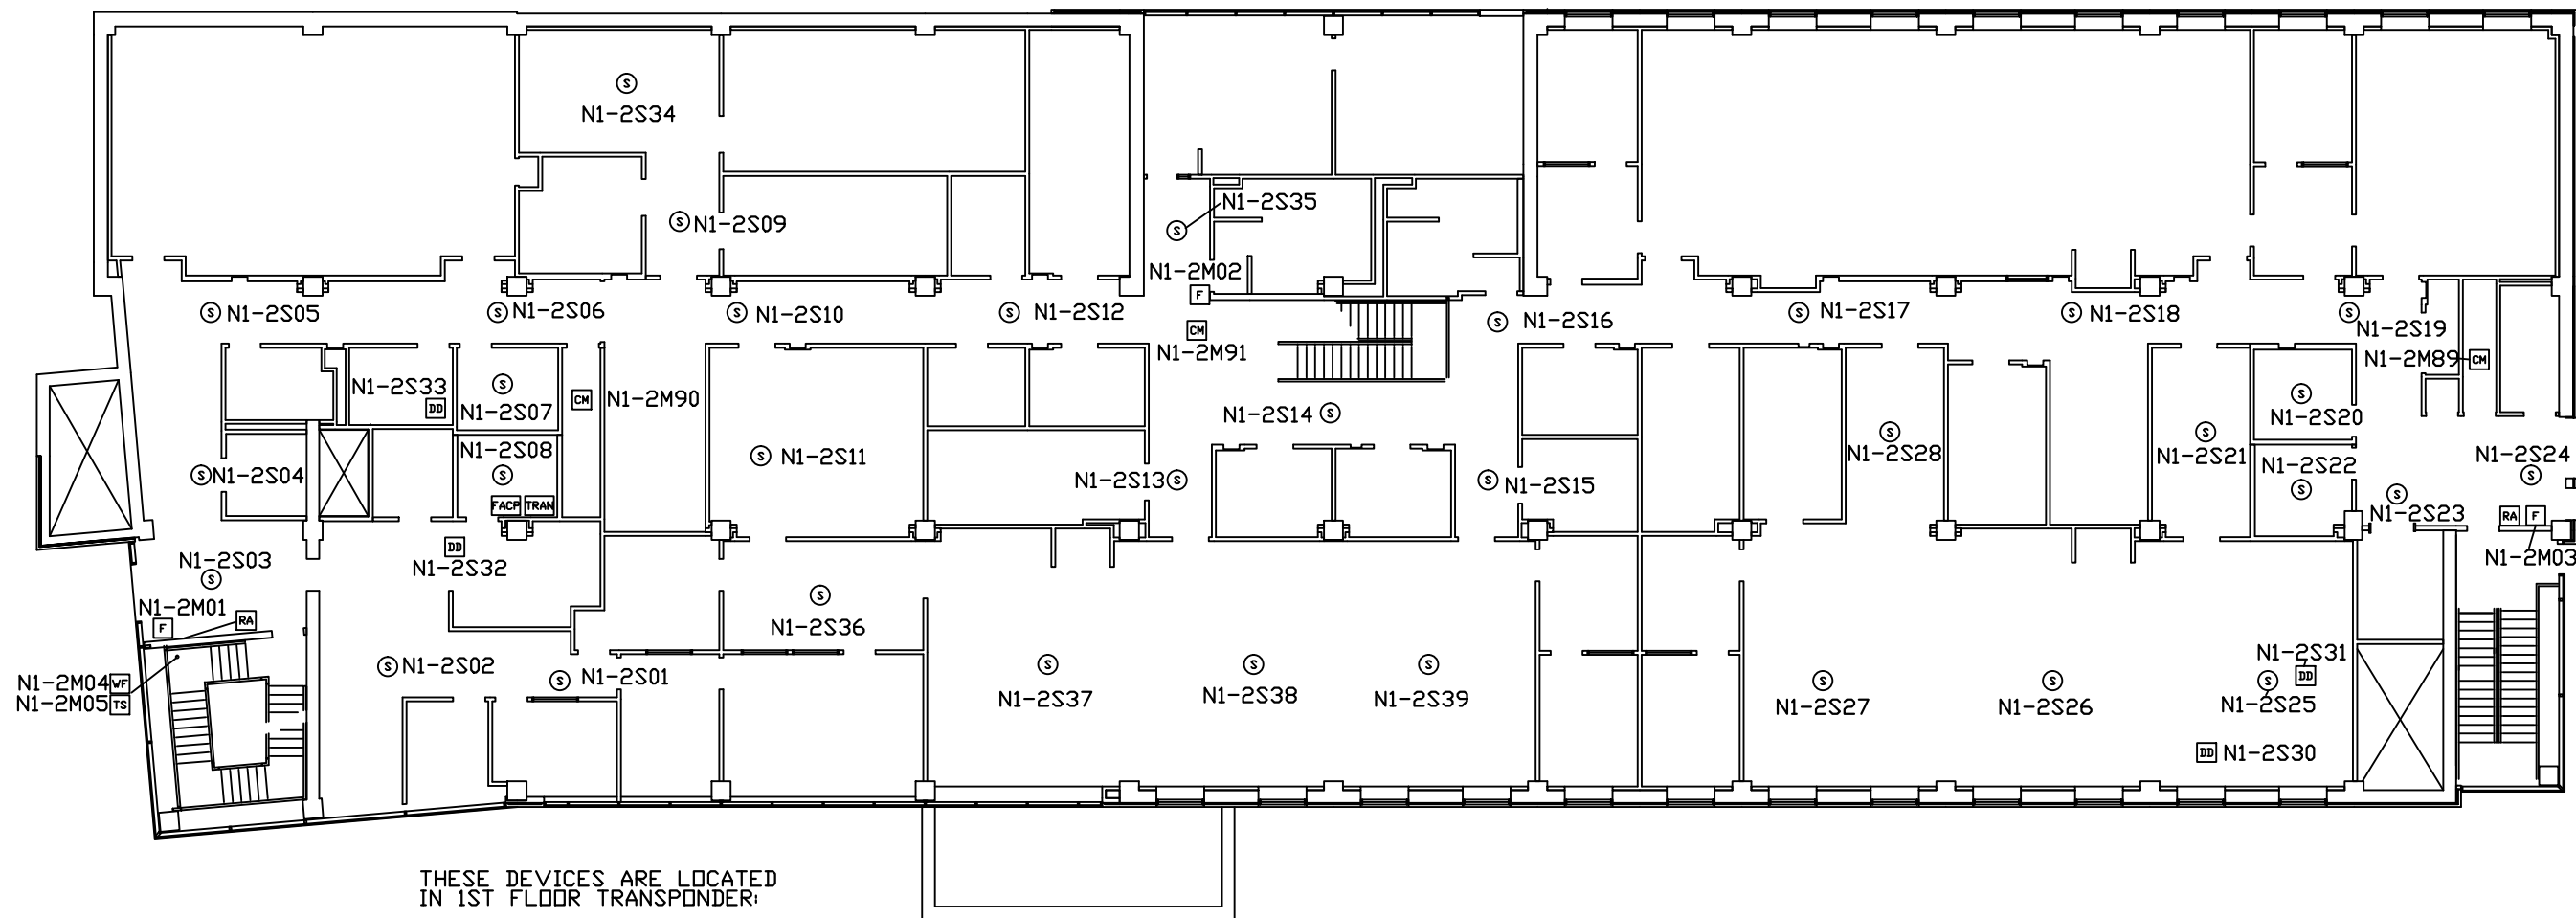

THESE DEVICES ARE LOCATED
IN 1ST FLOOR TRANSPONDER:

- N1-2M21-TRANSPONDER SUPERVISION
- N1-2M98-BUILDING STROBE BYPASS
- N1-2M95-FIRST FLOOR RELAY ACTIVATION
- N1-2M96-INCC BYPASS BUTTON SUPERVISION
- N1-2M06-INCC BYPASS BUTTON SUPERVISION

DEVICE LEGEND	
SYMBOL	DESCRIPTION
Ⓢ	SMOKE DETECTOR W/BASE
F	MANUAL PULL STATION
DD	DUCT SMOKE DETECTOR
WF	WATERFLOW SWITCH MONITOR MODULE
TS	TAMPER SWITCH MONITOR MODULE
CM	CONTROL MODULE
RA	REMOTE ANNUNCIATOR ENCLOSURE
FACP	FIRE ALARM CONTROL PANEL
TRAN	TRANSPONDER PANEL

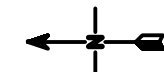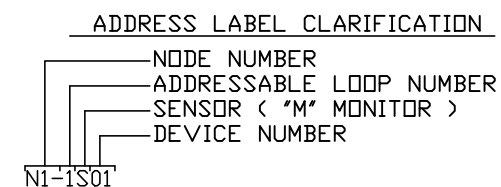

NOTE:
NFS DRAWINGS ARE BASED ON THE PROJECT
ARCHITECT/ENGINEER (A/E) PLANS AND SPECIFICATIONS
FURNISHED TO NFS. A/E IS SOLELY RESPONSIBLE
(NOT NFS) FOR THE TYPE, SIZE, LOCATION, AND
SUITABILITY OF ALL FIRE ALARMS, CONTROL PANELS,
AND OTHER DEVICES SHOWN ON THE A/E PLANS.
NFS DRAWINGS ARE TO SHOW ONLY THE WIRING
DIAGRAMS BETWEEN FIRE ALARM DEVICES AND
CONTROL PANELS. NFS IS NOT RESPONSIBLE FOR
THE INFORMATION SHOWN ON THE A/E PLANS.



EMMA ECCLES JONES
MEDICAL SCIENCE BUILDING
UNIVERSITY OF UTAH HEALTH SCIENCES
FIRST FLOOR
15 NORTH MEDICAL DRIVE EAST
SALT LAKE CITY, UTAH

NFS
NELSON FIRE SYSTEMS
801-468-8300

DRAWN BY:	DS
DESIGNED BY:	XXXX
APPROVED BY:	TCT
DATE:	12/28/2005
SCALE:	N.T.S.
PROJECT NO:	XXXX
REV NO:	XXXX
DRAWING NAME:	MEDSCIENCE1.DWG

FIRE ALARM SYSTEM
FIRST FLOOR
ADDRESSABLE LOOP NUMBERS

NFS:
FA-I-04

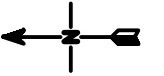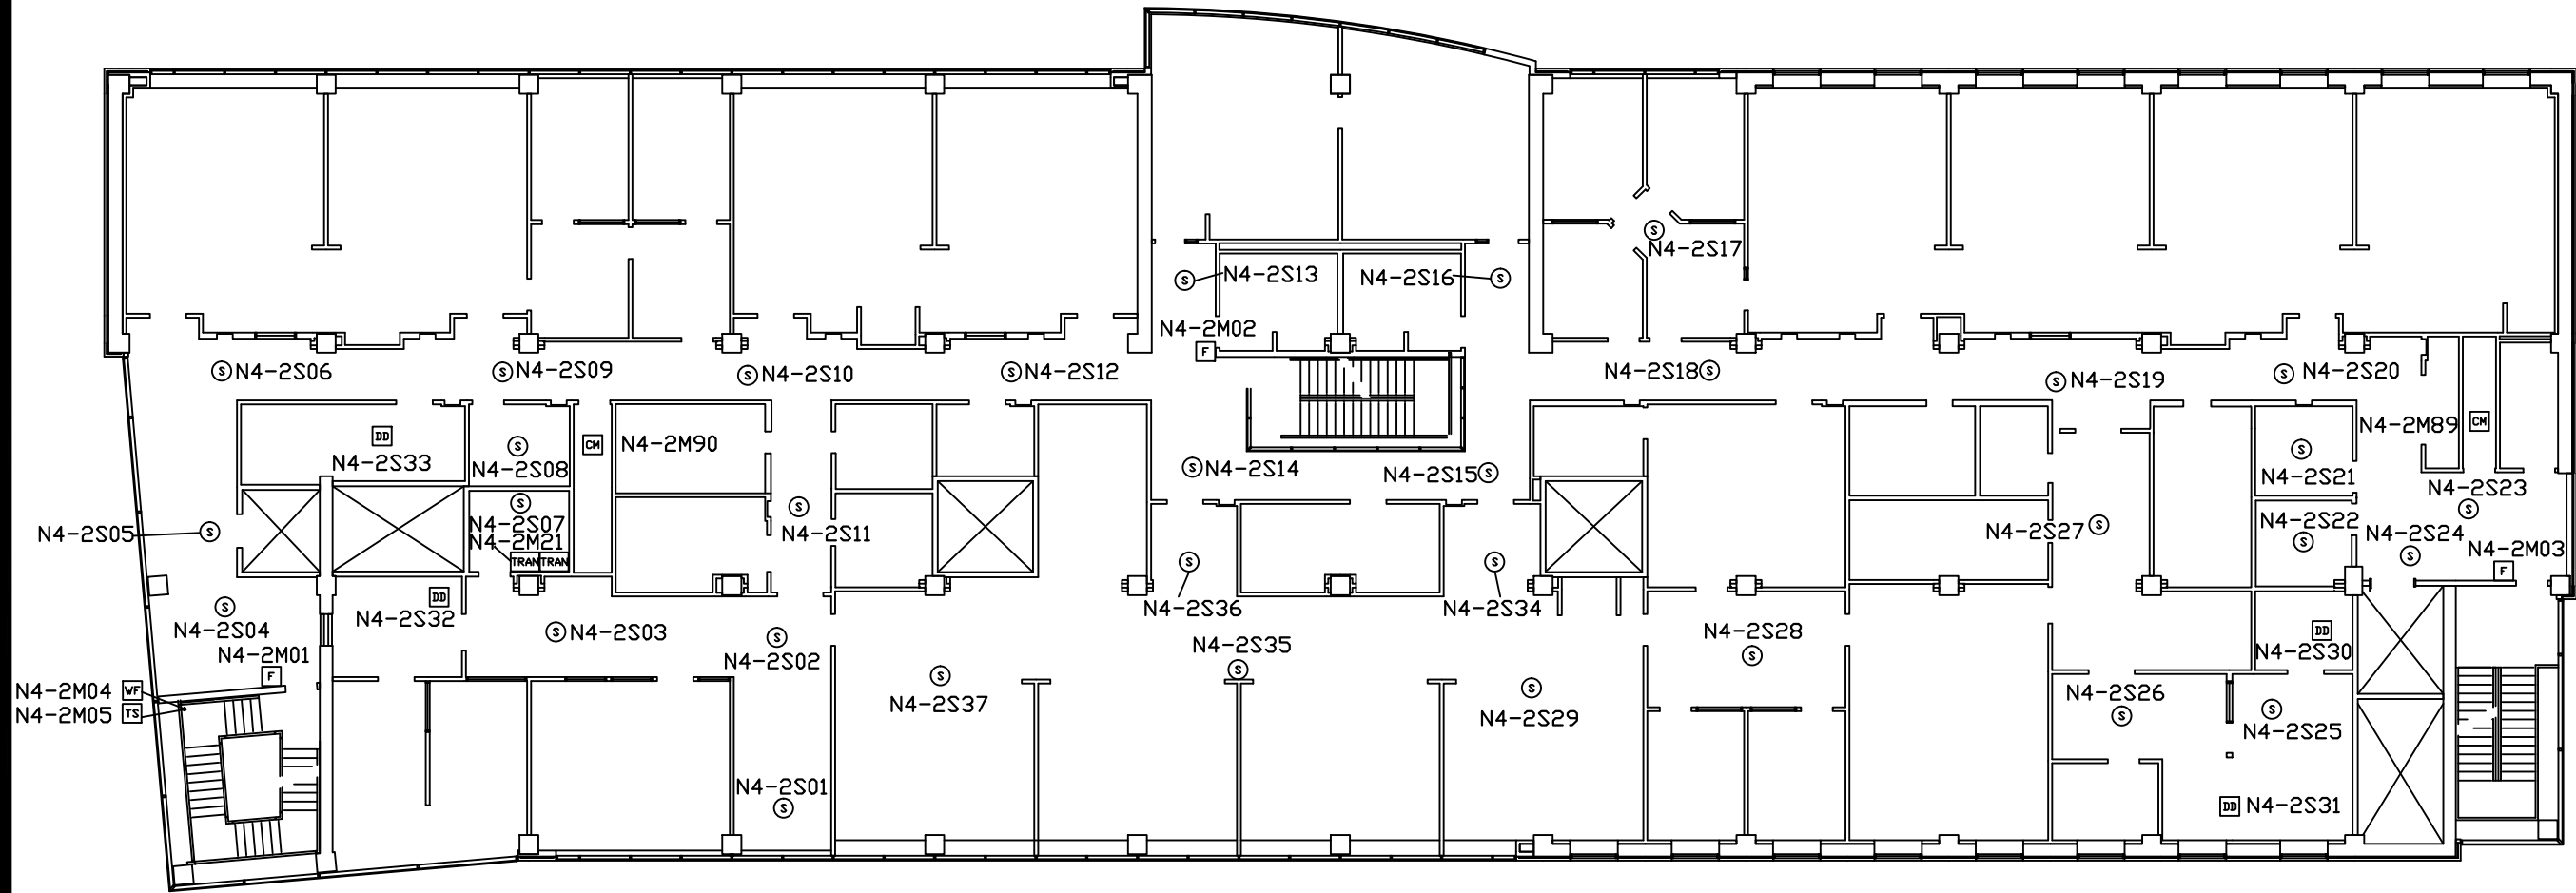

NOTE:
NFS DRAWINGS ARE BASED ON THE PROJECT
ARCHITECT/ENGINEER (A/E) PLANS AND SPECIFICATIONS
FURNISHED TO NFS. A/E IS SOLELY RESPONSIBLE
(NOT NFS) FOR THE TYPE, SIZE, LOCATION, AND
SUITABILITY OF ALL FIRE ALARMS, CONTROL PANELS,
AND OTHER DEVICES SHOWN ON THE A/E PLANS.
NFS DRAWINGS ARE TO SHOW ONLY THE WIRING
DIAGRAMS BETWEEN FIRE ALARM DEVICES AND
CONTROL PANELS. NFS IS NOT RESPONSIBLE FOR
THE INFORMATION SHOWN ON THE A/E PLANS.

EMMA ECCLES JONES
MEDICAL SCIENCE BUILDING
UNIVERSITY OF UTAH HEALTH SCIENCE
THIRD FLOOR
15 NORTH MEDICAL DRIVE EAST
SALT LAKE CITY, UTAH

NFS

NELSON FIRE SYSTEMS
801-468-8300

DRAWN BY: DPS
DESIGNED BY: XXXX
APPROVED BY: TCT
DATE: 12/28/2005
SCALE: N.T.S.
PROJECT NO: XXXX
REV NO: XXXX
DRAWING NAME: MEDSCIENCE3.DWG

FIRE ALARM SYSTEM


THIRD FLOOR
ADDRESSABLE LOOP NUMBERS



NFS:
FA-3-04

DEVICE LEGEND

SYMBOL	DESCRIPTION
Ⓢ	SMOKE DETECTOR W/BASE
ⓕ	MANUAL PULL STATION
ⓓⓓ	DUCT SMOKE DETECTOR
Ⓦⓕ	WATERFLOW SWITCH MONITOR MODULE
ⓉⓈ	TAMPER SWITCH MONITOR MODULE
ⓐⓂ	CONTROL MODULE
Ⓡⓐ	REMOTE ANNUNCIATOR ENCLOSURE
ⓕⓐⓐⓕ	FIRE ALARM CONTROL PANEL
ⓉⓇⓐⓃ	TRANSPONDER PANEL

ADDRESS LABEL CLARIFICATION

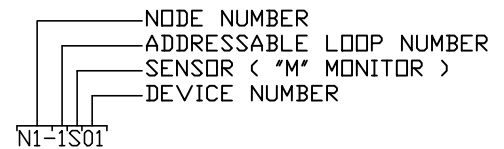

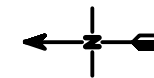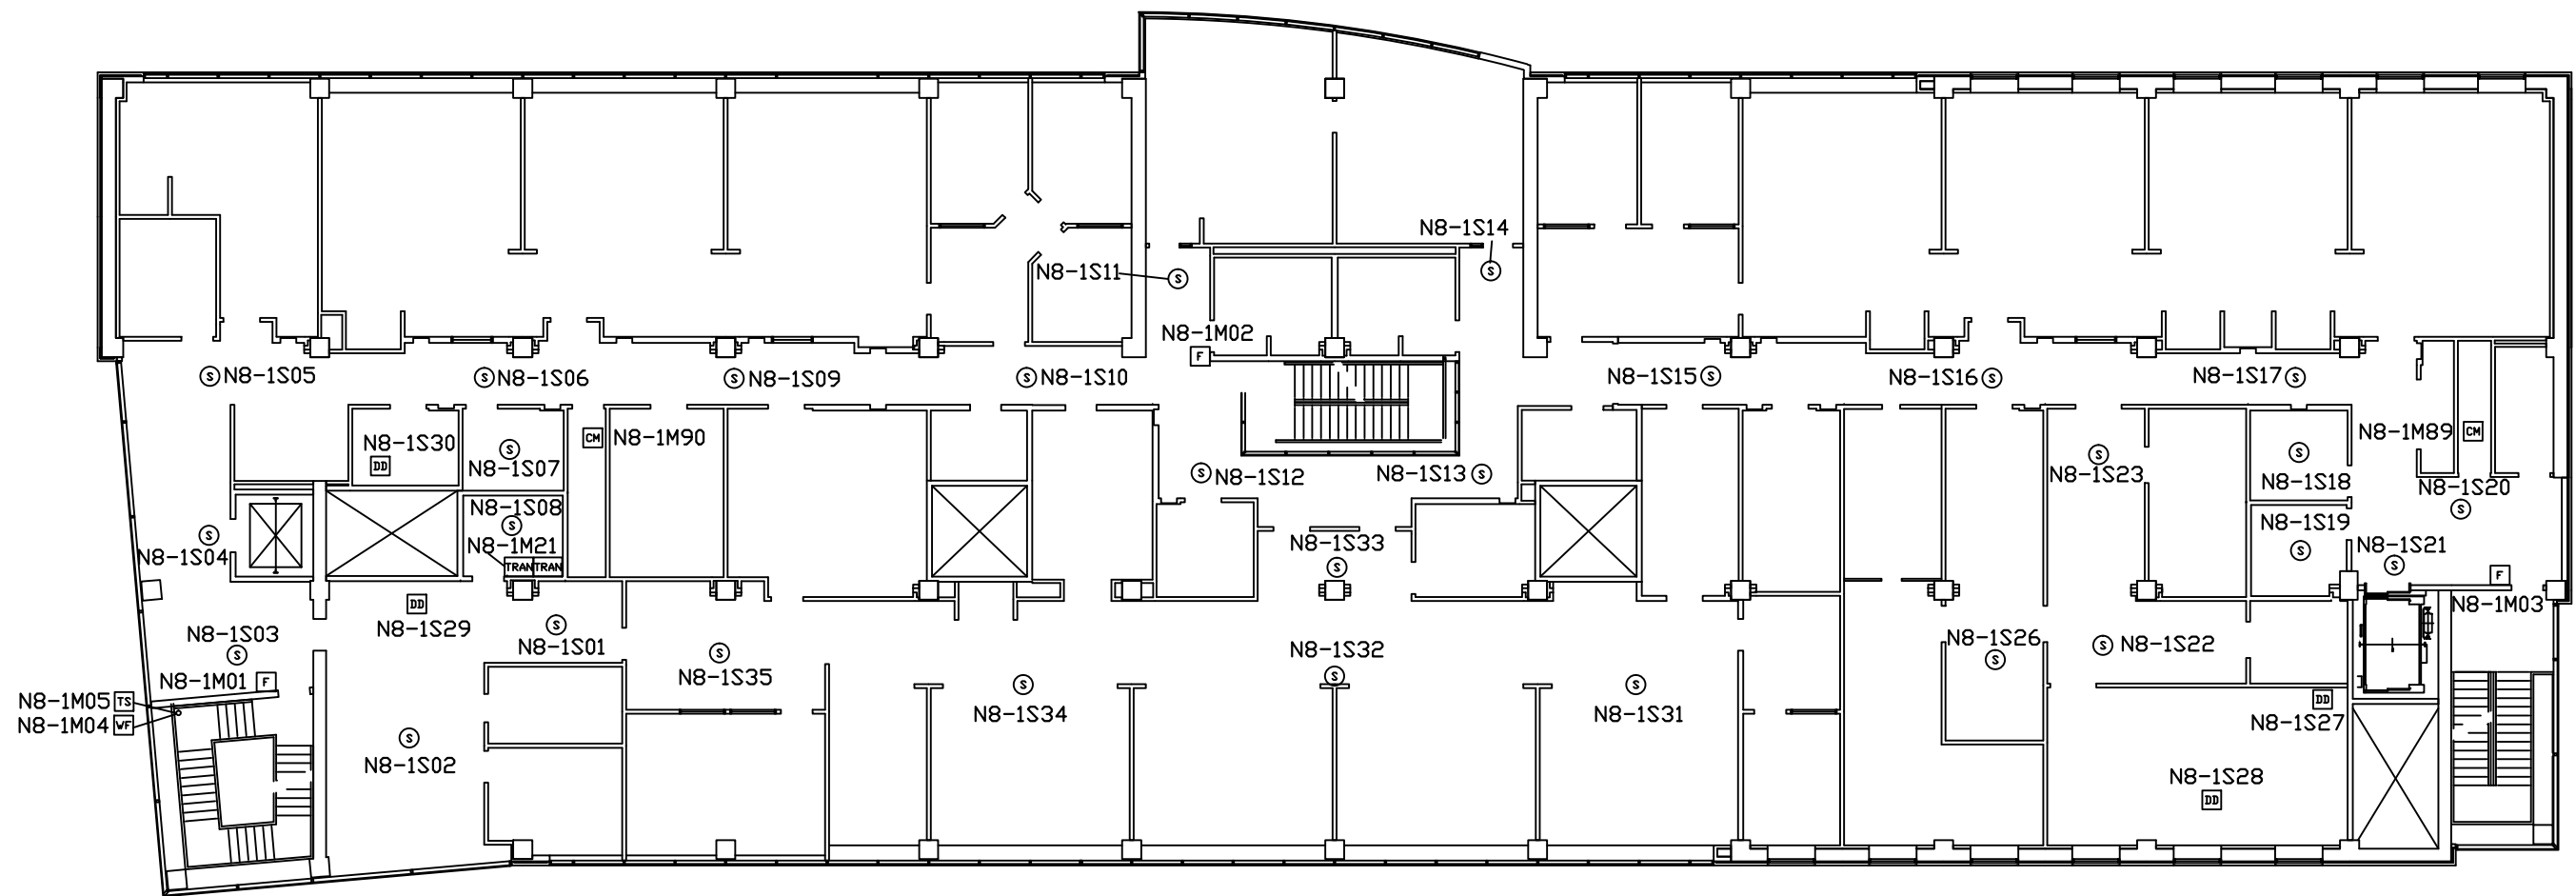

NOTE:
NFS DRAWINGS ARE BASED ON THE PROJECT
ARCHITECT/ENGINEER (A/E) PLANS AND SPECIFICATIONS
FURNISHED TO NFS. A/E IS SOLELY RESPONSIBLE
(NOT NFS) FOR THE TYPE, SIZE, LOCATION, AND
SUITABILITY OF ALL FIRE ALARMS, CONTROL PANELS,
AND OTHER DEVICES SHOWN ON THE A/E PLANS.
NFS DRAWINGS ARE TO SHOW ONLY THE WIRING
DIAGRAMS BETWEEN FIRE ALARM DEVICES AND
CONTROL PANELS. NFS IS NOT RESPONSIBLE FOR
THE INFORMATION SHOWN ON THE A/E PLANS.

EMMA ECCLES JONES
MEDICAL SCIENCE BUILDING
UNIVERSITY OF UTAH HEALTH SCIENCE
FOURTH FLOOR
15 NORTH MEDICAL DRIVE EAST
SALT LAKE CITY, UTAH

NFS

NELSON FIRE SYSTEMS
801-468-8300

DRAWN BY: DPS
DESIGNED BY: XXXX
APPROVED BY: TCT
DATE: 12/28/2005
SCALE: N.T.S.
PROJECT NO: XXXX
REV NO: XXXX
DRAWING NAME: MEDSCIENCE4.DWG

FIRE ALARM SYSTEM

FOURTH FLOOR
ADDRESSABLE LOOP NUMBERS


NFS


FA-4-04

DEVICE LEGEND


SYMBOL	DESCRIPTION
Ⓢ	SMOKE DETECTOR W/BASE
F	MANUAL PULL STATION
DD	DUCT SMOKE DETECTOR
WF	WATERFLOW SWITCH MONITOR MODULE
TS	TAMPER SWITCH MONITOR MODULE
CM	CONTROL MODULE
RA	REMOTE ANNUNCIATOR ENCLOSURE
FACP	FIRE ALARM CONTROL PANEL
TRAN	TRANSPONDER PANEL



ADDRESS LABEL CLARIFICATION

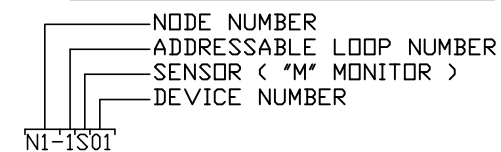


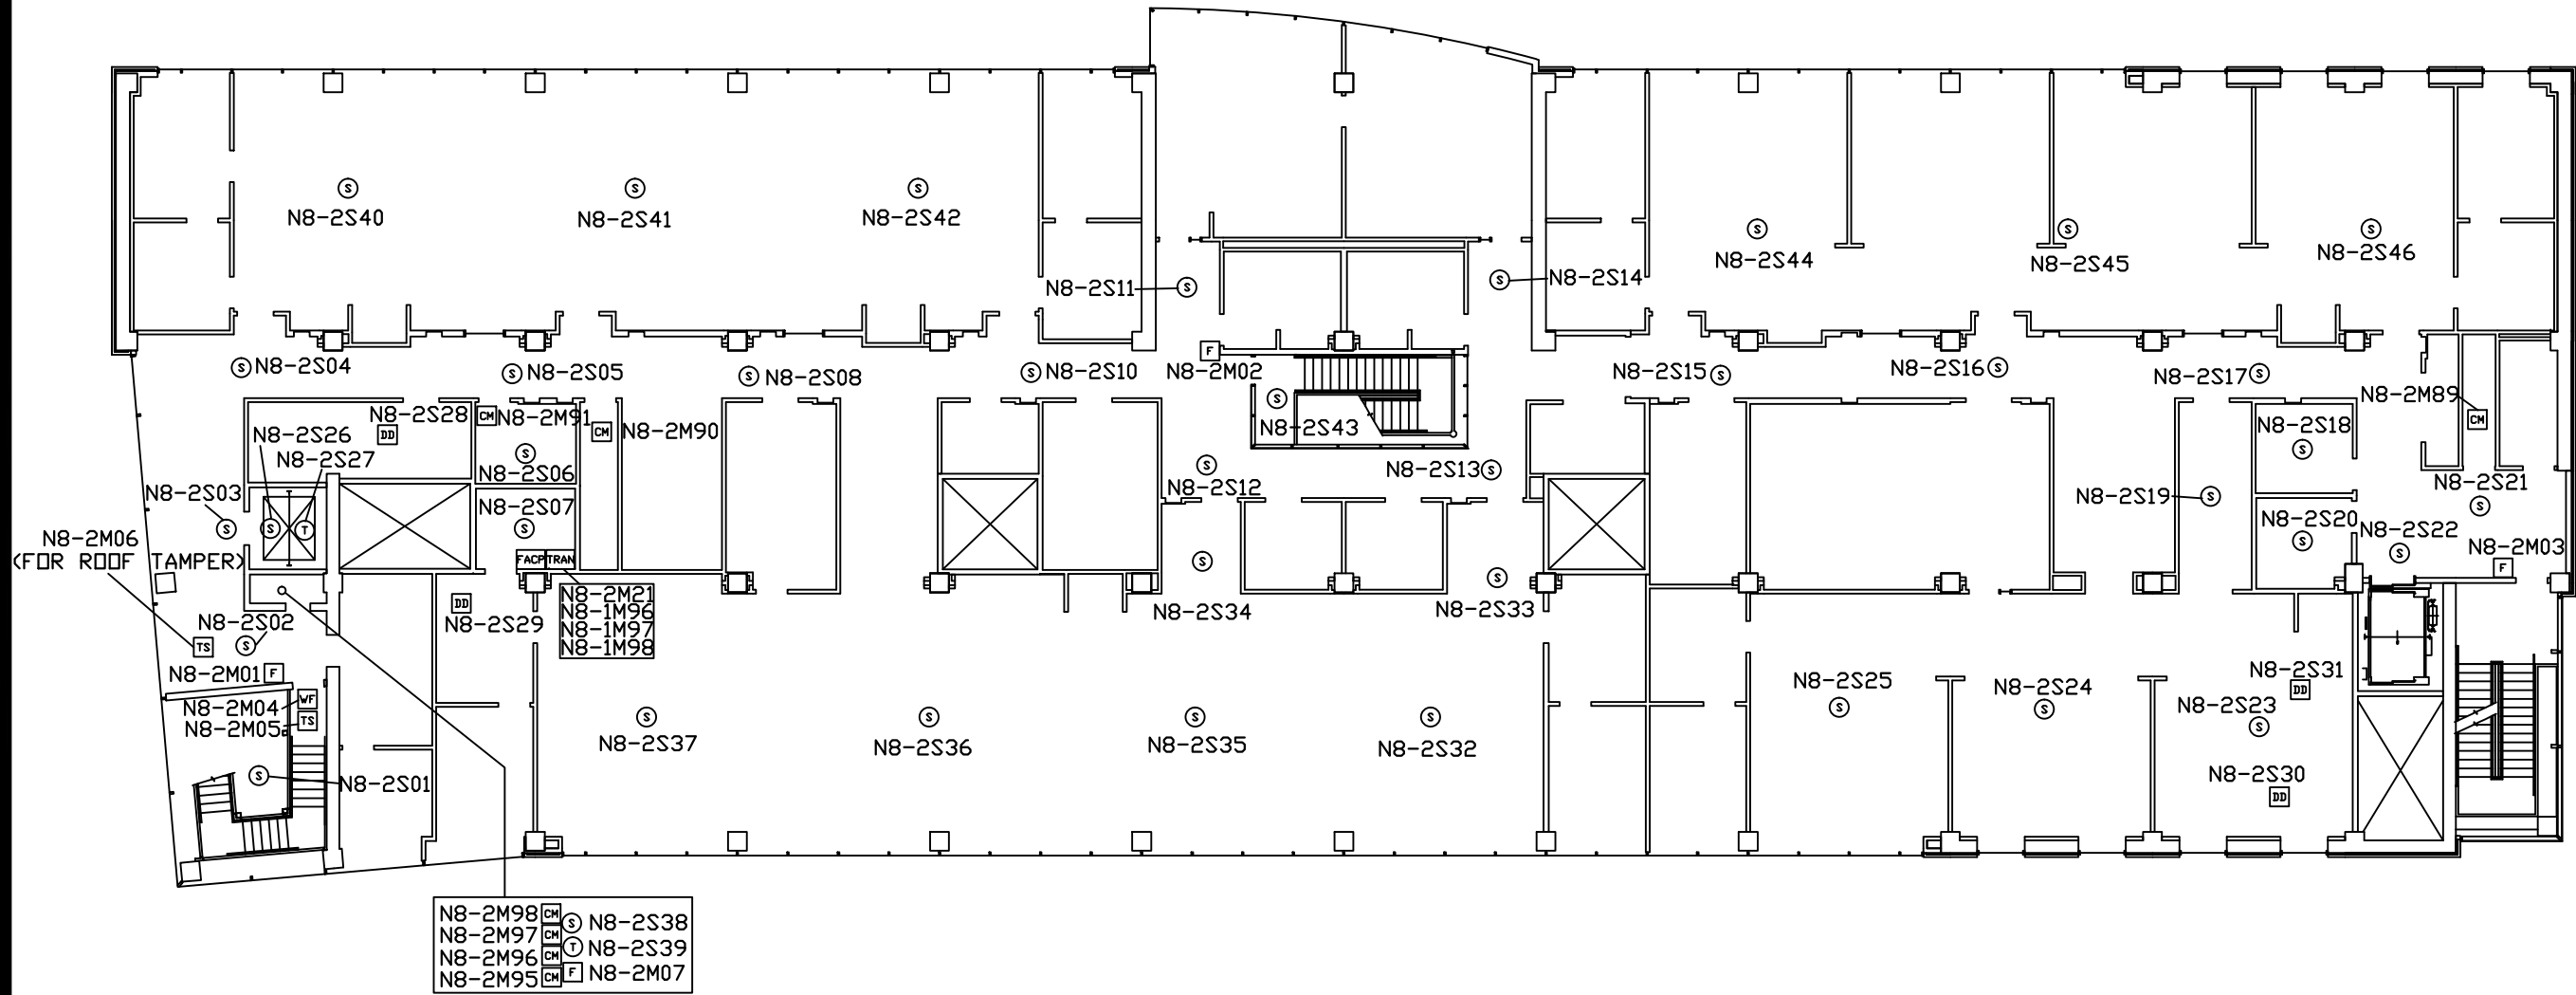


DEVICE LEGEND	
SYMBOL	DESCRIPTION
Ⓢ	SMOKE DETECTOR W/BASE
Ⓛ	MANUAL PULL STATION
ⓁⓁ	DUCT SMOKE DETECTOR
ⓁⓂ	WATERFLOW SWITCH MONITOR MODULE
Ⓜ	TAMPER SWITCH MONITOR MODULE
ⓈⓂ	CONTROL MODULE
ⓈⓂⓈ	REMOTE ANNUNCIATOR ENCLOSURE
ⓈⓈⓈ	FIRE ALARM CONTROL PANEL
ⓈⓈⓈⓈ	TRANSPONDER PANEL

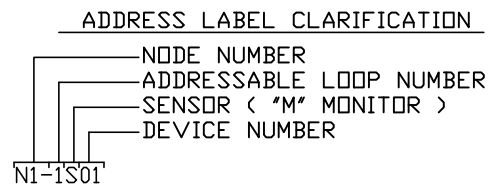

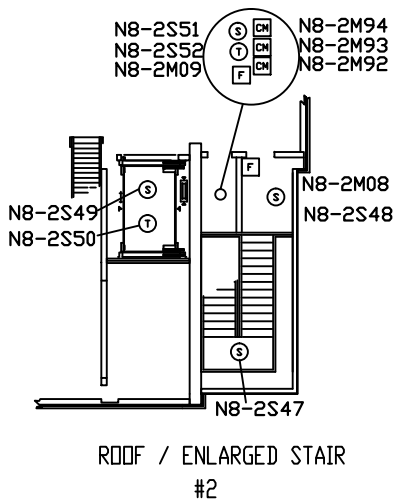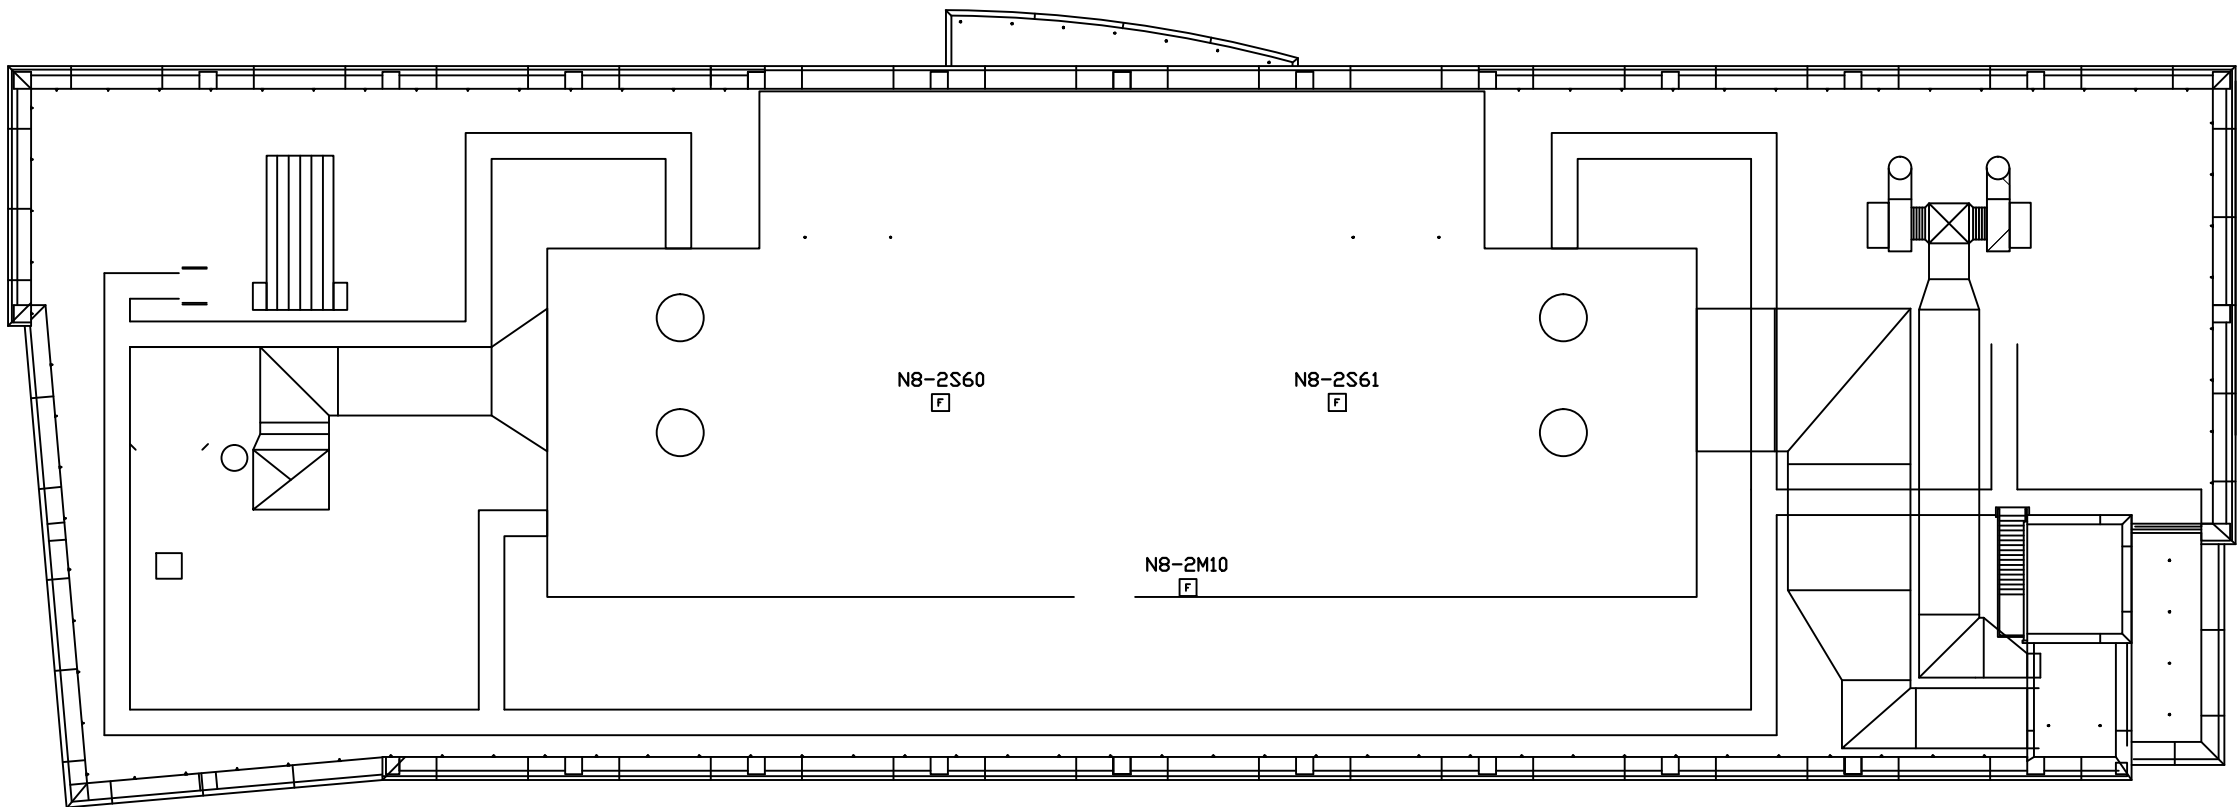

DEVICE LEGEND	
SYMBOL	DESCRIPTION
Ⓢ	SMOKE DETECTOR W/BASE
F	MANUAL PULL STATION
DU	DUCT SMOKE DETECTOR
WF	WATERFLOW SWITCH MONITOR MODULE
TS	TAMPER SWITCH MONITOR MODULE
CM	CONTROL MODULE
RA	REMOTE ANNUNCIATOR ENCLOSURE
FACP	FIRE ALARM CONTROL PANEL
TRAN	TRANSPONDER PANEL

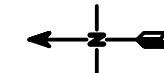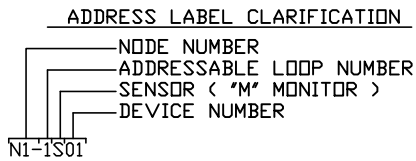

NOTE:
NFS DRAWINGS ARE BASED ON THE PROJECT
ARCHITECT/ENGINEER (A/E) PLANS AND SPECIFICATIONS
FURNISHED TO NFS. A/E IS SOLELY RESPONSIBLE
(NOT NFS) FOR THE TYPE, SIZE, LOCATION, AND
SUITABILITY OF ALL FIRE ALARMS, CONTROL PANELS,
AND OTHER DEVICES SHOWN ON THE A/E PLANS.
NFS DRAWINGS ARE TO SHOW ONLY THE WIRING
DIAGRAMS BETWEEN FIRE ALARM DEVICES AND
CONTROL PANELS. NFS IS NOT RESPONSIBLE FOR
THE INFORMATION SHOWN ON THE A/E PLANS.

EMMA ECCLES JONES
MEDICAL SCIENCE BUILDING
UNIVERSITY OF UTAH HEALTH SCIENCE
ROOF
15 NORTH MEDICAL DRIVE EAST
SALT LAKE CITY, UTAH

NFS
NELSON FIRE SYSTEMS
801-468-8300



DRAWN BY:	DPS
DESIGNED BY:	XXXX
APPROVED BY:	TCT
DATE:	12/28/2005
SCALE:	N.T.S.
PROJECT NO:	XXXX
REV NO:	XXXX
DRAWING NAME:	MEDSCIENCE6.DWG

FIRE ALARM SYSTEM
ROOF
ADDRESSABLE LOOP NUMBERS

NFS
FA-R-04

BASEMENT
MEZZANINE

ADDRESS LABEL CLARIFICATION

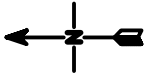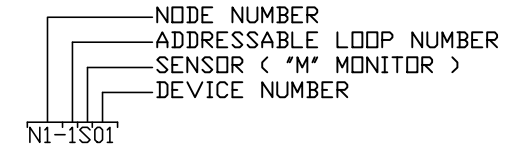

NOTE:
NFS DRAWINGS ARE BASED ON THE PROJECT
ARCHITECT/ENGINEER (A/E) PLANS AND SPECIFICATIONS
FURNISHED TO NFS. A/E IS SOLELY RESPONSIBLE
(NOT NFS) FOR THE TYPE, SIZE, LOCATION, AND
SUITABILITY OF ALL FIRE ALARMS, CONTROL PANELS,
AND OTHER DEVICES SHOWN ON THE A/E PLANS.
NFS DRAWINGS ARE TO SHOW ONLY THE WIRING
DIAGRAMS BETWEEN FIRE ALARM DEVICES AND
CONTROL PANELS. NFS IS NOT RESPONSIBLE FOR
THE INFORMATION SHOWN ON THE A/E PLANS.

EMMA ECCLES JONES
MEDICAL SCIENCES BUILDING
UNIVERSITY OF UTAH HEALTH SCIENCES
BASEMENT
15 NORTH MEDICAL DRIVE EAST
SALT LAKE CITY, UTAH

NFS

NELSON FIRE SYSTEMS
801-468-8300

DRAWN BY: DS
DESIGNED BY: XXXX
APPROVED BY: TT
DATE: 8/16/07
SCALE: N.T.S.
PROJECT NO: XXXX
REV NO: XXXX
DRAWING NAME:
MEDSCIENCEB.DWG

FIRE ALARM SYSTEM

BASEMENT
ADDRESSABLE LOOP NUMBERS

NFS

FA-B-04

DEVICE LEGEND

SYMBOL	DESCRIPTION
Ⓢ	SMOKE DETECTOR W/BASE
Ⓣ	THERMAL DETECTOR
F	MANUAL PULL STATION
Ⓛ	DUCT SMOKE DETECTOR
WF	WATERFLOW SWITCH MONITOR MODULE
TS	TAMPER SWITCH MONITOR MODULE
M	MONITOR MODULE
CM	CONTROL MODULE
FACP	FIRE ALARM CONTROL PANEL
TRAN	TRANSPONDER PANEL

