


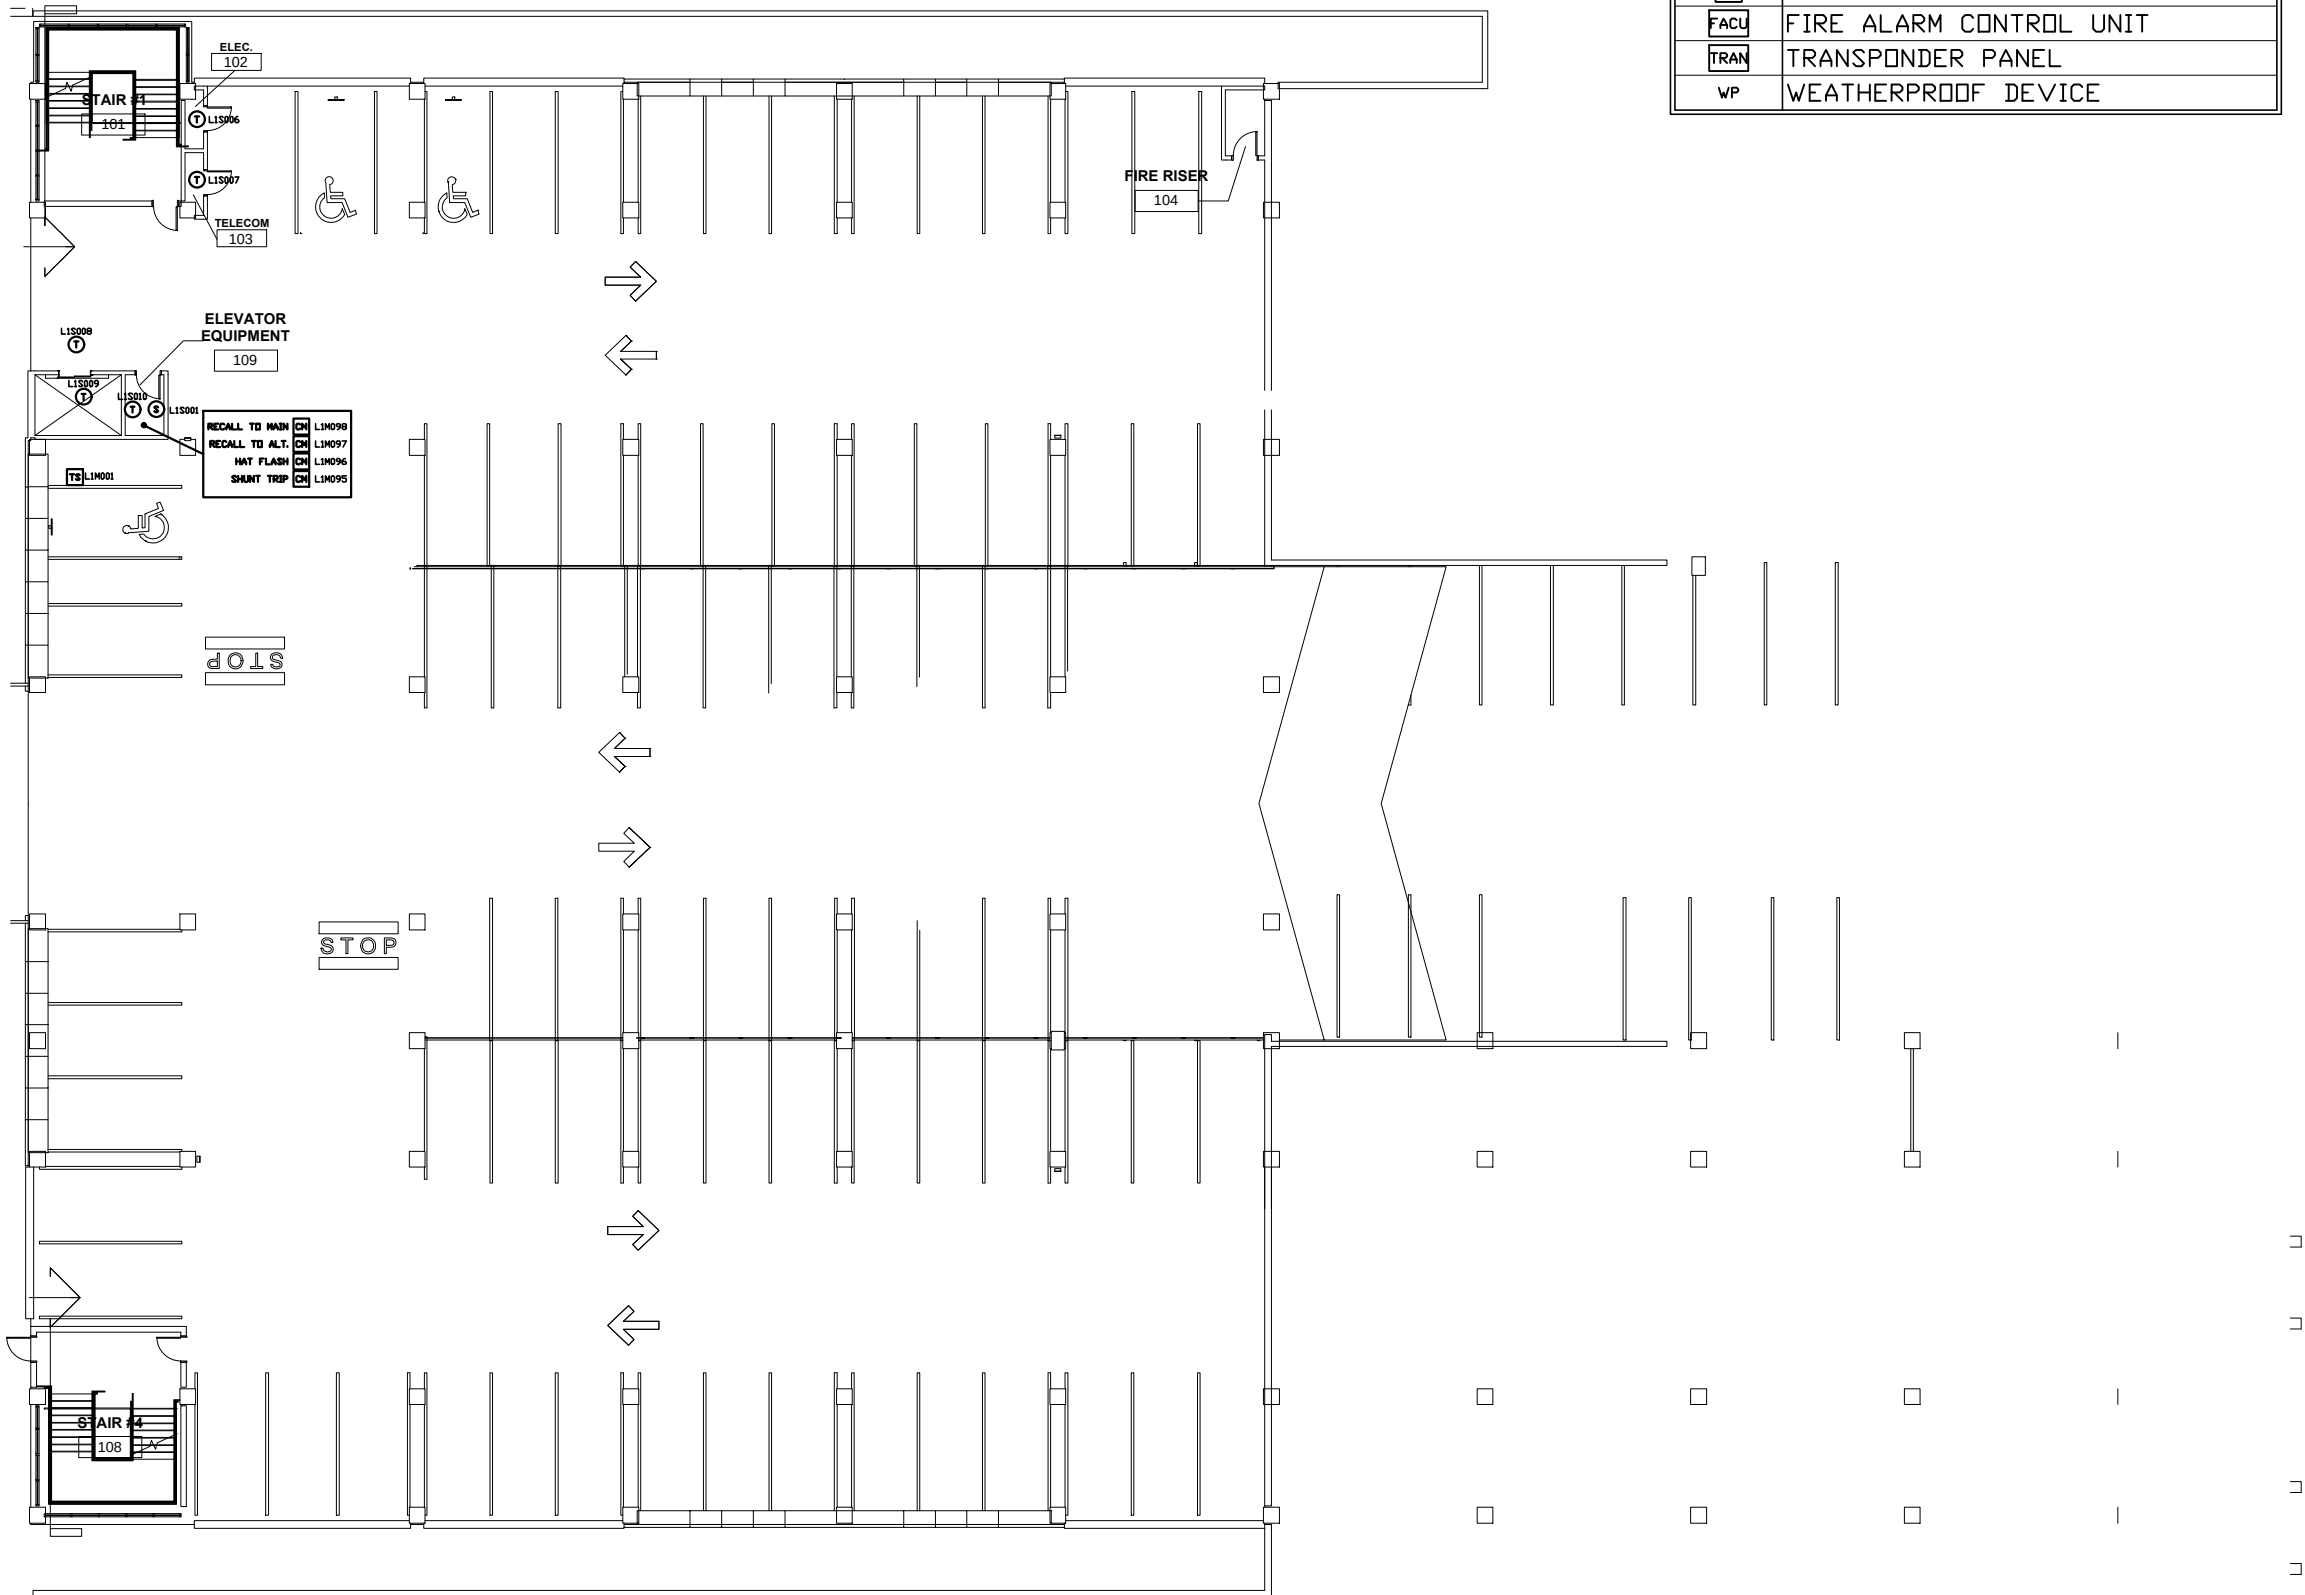

DEVICE LEGEND	
SYMBOL	DESCRIPTION
(S)	SMOKE DETECTOR
(T)	HEAT DETECTOR
(TS)	TAMPER SWITCH
FACU	FIRE ALARM CONTROL UNIT
TRAN	TRANSPONDER PANEL
WP	WEATHERPROOF DEVICE



NOTE:
NFS DRAWINGS ARE BASED ON THE PROJECT
NFS ARCHITECTURE/ENGINEER (A/E) PLANS AND
SPECIFICATIONS FURNISHED TO NFS. A/E IS SOLELY
RESPONSIBLE (NOT NFS) FOR THE TYPE, SIZE,
LOCATION, AND SUITABILITY OF ALL FIRE ALARMS,
CONTROL PANELS, AND OTHER DEVICES SHOWN ON
THE A/E PLANS. NFS DRAWINGS ARE TO SHOW ONLY
THE WIRING DIAGRAMS BETWEEN FIRE ALARM
DEVICES AND CONTROL PANELS. NFS IS NOT
RESPONSIBLE FOR THE INFORMATION SHOWN ON THE
A/E PLANS.

UNIVERSITY OF UTAH
HEALTH SCIENCE PARKING STRUCTURE
LEVEL I
SALT LAKE CITY, UTAH 84112
FIRE ALARM SYSTEM

NFS

NELSON FIRE SYSTEMS
801-468-8300

DRAWN BY:	BDT
DESIGNED BY:	XXXX
APPROVED BY:	DS
DATE:	3/20/2017
SCALE:	(ARCH D) 1/16" = 1'
PROJECT NO:	XXXX
REVISION NO:	XXXX
DRAWING NAME:	U OF U HS PARKING S LVL I.DWG



NELSON FIRE SYSTEMS

LEVEL I

NUMBERS

PAGE:

FA-I-02

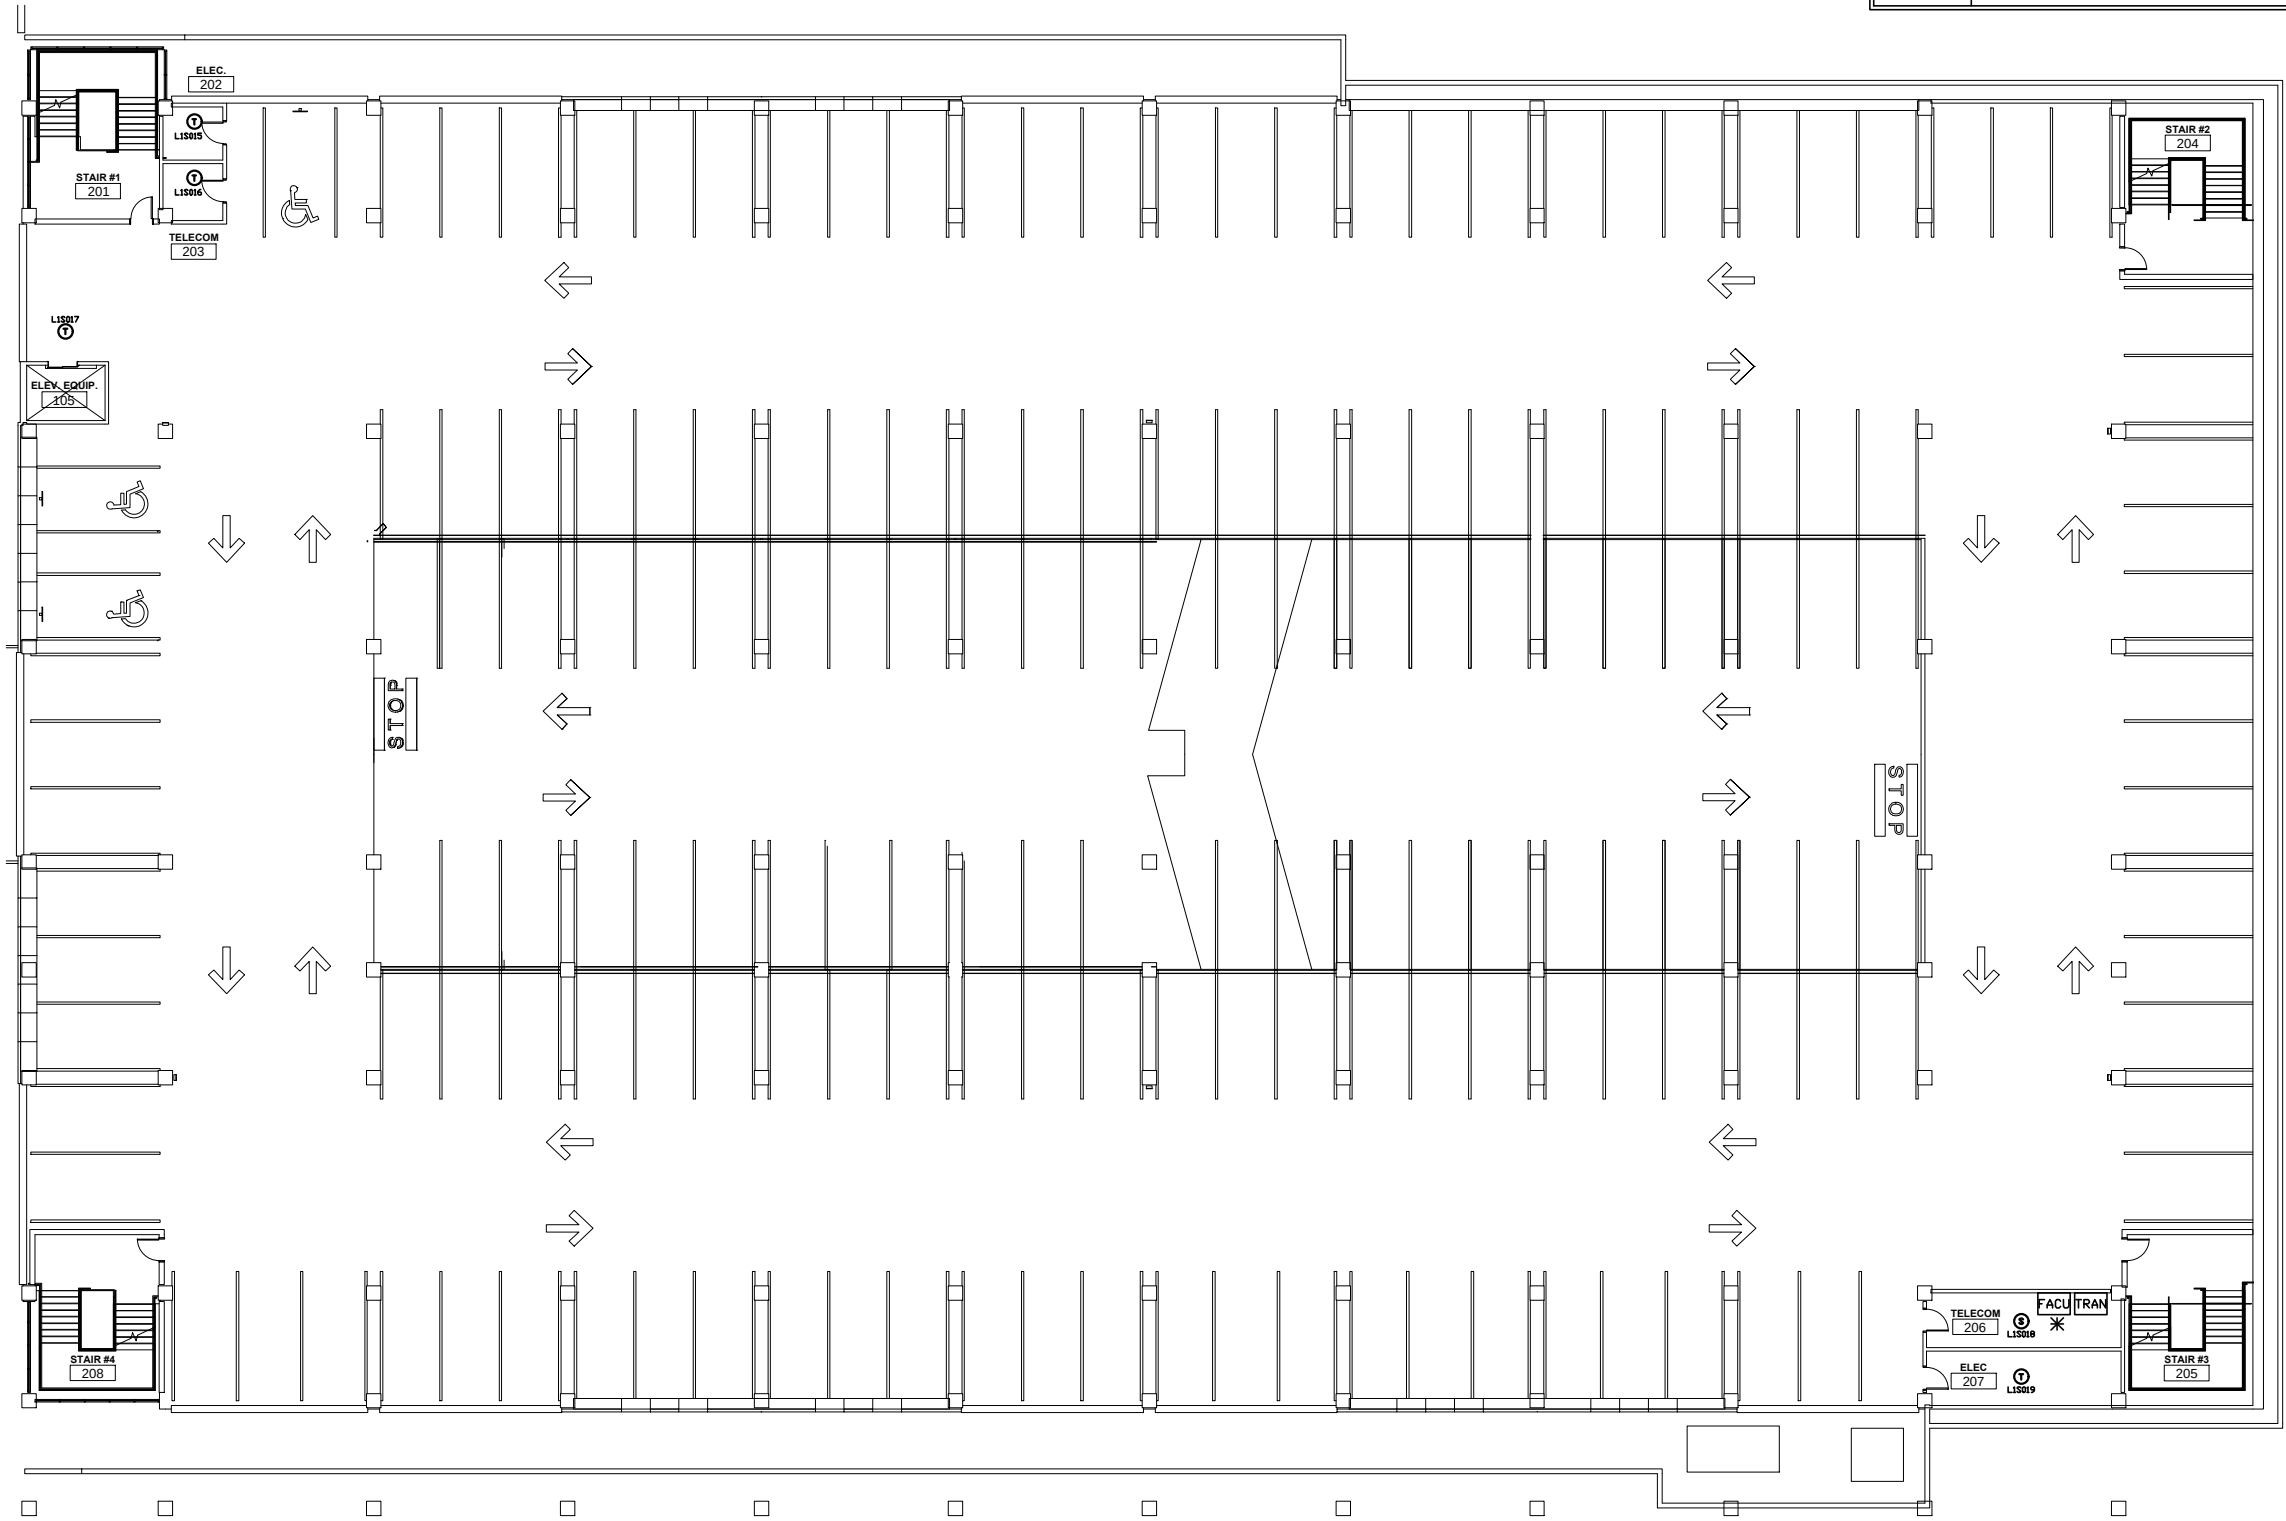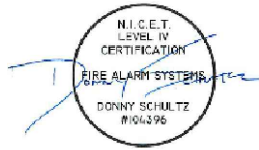

DEVICE LEGEND	
SYMBOL	DESCRIPTION
(S)	SMOKE DETECTOR
(T)	HEAT DETECTOR
TS	TAMPER SWITCH
FACU	FIRE ALARM CONTROL UNIT
TRAN	TRANSPONDER PANEL
WP	WEATHERPROOF DEVICE


NOTE: NFS DRAWINGS ARE BASED ON THE PROJECT ARCHITECTURE/ENGINEER (A/E) PLANS AND SPECIFICATIONS FURNISHED TO NFS. A/E IS SOLELY RESPONSIBLE (NOT NFS) FOR THE TYPE, SIZE, LOCATION, AND SUITABILITY OF ALL FIRE ALARMS CONTROL PANELS, AND OTHER DEVICES SHOWN ON THE A/E PLANS. NFS DRAWINGS ARE TO SHOW ONLY THE WIRING DIAGRAMS BETWEEN FIRE ALARM DEVICES AND CONTROL PANELS. NFS IS NOT RESPONSIBLE FOR THE INFORMATION SHOWN ON THE A/E PLANS.

UNIVERSITY OF UTAH
HEALTH SCIENCE PARKING STRUCTURE
LEVEL 2
SALT LAKE CITY, UTAH 84112
FIRE ALARM SYSTEM


NFS
NELSON FIRE SYSTEMS
801-468-8300

DRAWN BY:	BDT
DESIGNED BY:	XXXX
APPROVED BY:	DS
DATE:	3/20/2017
SCALE:	(ARCH D) 1/16" = 1'
PROJECT NO:	XXXX
REVISION NO:	XXXX
DRAWING NAME:	U OF U HS PARKING S LVL 2.DWG

NELSON FIRE SYSTEMS
LEVEL 2
NUMBERS

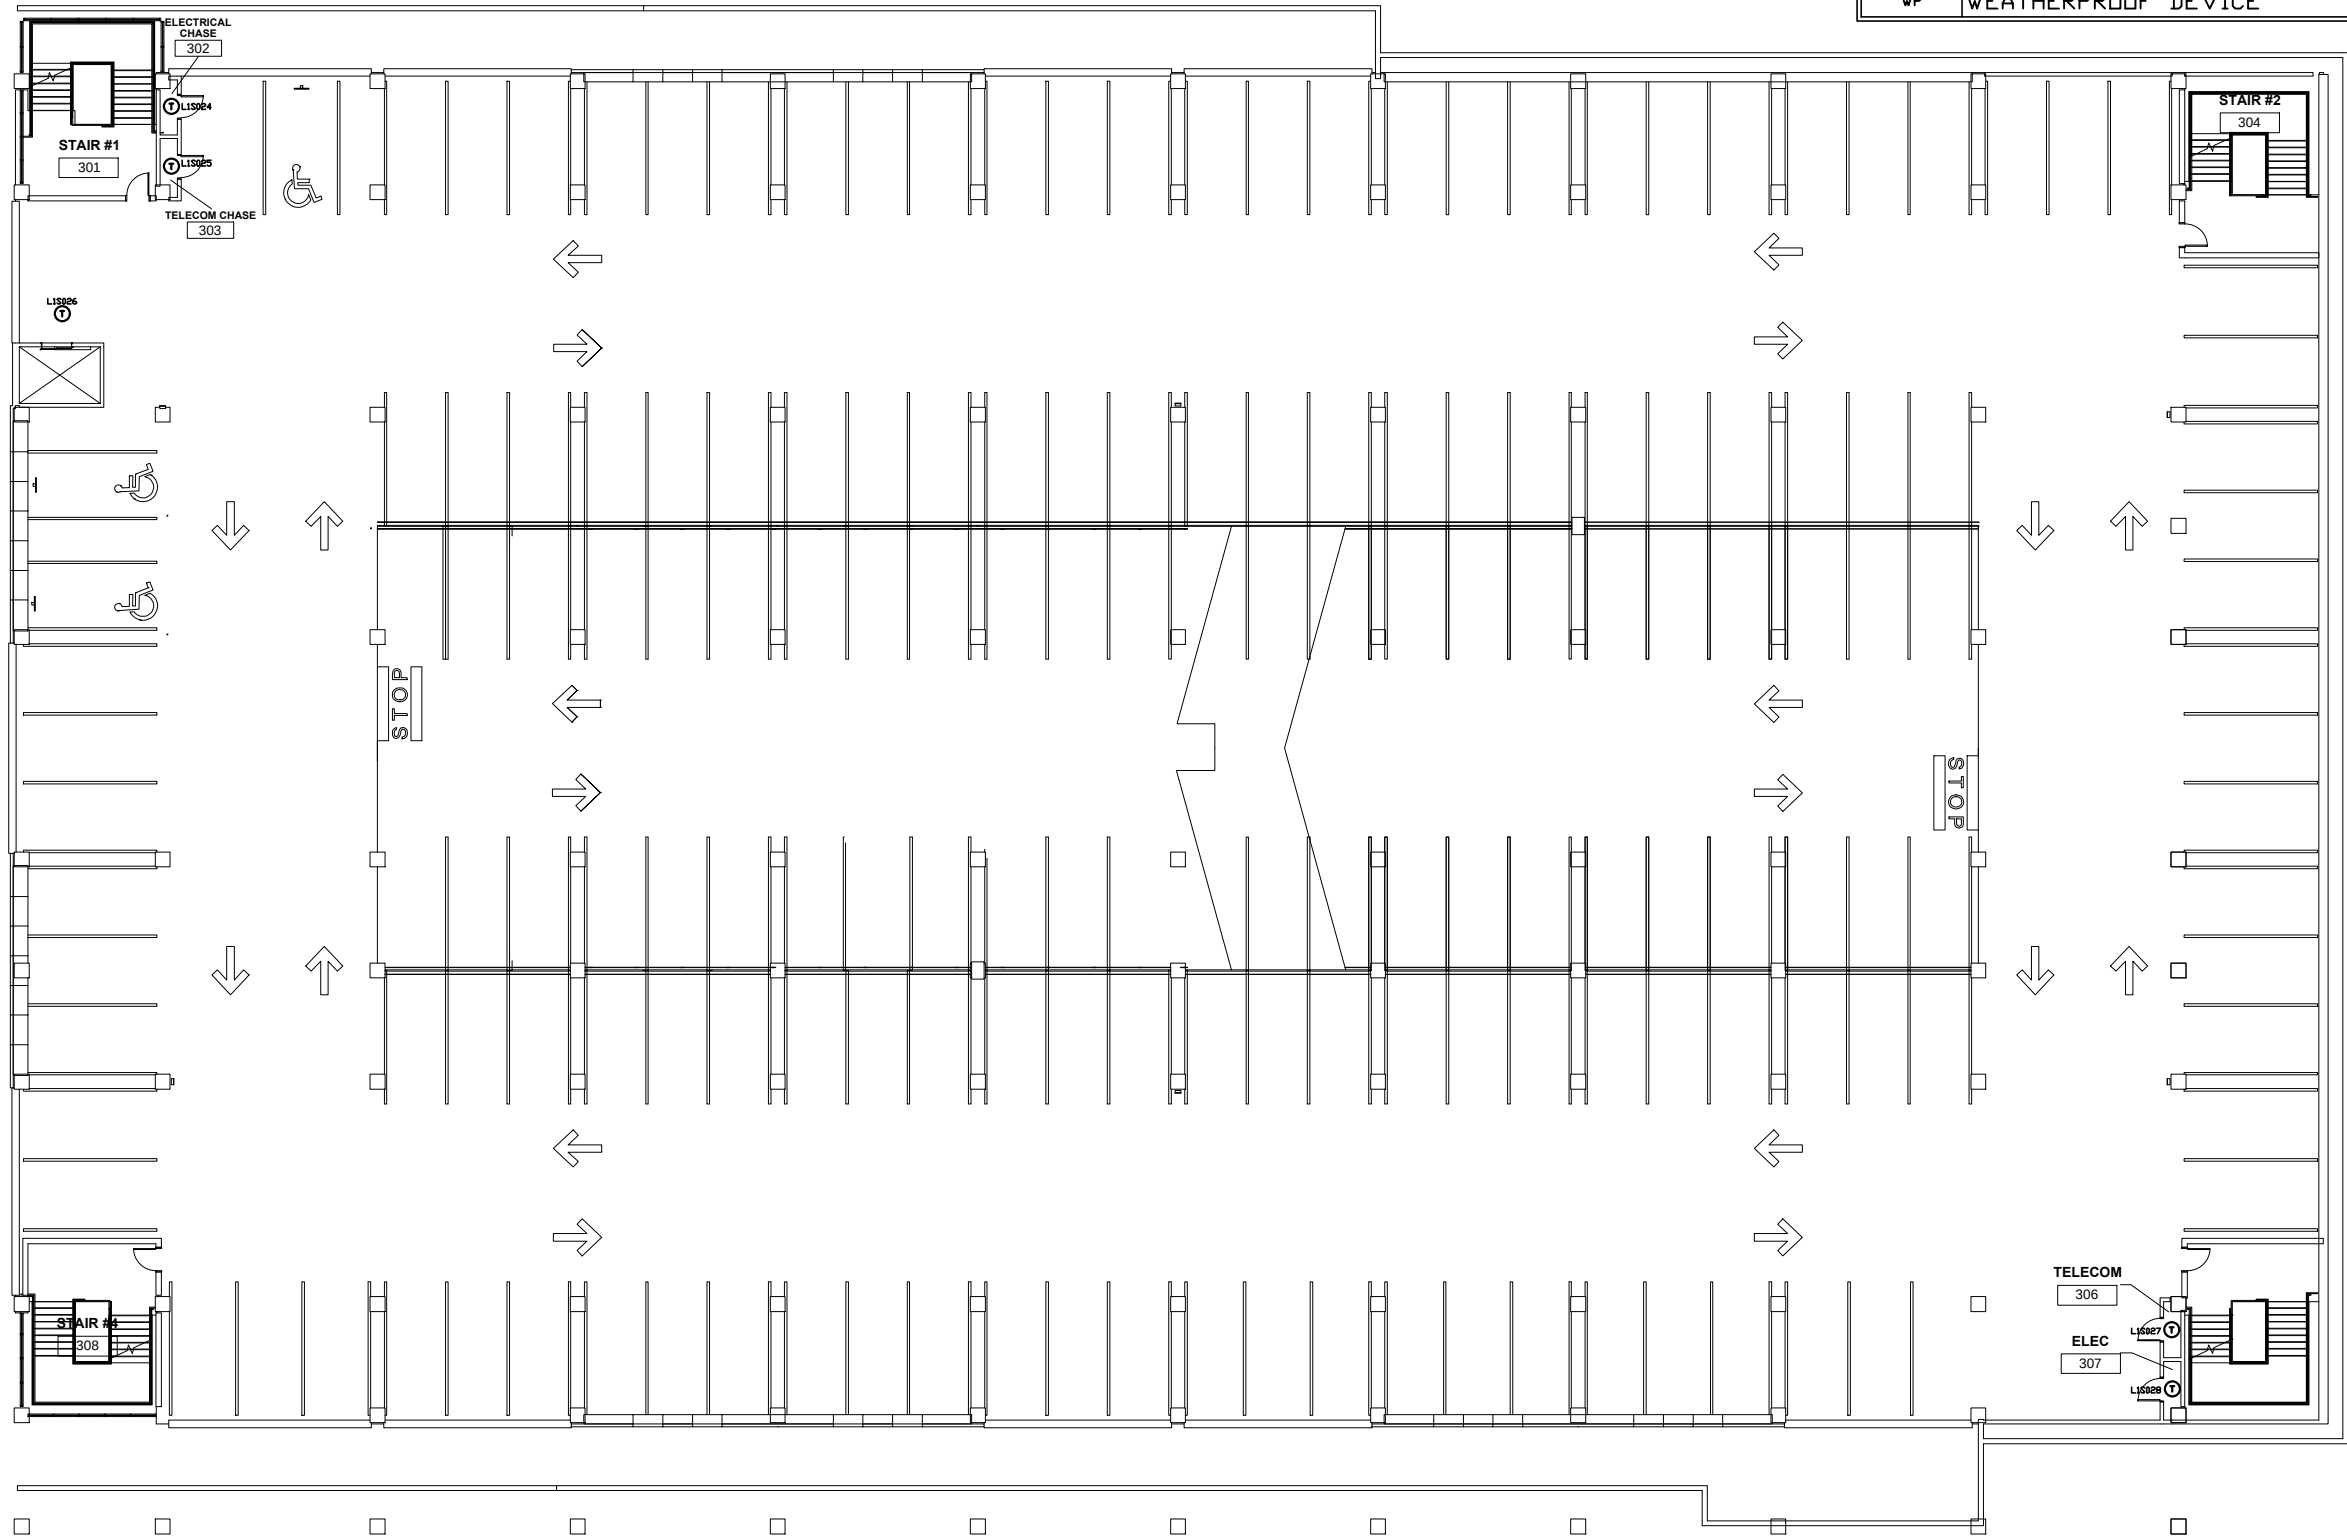

DEVICE LEGEND	
SYMBOL	DESCRIPTION
Ⓢ	SMOKE DETECTOR
Ⓣ	HEAT DETECTOR
Ⓣs	TAMPER SWITCH
FACU	FIRE ALARM CONTROL UNIT
TRAN	TRANSPONDER PANEL
WP	WEATHERPROOF DEVICE

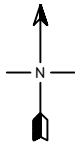

NOTE: NFS DRAWINGS ARE BASED ON THE PROJECT ARCHITECTURE/ENGINEER (A/E) PLANS AND SPECIFICATIONS FURNISHED TO NFS. A/E IS SOLELY RESPONSIBLE (NOT NFS) FOR THE TYPE, SIZE, LOCATION, AND SUITABILITY OF ALL FIRE ALARMS, CONTROL PANELS, AND OTHER DEVICES SHOWN ON THE A/E PLANS. NFS DRAWINGS ARE TO SHOW ONLY THE WIRING DIAGRAMS BETWEEN FIRE ALARM DEVICES AND CONTROL PANELS. NFS IS NOT RESPONSIBLE FOR THE INFORMATION SHOWN ON THE A/E PLANS.

UNIVERSITY OF UTAH
HEALTH SCIENCE PARKING STRUCTURE
LEVEL 3
SALT LAKE CITY, UTAH 84112
FIRE ALARM SYSTEM

NFS

NELSON FIRE SYSTEMS
801-468-8300

DRAWN BY: BDT
DESIGNED BY: XXXX
APPROVED BY: DS
DATE: 3/20/2017
SCALE: (ARCH D) 1/16" = 1'
PROJECT NO: XXXX
REVISION NO: XXXX
DRAWING NAME:
U OF U HS PARKING S LVL 3.DWG

NELSON FIRE SYSTEMS


LEVEL 3
NUMBERS

PAGE:

FA-3-02



DEVICE LEGEND	
SYMBOL	DESCRIPTION
(S)	SMOKE DETECTOR
(T)	HEAT DETECTOR
TS	TAMPER SWITCH
FACU	FIRE ALARM CONTROL UNIT
TRAN	TRANSPONDER PANEL
WP	WEATHERPROOF DEVICE

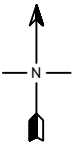

NOTE: NFS DRAWINGS ARE BASED ON THE PROJECT ARCHITECTURE/ENGINEER (A/E) PLANS AND SPECIFICATIONS FURNISHED TO NFS. A/E IS SOLELY RESPONSIBLE (NOT NFS) FOR THE TYPE, SIZE, LOCATION, AND SUITABILITY OF ALL FIRE ALARMS, CONTROL PANELS, AND OTHER DEVICES SHOWN ON THE A/E PLANS. NFS DRAWINGS ARE TO SHOW ONLY THE WIRING DIAGRAMS BETWEEN FIRE ALARM DEVICES AND CONTROL PANELS. NFS IS NOT RESPONSIBLE FOR THE INFORMATION SHOWN ON THE A/E PLANS.

UNIVERSITY OF UTAH
HEALTH SCIENCE PARKING STRUCTURE
LEVEL 4
SALT LAKE CITY, UTAH 84112
FIRE ALARM SYSTEM

NFS

NELSON FIRE SYSTEMS
801-468-8300


DRAWN BY: BDT
DESIGNED BY: XXXX
APPROVED BY: DS
DATE: 3/20/2017
SCALE: (ARCH D) 1/16" = 1'
PROJECT NO: XXXX
REVISION NO: XXXX
DRAWING NAME:
U OF U HS PARKING S LVL 4.DWG


NELSON FIRE SYSTEMS

LEVEL 4
NUMBERS


PAGE:

FA-4-02

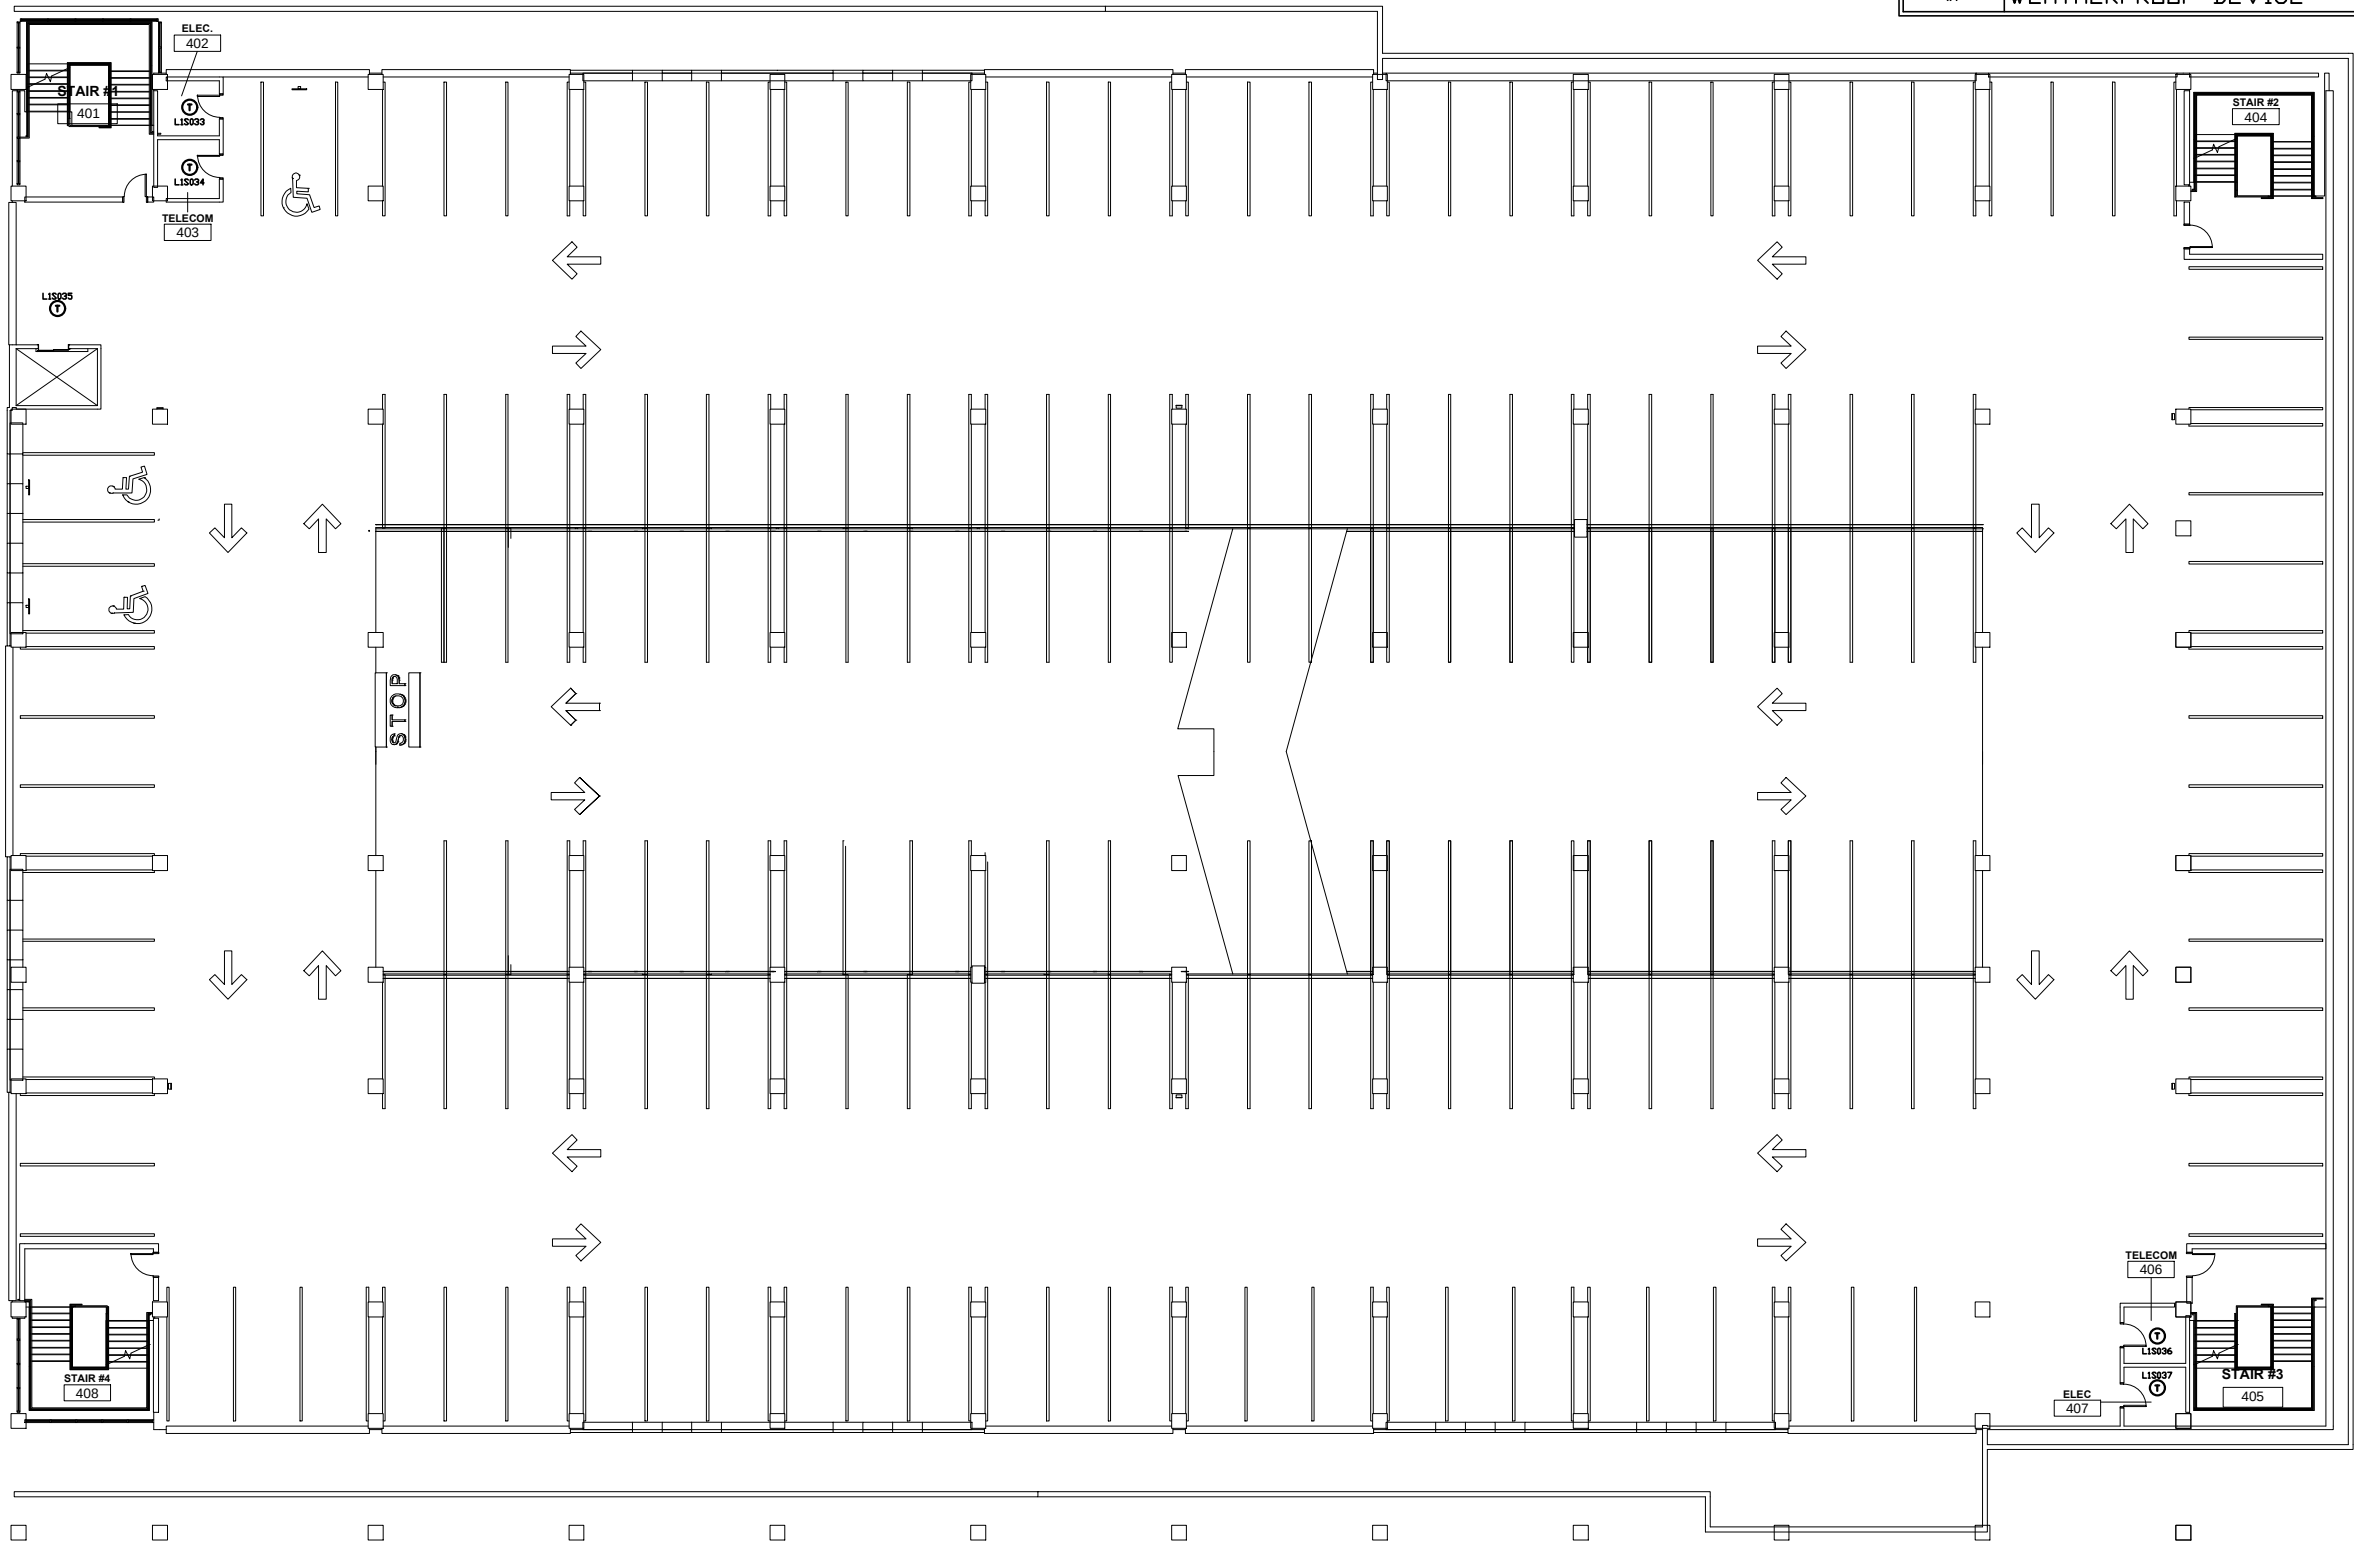

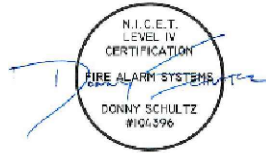

DEVICE LEGEND	
SYMBOL	DESCRIPTION
Ⓢ	SMOKE DETECTOR
Ⓣ	HEAT DETECTOR
TS	TAMPER SWITCH
FACU	FIRE ALARM CONTROL UNIT
TRAN	TRANSPONDER PANEL
WP	WEATHERPROOF DEVICE

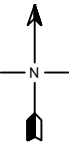

NOTE: NFS DRAWINGS ARE BASED ON THE PROJECT ARCHITECTURE/ENGINEER (A/E) PLANS AND SPECIFICATIONS FURNISHED TO NFS. A/E IS SOLELY RESPONSIBLE (NOT NFS) FOR THE TYPE, SIZE, LOCATION, AND SUITABILITY OF ALL FIRE ALARMS, CONTROL PANELS, AND OTHER DEVICES SHOWN ON THE A/E PLANS. NFS DRAWINGS ARE TO SHOW ONLY THE WIRING DIAGRAMS BETWEEN FIRE ALARM DEVICES AND CONTROL PANELS. NFS IS NOT RESPONSIBLE FOR THE INFORMATION SHOWN ON THE A/E PLANS.

UNIVERSITY OF UTAH
HEALTH SCIENCE PARKING STRUCTURE
LEVEL 5
SALT LAKE CITY, UTAH 84112
FIRE ALARM SYSTEM

NFS


NELSON FIRE SYSTEMS
801-468-8300


DRAWN BY: BDT
DESIGNED BY: XXXX
APPROVED BY: DS
DATE: 3/20/2017
SCALE: (ARCH D) 1/16" = 1'
PROJECT NO: XXXX
REVISION NO: XXXX
DRAWING NAME:
U OF U HS PARKING S LVL 5.DWG

NELSON FIRE SYSTEMS
LEVEL 5
NUMBERS

PAGE:

FA-5-02

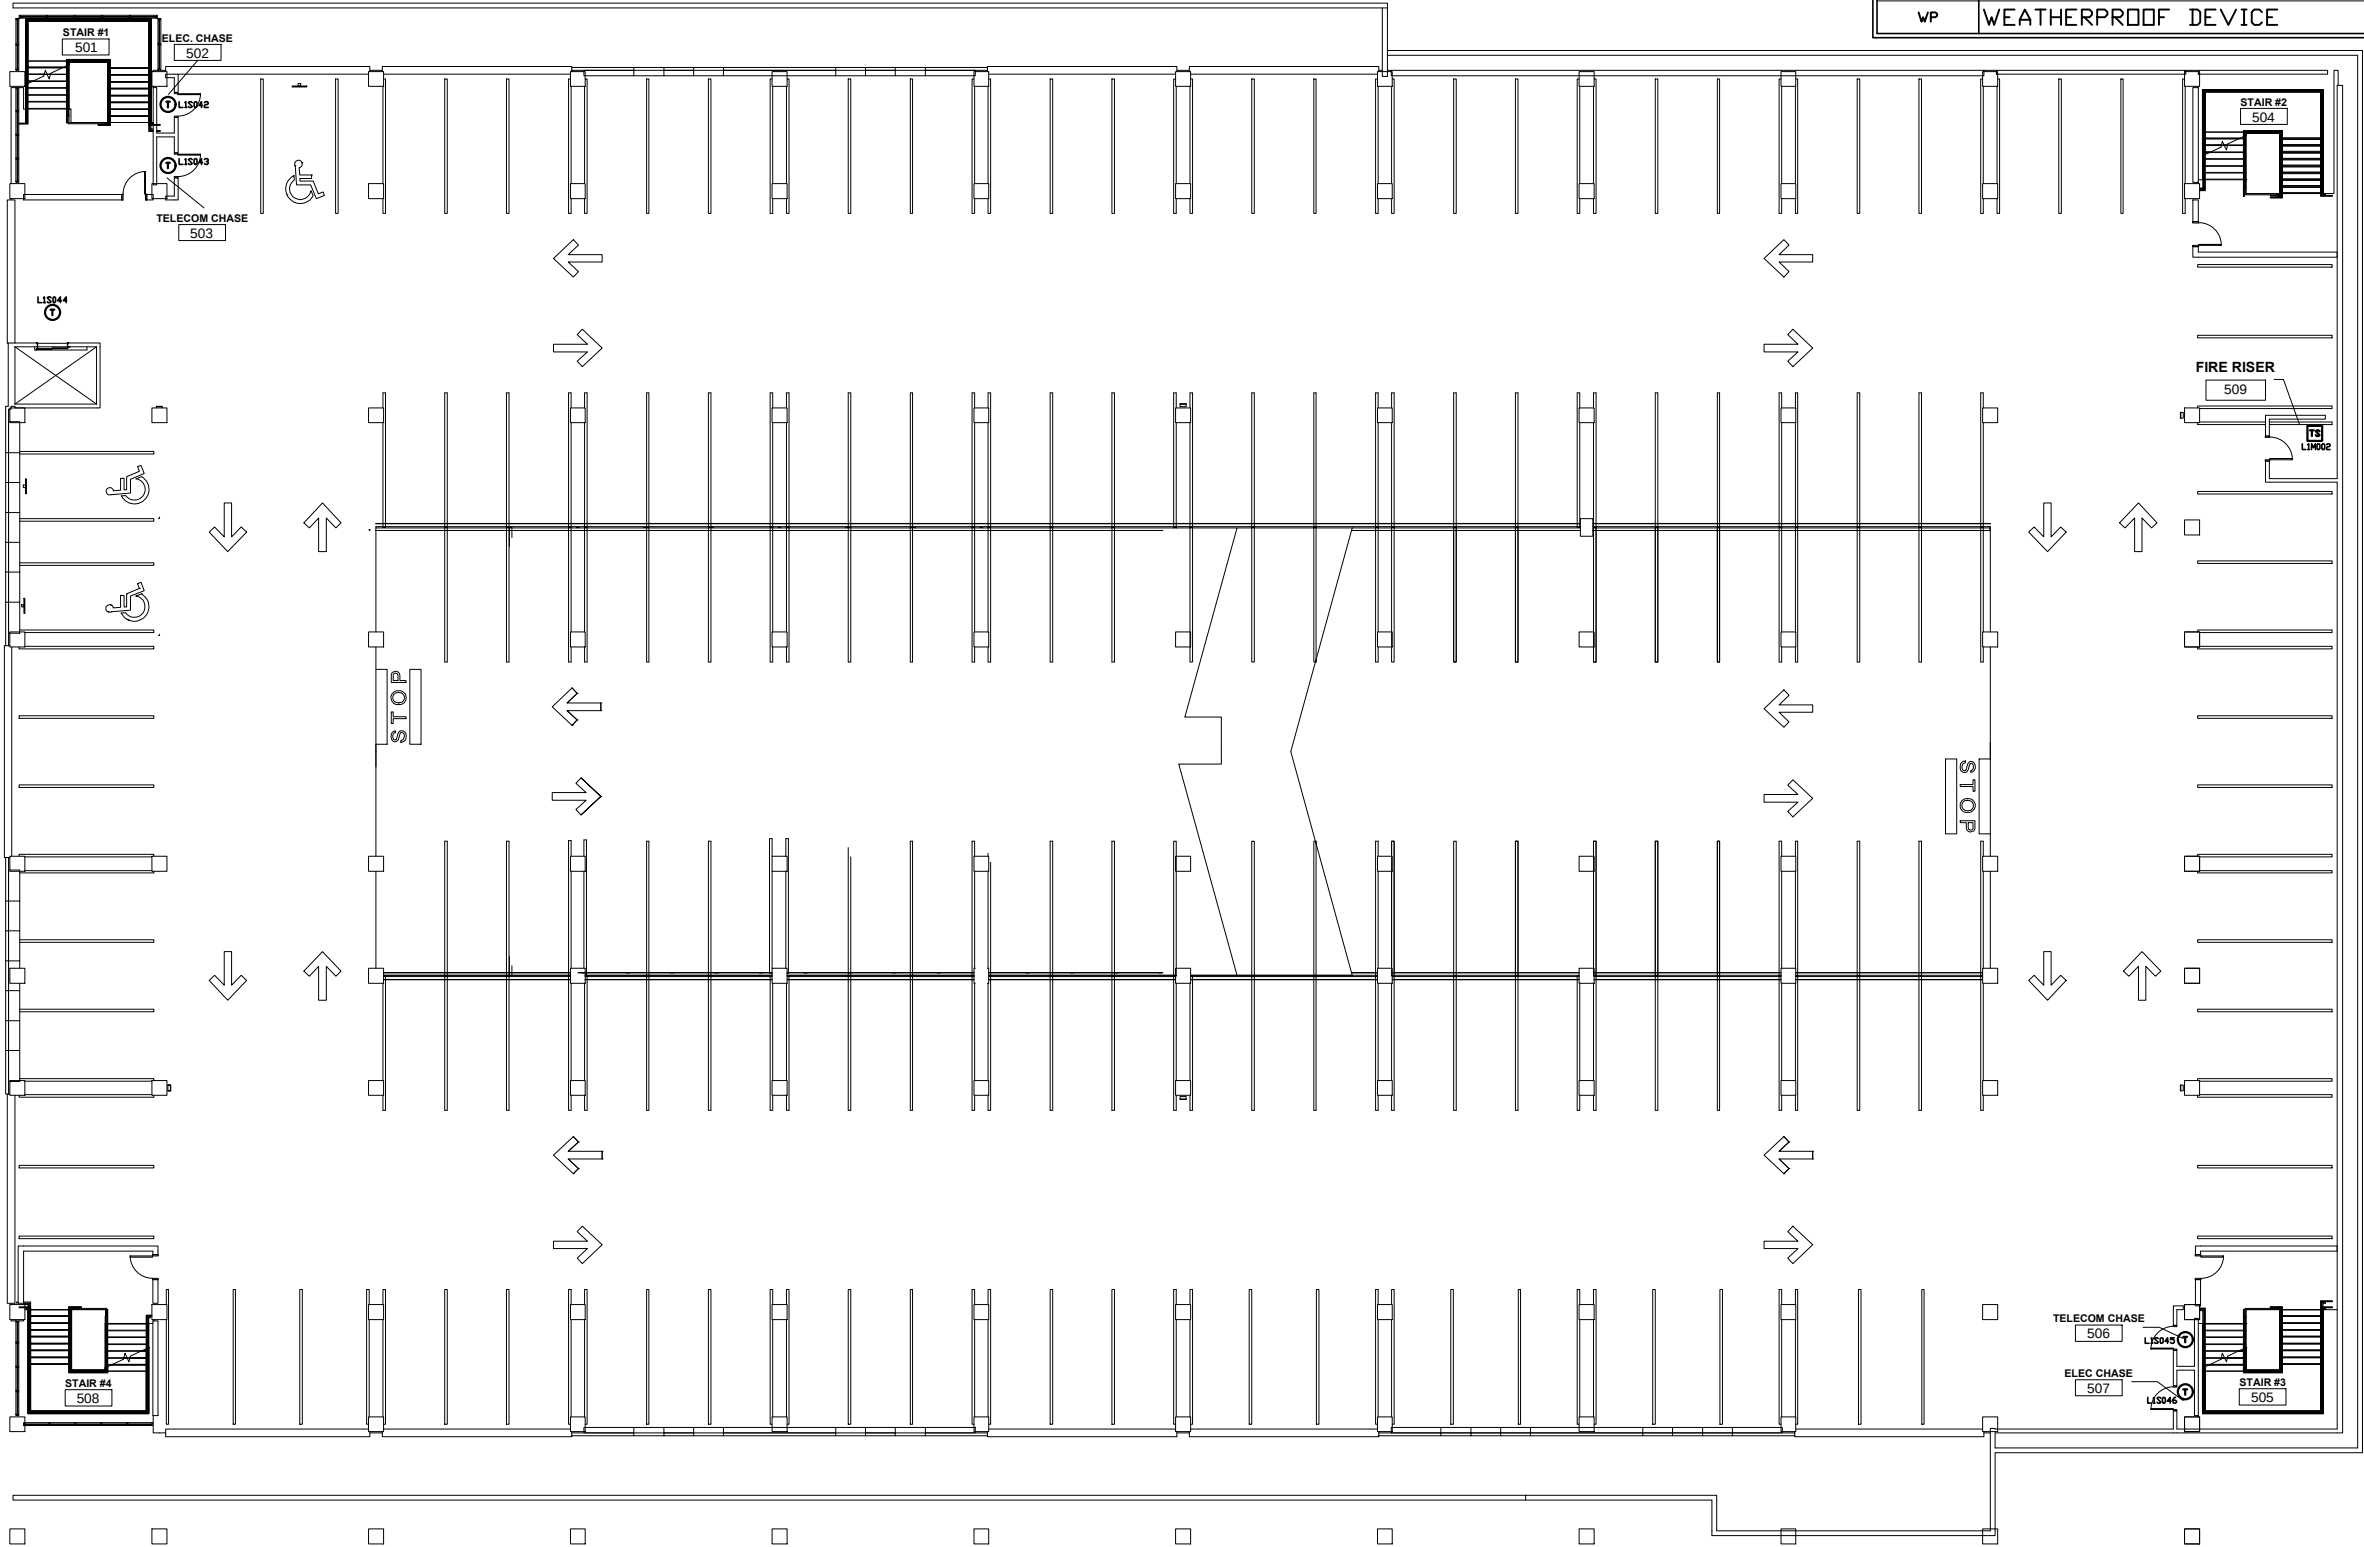

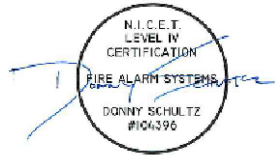

DEVICE LEGEND	
SYMBOL	DESCRIPTION
(S)	SMOKE DETECTOR
(T)	HEAT DETECTOR
TS	TAMPER SWITCH
FACU	FIRE ALARM CONTROL UNIT
TRAN	TRANSPONDER PANEL
WP	WEATHERPROOF DEVICE

NOTE:
NFS DRAWINGS ARE BASED ON THE PROJECT
ARCHITECTURE/ENGINEER (A/E) PLANS AND
SPECIFICATIONS FURNISHED TO NFS. A/E IS SOLELY
RESPONSIBLE (NOT NFS) FOR THE TYPE, SIZE,
LOCATION, AND SUITABILITY OF ALL FIRE ALARMS
CONTROL PANELS, AND OTHER DEVICES SHOWN ON
THE A/E PLANS. NFS DRAWINGS ARE TO SHOW ONLY
THE WIRING DIAGRAMS BETWEEN FIRE ALARM
DEVICES AND CONTROL PANELS. NFS IS NOT
RESPONSIBLE FOR THE INFORMATION SHOWN ON THE
A/E PLANS.

UNIVERSITY OF UTAH
HEALTH SCIENCE PARKING STRUCTURE
LEVEL 6
SALT LAKE CITY, UTAH 84112
FIRE ALARM SYSTEM

NFS
NELSON FIRE SYSTEMS
801-468-8300

DRAWN BY:	BDT
DESIGNED BY:	XXXX
APPROVED BY:	DS
DATE:	3/20/2017
SCALE:	(ARCH D) 1/16" = 1'
PROJECT NO:	XXXX
REVISION NO:	XXXX
DRAWING NAME:	U OF U HS PARKING S LVL 6.DWG

NELSON FIRE SYSTEMS
LEVEL 6
NUMBERS

