



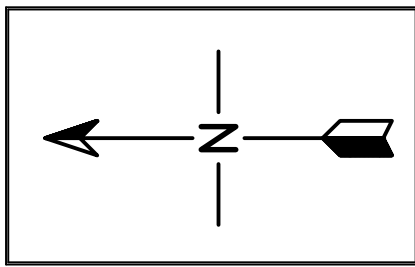

UNIVERSITY OF UTAH
SKAGGS PHARMACY RESEARCH BUILDING
FIRE ALARM SYSTEM
2/18/2013

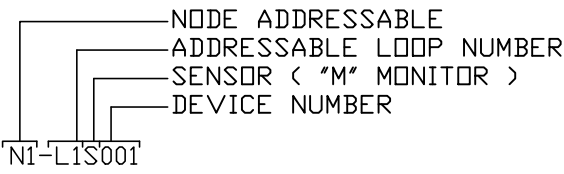


ADDRESS LABEL CLARIFICATION






DEVICE LEGEND

SYMBOL	DESCRIPTION
Ⓢ	SMOKE DETECTOR
Ⓣ	THERMAL DETECTOR
F	MANUAL PULL STATION
DD	DUCT SMOKE DETECTOR
WF	WATERFLOW SWITCH
TS	TAMPER SWITCH
MM	MONITOR MODULE
CM	CONTROL MODULE
FE	MIJA W/ MONITOR MODULE
RA	REMOTE ANNUNCIATOR
FACP	FIRE ALARM CONTROL PANEL
TRAN	TRANSPONDER PANEL
SCP	SMOKE CONTROL PANEL
VSD	VESDA AIR SAMPLING DETECTOR
VPS	VESDA POWER SUPPLY
FSD	FIRE SMOKE DAMPER
FD	FIRE DAMPER

- THESE DEVICES ARE LOCATED IN TELECOMM ROOM B0421
- N2-LIM074 SILENTONE TRIP
 - N2-LIM084 FIRE SMOKE DAMPER
 - N2-LIM085 FIRE SMOKE DAMPER
 - N2-LIM086 FIRE SMOKE DAMPER
 - N2-LIM087 FIRE SMOKE DAMPER
 - N2-LIM088 FIRE SMOKE DAMPER
 - N2-LIM089 FIRE SMOKE DAMPER
 - N2-LIM091 FIRE SMOKE DAMPER
 - N2-LIM092 FIRE SMOKE DAMPER

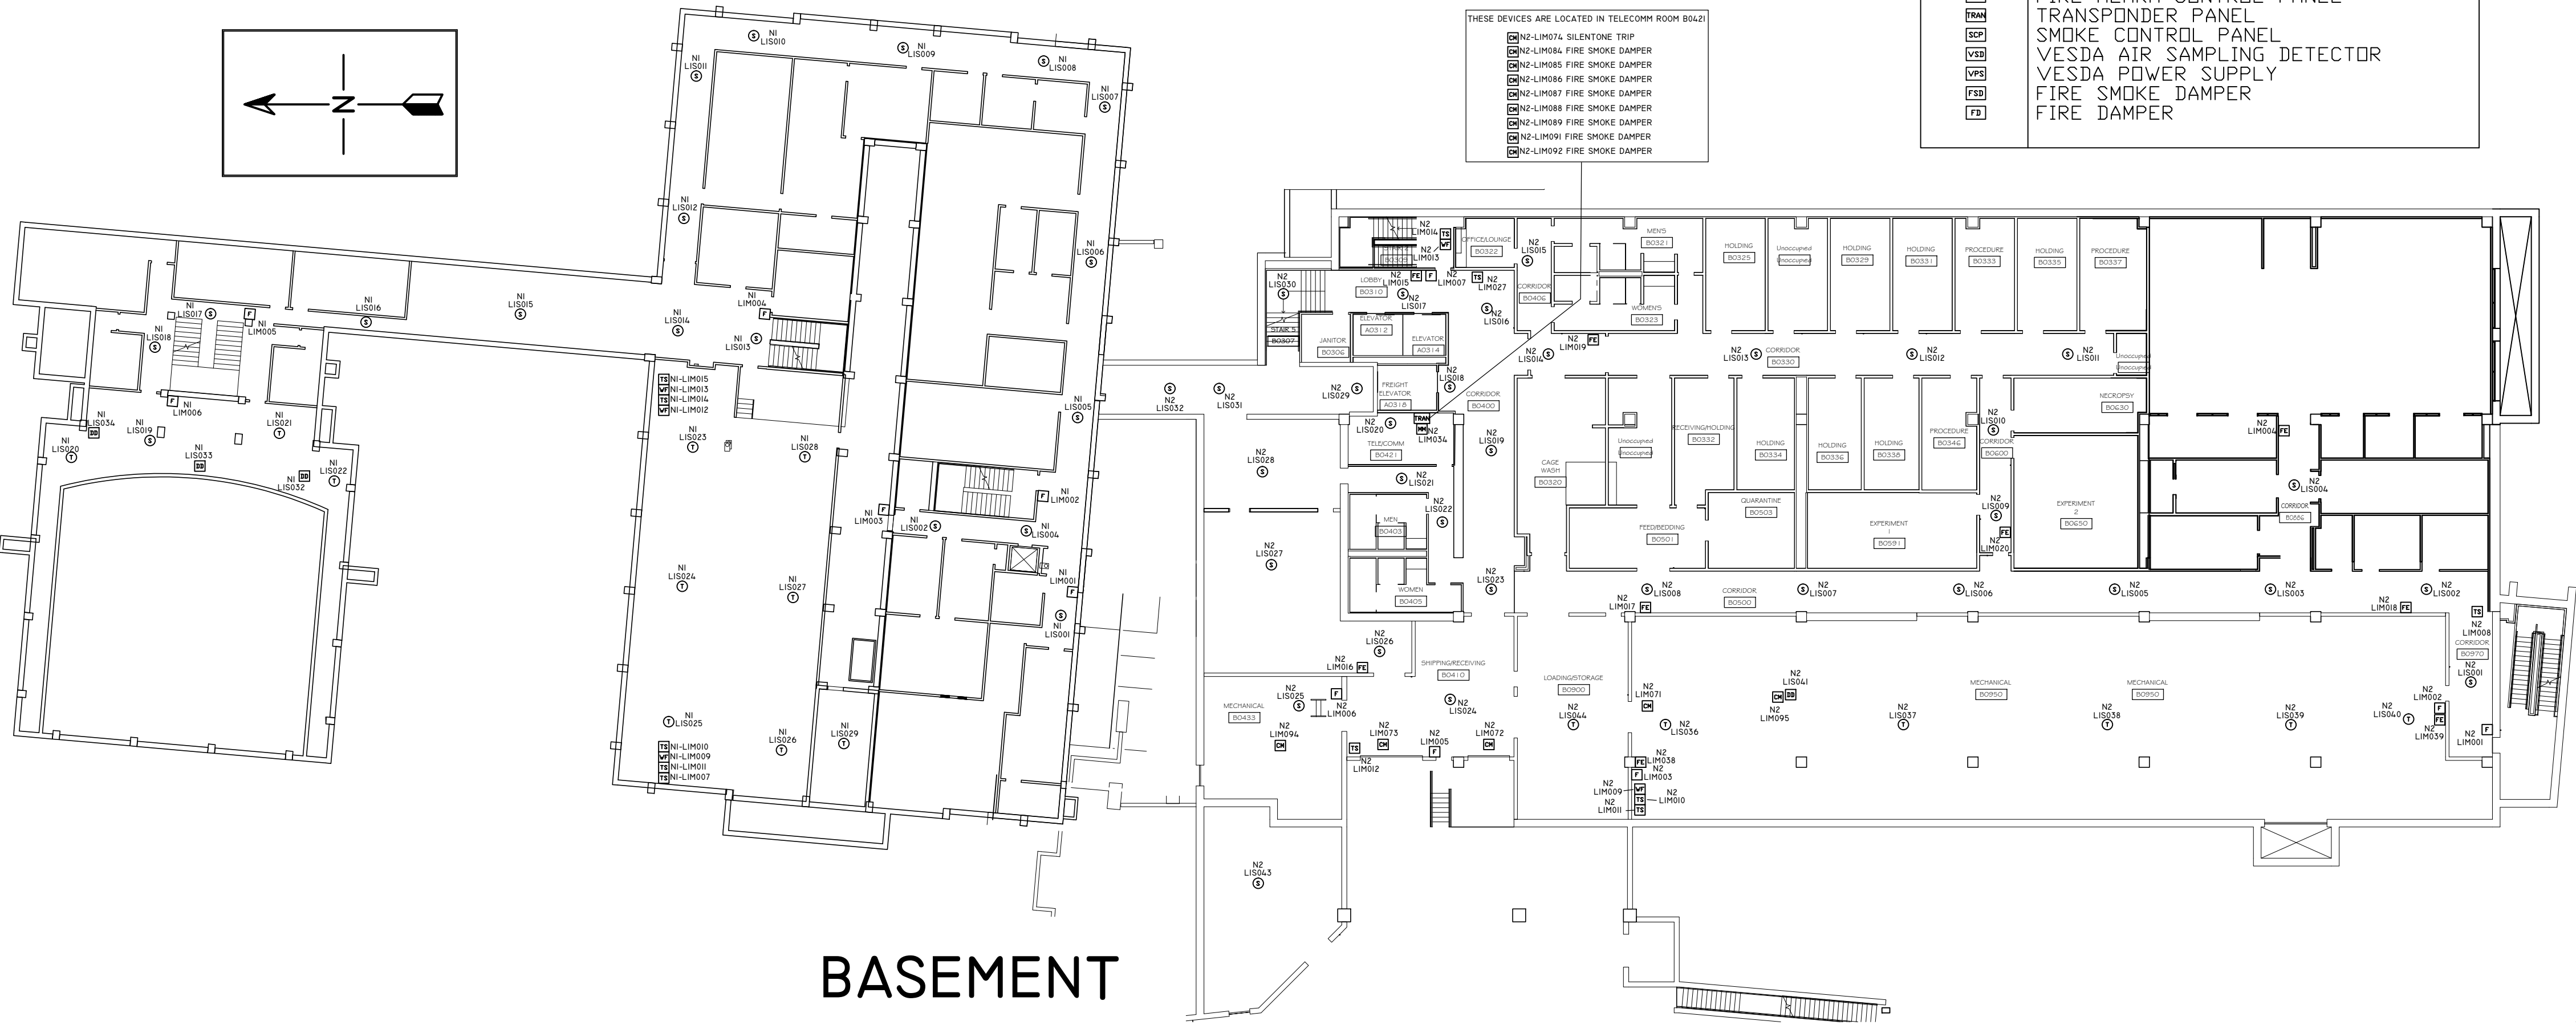

BASEMENT

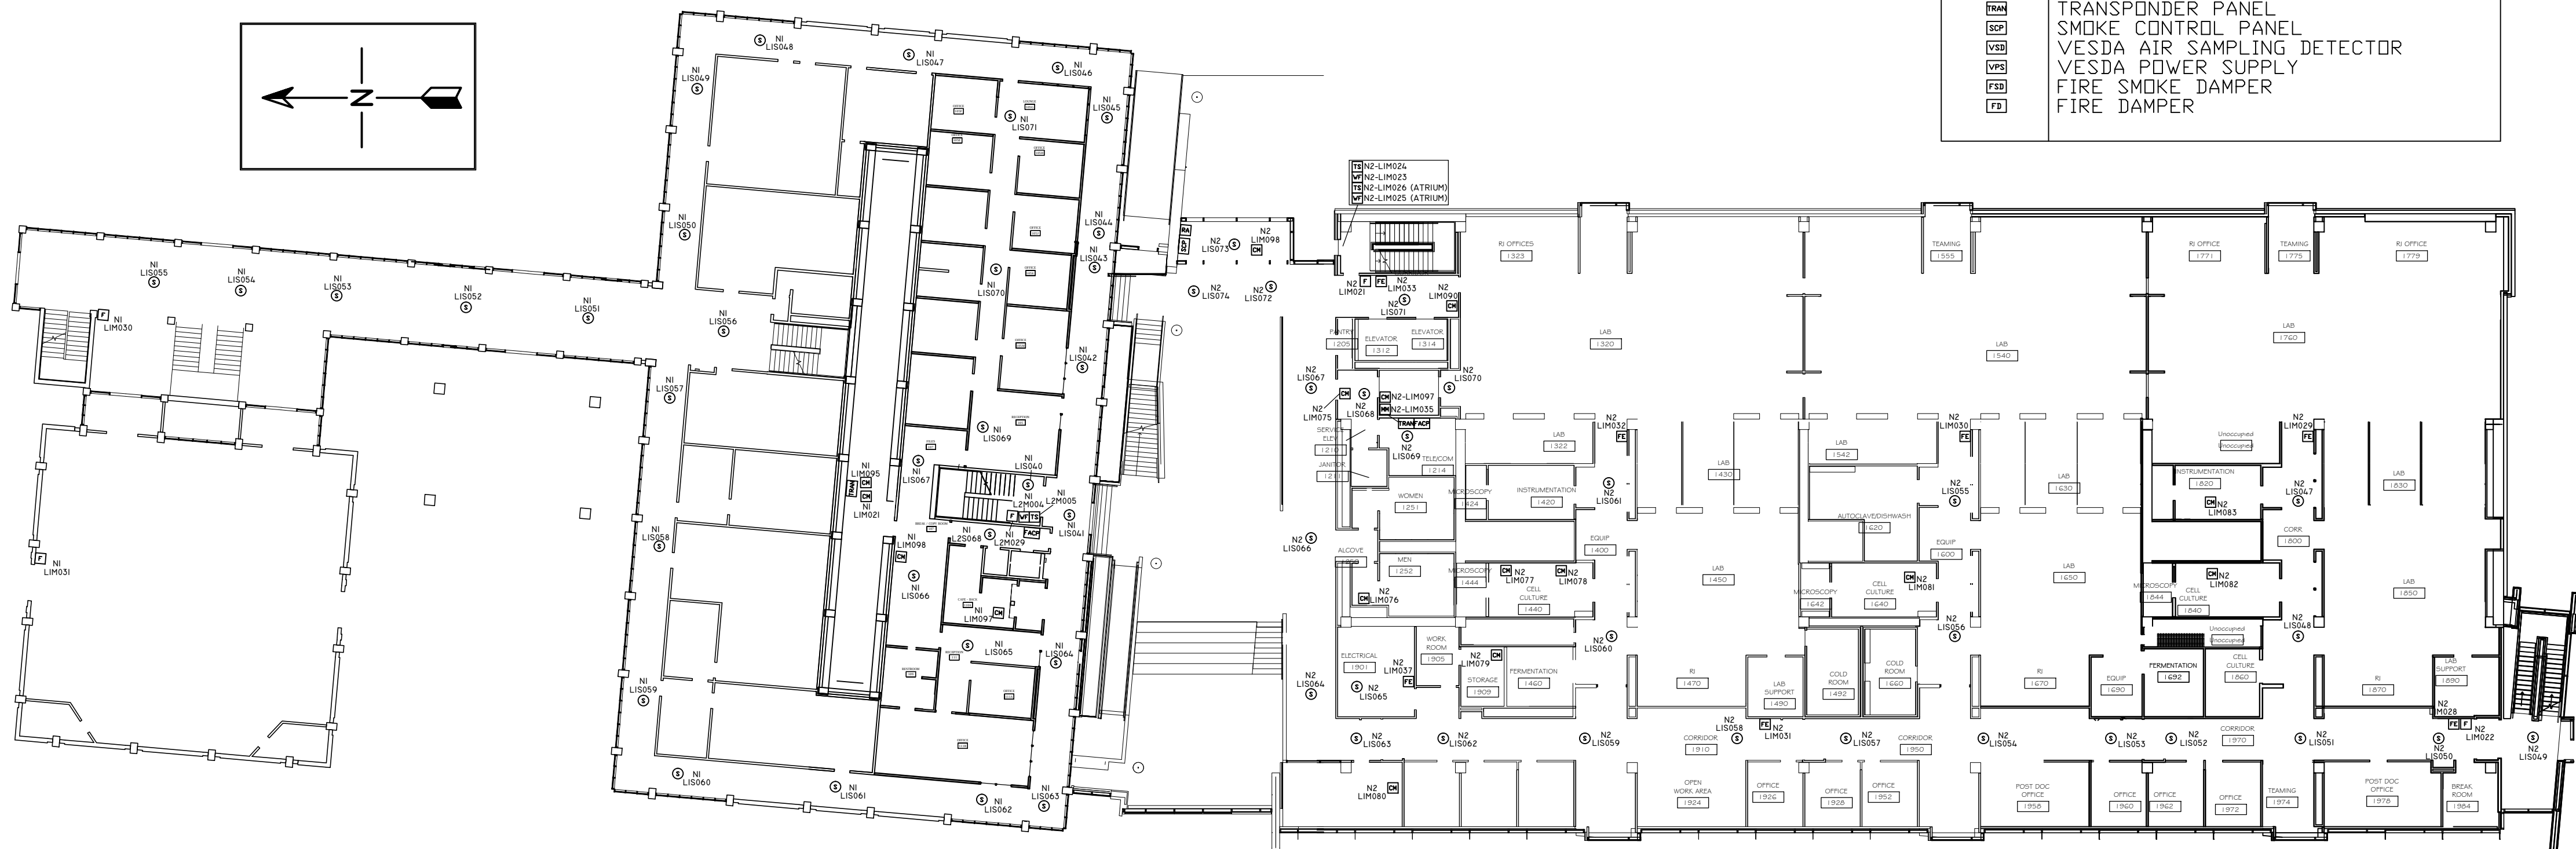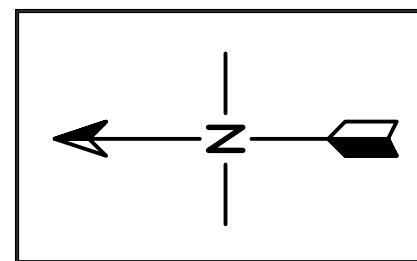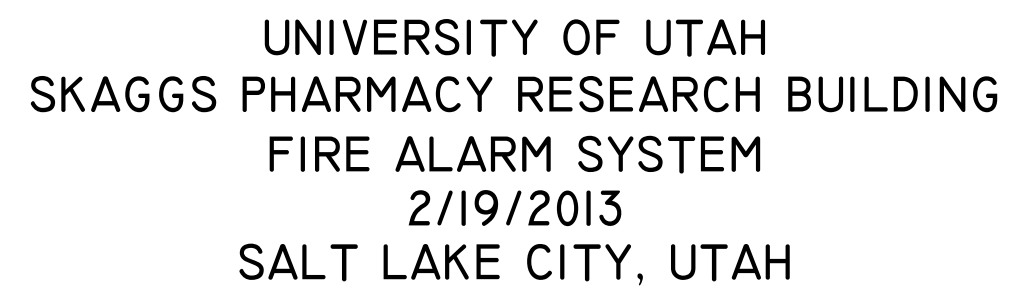


FIRST FLOOR

DEVICE LEGEND


SYMBOL	DESCRIPTION
③	SMOKE DETECTOR
①	THERMAL DETECTOR
F	MANUAL PULL STATION
DD	DUCT SMOKE DETECTOR
WT	WATERFLOW SWITCH
TS	TAMPER SWITCH
MM	MONITOR MODULE
CM	CONTROL MODULE
FE	ENGAGE W/ MONITOR MODULE
RA	REMOTE ANNUNCIATOR
FACP	FIRE ALARM CONTROL PANEL
TRAN	TRANSPONDER PANEL
SCP	SMOKE CONTROL PANEL
VSD	VESDA AIR SAMPLING DETECTOR
VPS	VESDA POWER SUPPLY
FSD	FIRE SMOKE DAMPER
FD	FIRE DAMPER



UNIVERSITY OF UTAH
SKAGGS PHARMACY RESEARCH BUILDING
FIRE ALARM SYSTEM
2/18/2013
SALT LAKE CITY, UTAH

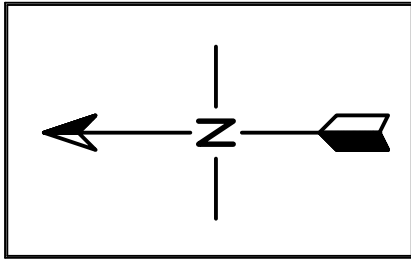


ADDRESS LABEL CLARIFICATION

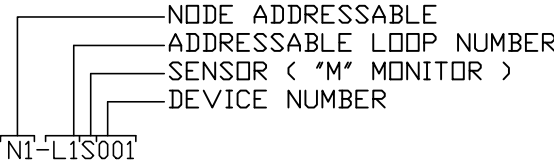

- THESE DEVICES ARE LOCATED IN TELECOMM ROOM 2214
- N2-L2M084 FIRE SMOKE DAMPER
 - N2-L2M085 FIRE SMOKE DAMPER
 - N2-L2M086 FIRE SMOKE DAMPER
 - N2-L2M087 FIRE SMOKE DAMPER
 - N2-L2M088 FIRE SMOKE DAMPER
 - N2-L2M089 FIRE SMOKE DAMPER
 - N2-L2M090 FIRE SMOKE DAMPER
 - N2-L2M091 FIRE SMOKE DAMPER
 - N2-L2M092 FIRE SMOKE DAMPER


DEVICE LEGEND	
SYMBOL	DESCRIPTION
Ⓢ	SMOKE DETECTOR
Ⓣ	THERMAL DETECTOR
Ⓜ	MANUAL PULL STATION
ⓈⓈ	DUCT SMOKE DETECTOR
ⓌⓈ	WATERFLOW SWITCH
ⓉⓈ	TAMPER SWITCH
ⓂⓂ	MONITOR MODULE
ⓈⓂ	CONTROL MODULE
ⓂⓂⓂ	MIJA W/ MONITOR MODULE
ⓂⓂⓂ	REMOTE ANNUNCIATOR
ⓂⓂⓂ	FIRE ALARM CONTROL PANEL
ⓂⓂⓂ	TRANSPONDER PANEL
ⓂⓂⓂ	SMOKE CONTROL PANEL
ⓂⓂⓂ	VESDA AIR SAMPLING DETECTOR
ⓂⓂⓂ	VESDA POWER SUPPLY
ⓂⓂⓂ	FIRE SMOKE DAMPER
ⓂⓂⓂ	FIRE DAMPER

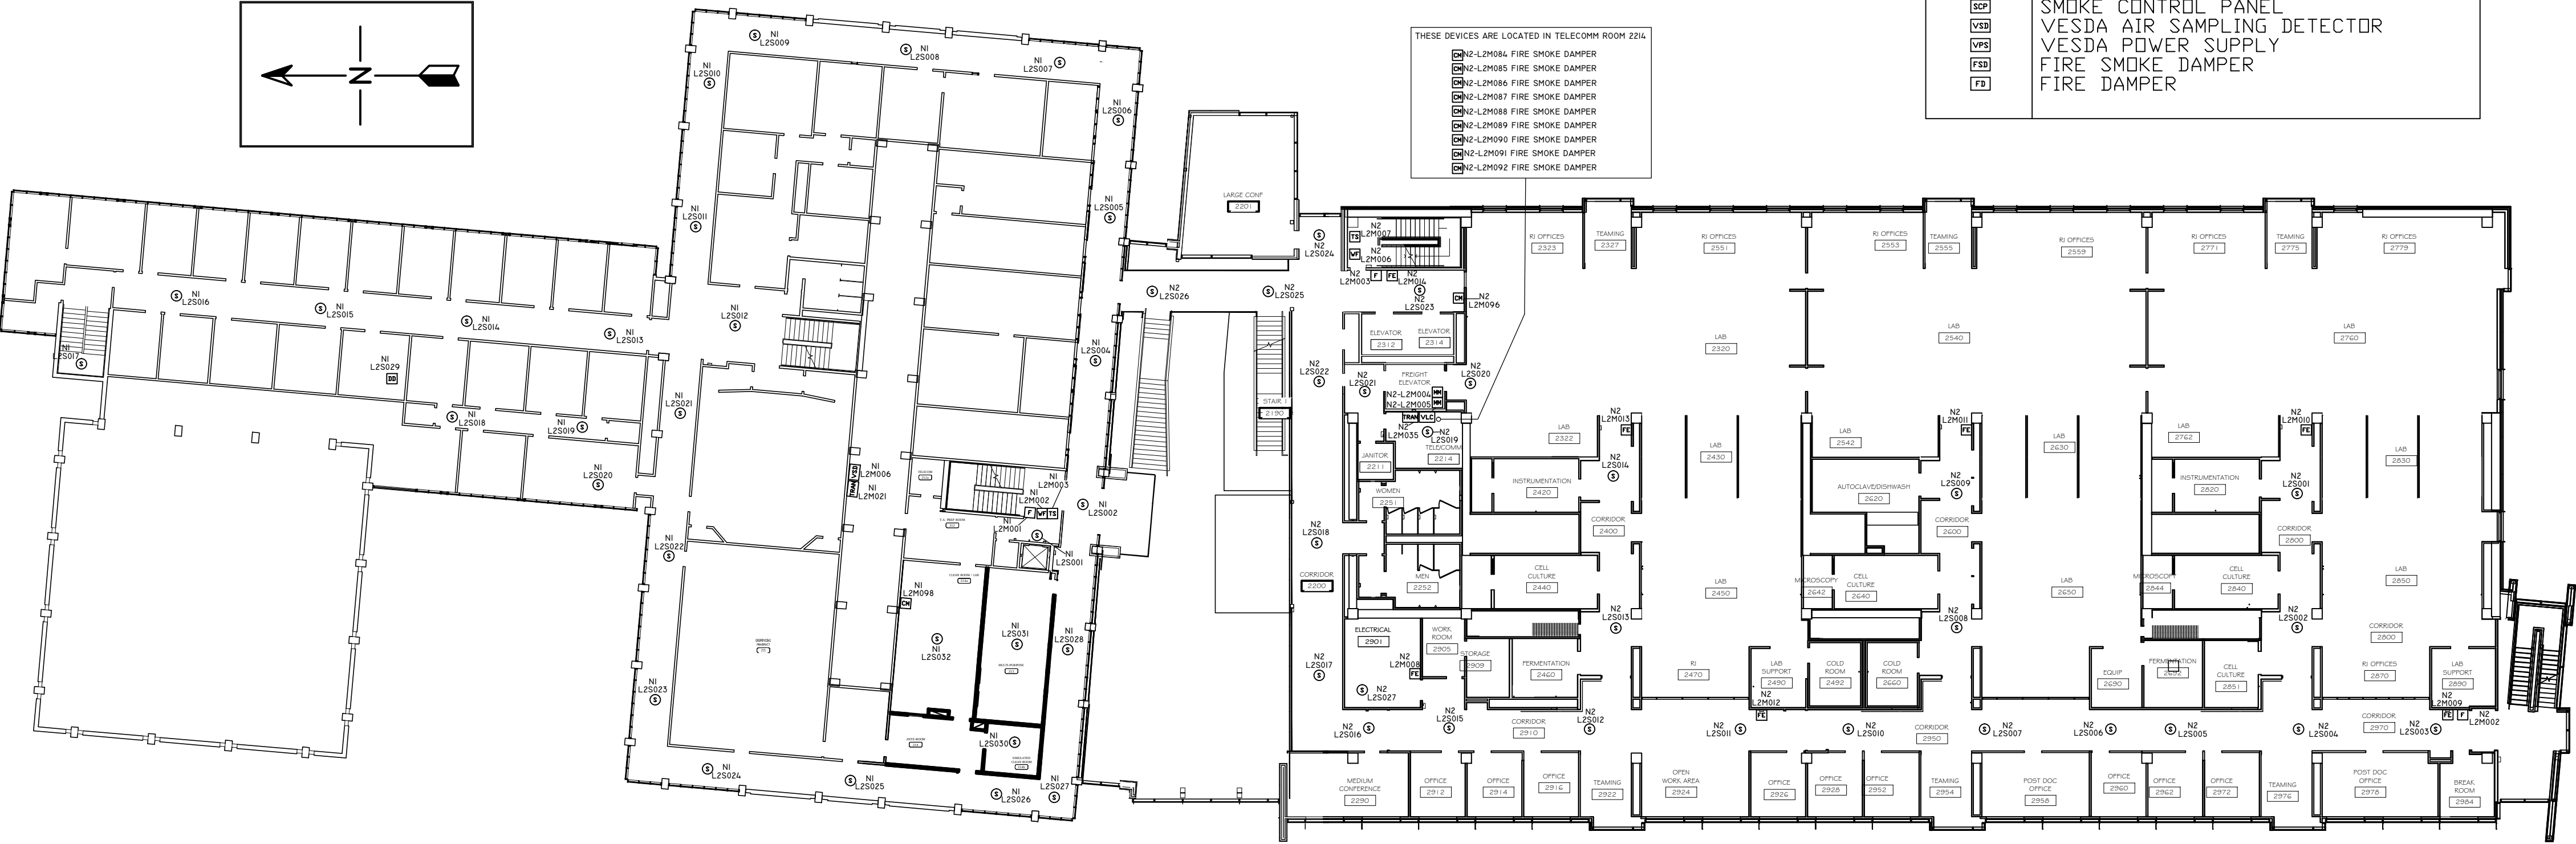


SECOND FLOOR



UNIVERSITY OF UTAH
SKAGGS PHARMACY RESEARCH BUILDING
FIRE ALARM SYSTEM
2/18/2013
SALT LAKE CITY, UTAH

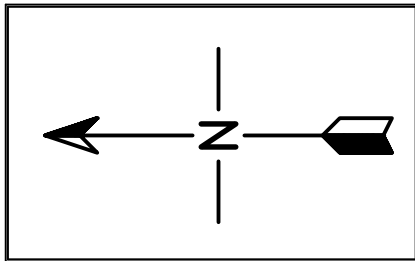


ADDRESS LABEL CLARIFICATION

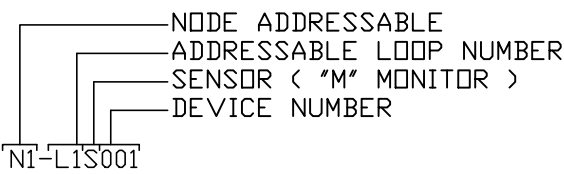

DEVICE LEGEND



SYMBOL	DESCRIPTION
Ⓢ	SMOKE DETECTOR
Ⓣ	THERMAL DETECTOR
F	MANUAL PULL STATION
DD	DUCT SMOKE DETECTOR
WF	WATERFLOW SWITCH
TS	TAMPER SWITCH
MM	MONITOR MODULE
CM	CONTROL MODULE
FE	MIJA W/ MONITOR MODULE
RA	REMOTE ANNUNCIATOR
FACP	FIRE ALARM CONTROL PANEL
TRAN	TRANSPONDER PANEL
SCP	SMOKE CONTROL PANEL
VSD	VESDA AIR SAMPLING DETECTOR
VPS	VESDA POWER SUPPLY
FSD	FIRE SMOKE DAMPER
FD	FIRE DAMPER

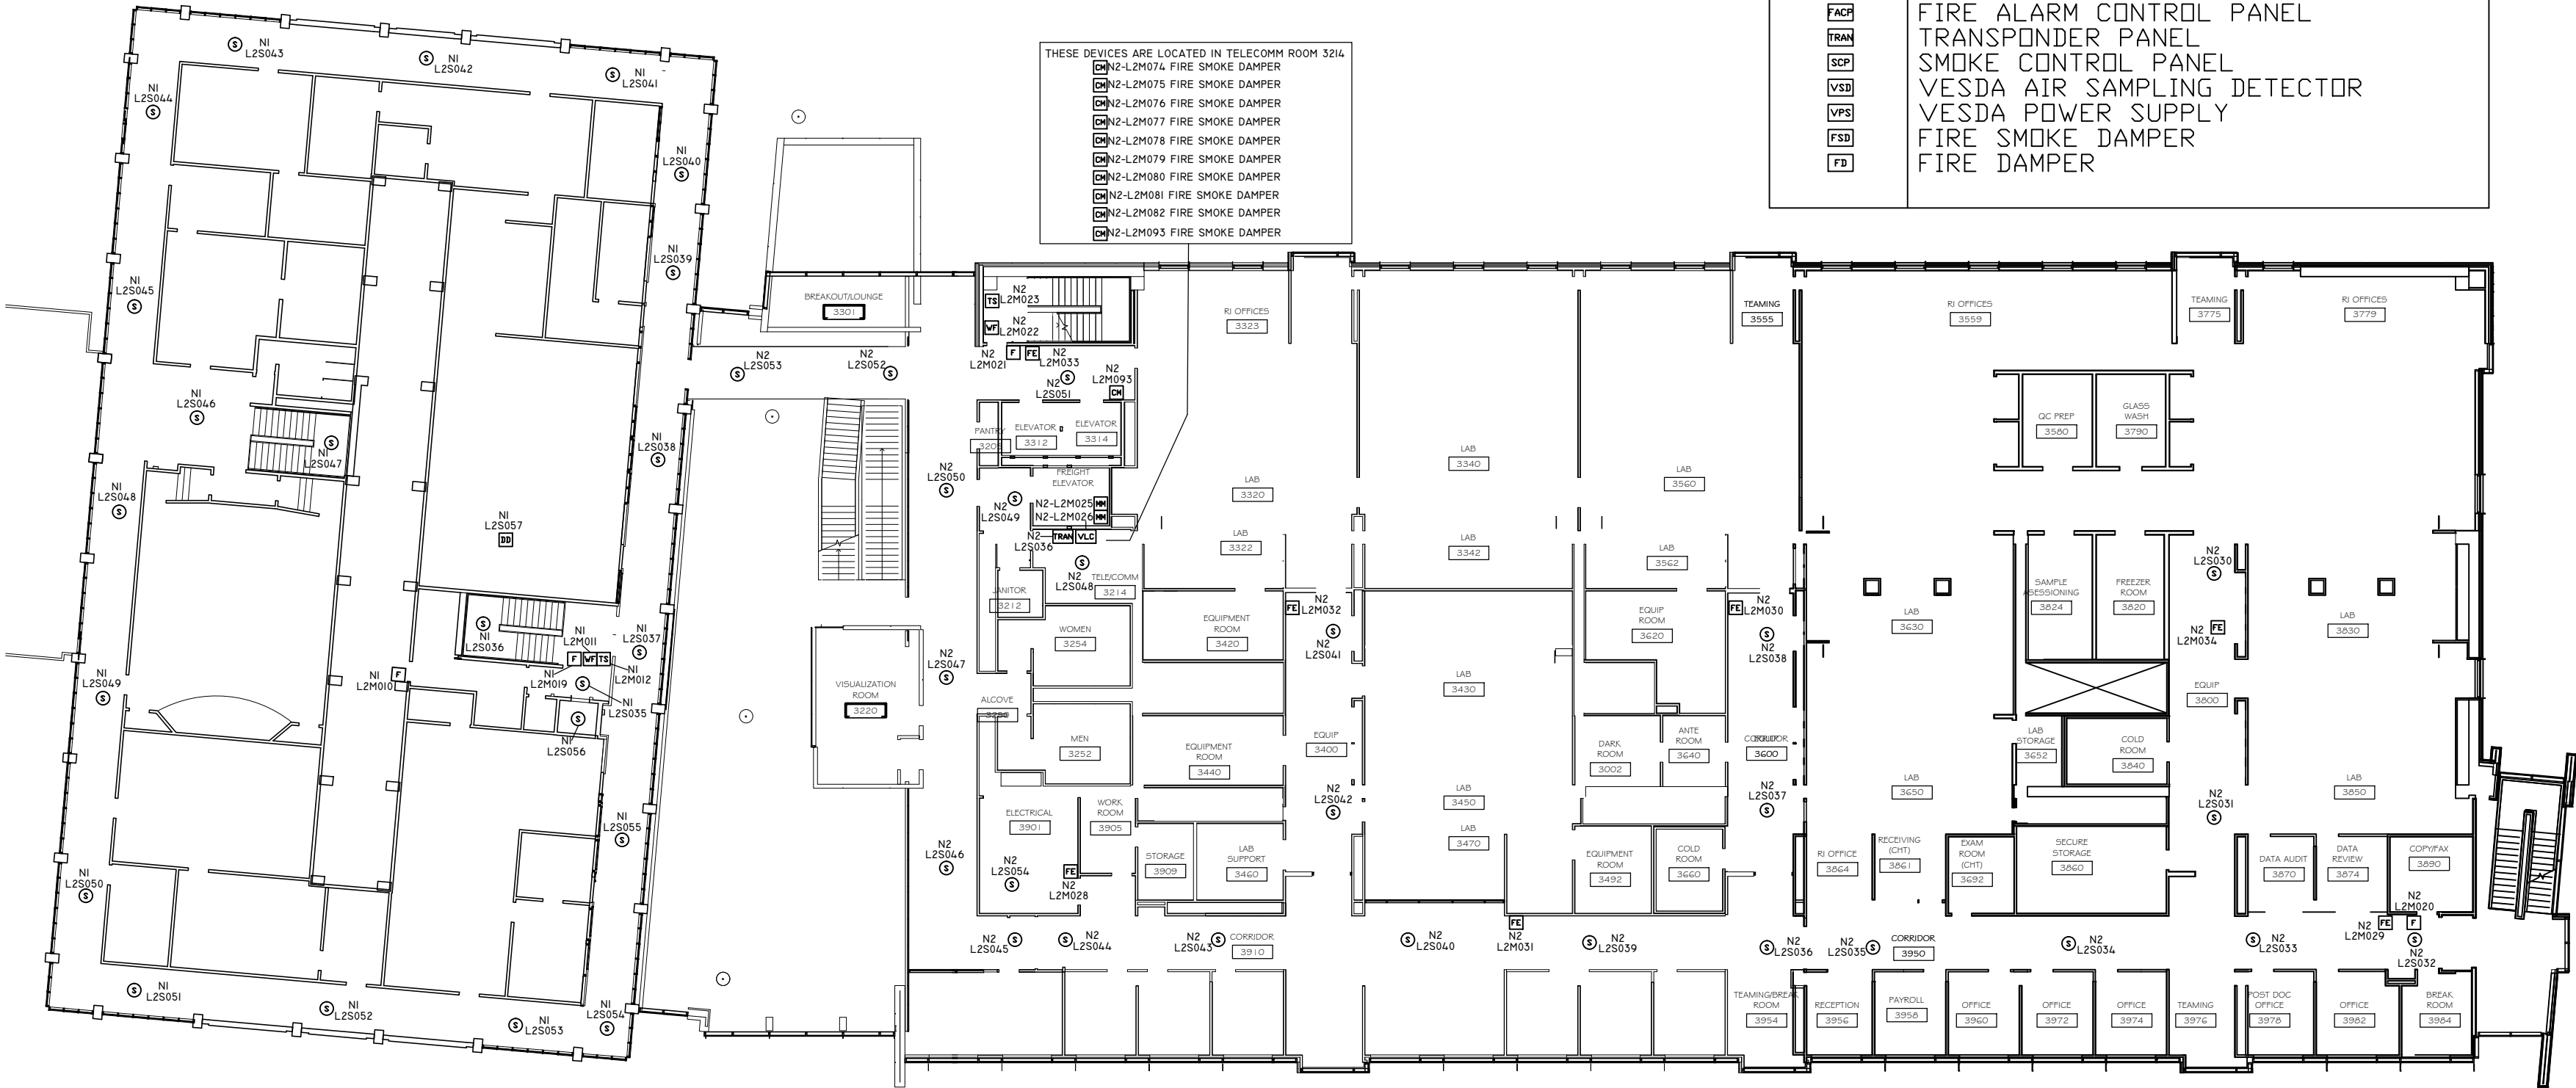


THIRD FLOOR





UNIVERSITY OF UTAH
SKAGGS PHARMACY RESEARCH BUILDING
FIRE ALARM SYSTEM
2/18/2013
SALT LAKE CITY, UTAH

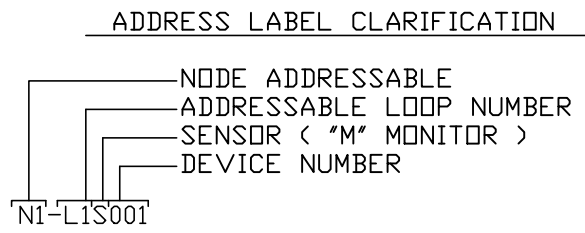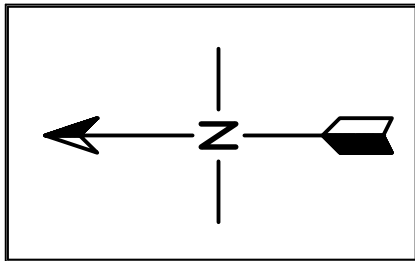


DEVICE LEGEND	
SYMBOL	DESCRIPTION
Ⓢ	SMOKE DETECTOR
Ⓣ	THERMAL DETECTOR
F	MANUAL PULL STATION
DD	DUCT SMOKE DETECTOR
WF	WATERFLOW SWITCH
TS	TAMPER SWITCH
MM	MONITOR MODULE
CM	CONTROL MODULE
FE	MIJA W/ MONITOR MODULE
RA	REMOTE ANNUNCIATOR
FACP	FIRE ALARM CONTROL PANEL
TRAN	TRANSPONDER PANEL
SCP	SMOKE CONTROL PANEL
VSD	VESDA AIR SAMPLING DETECTOR
VPS	VESDA POWER SUPPLY
FSD	FIRE SMOKE DAMPER
FD	FIRE DAMPER

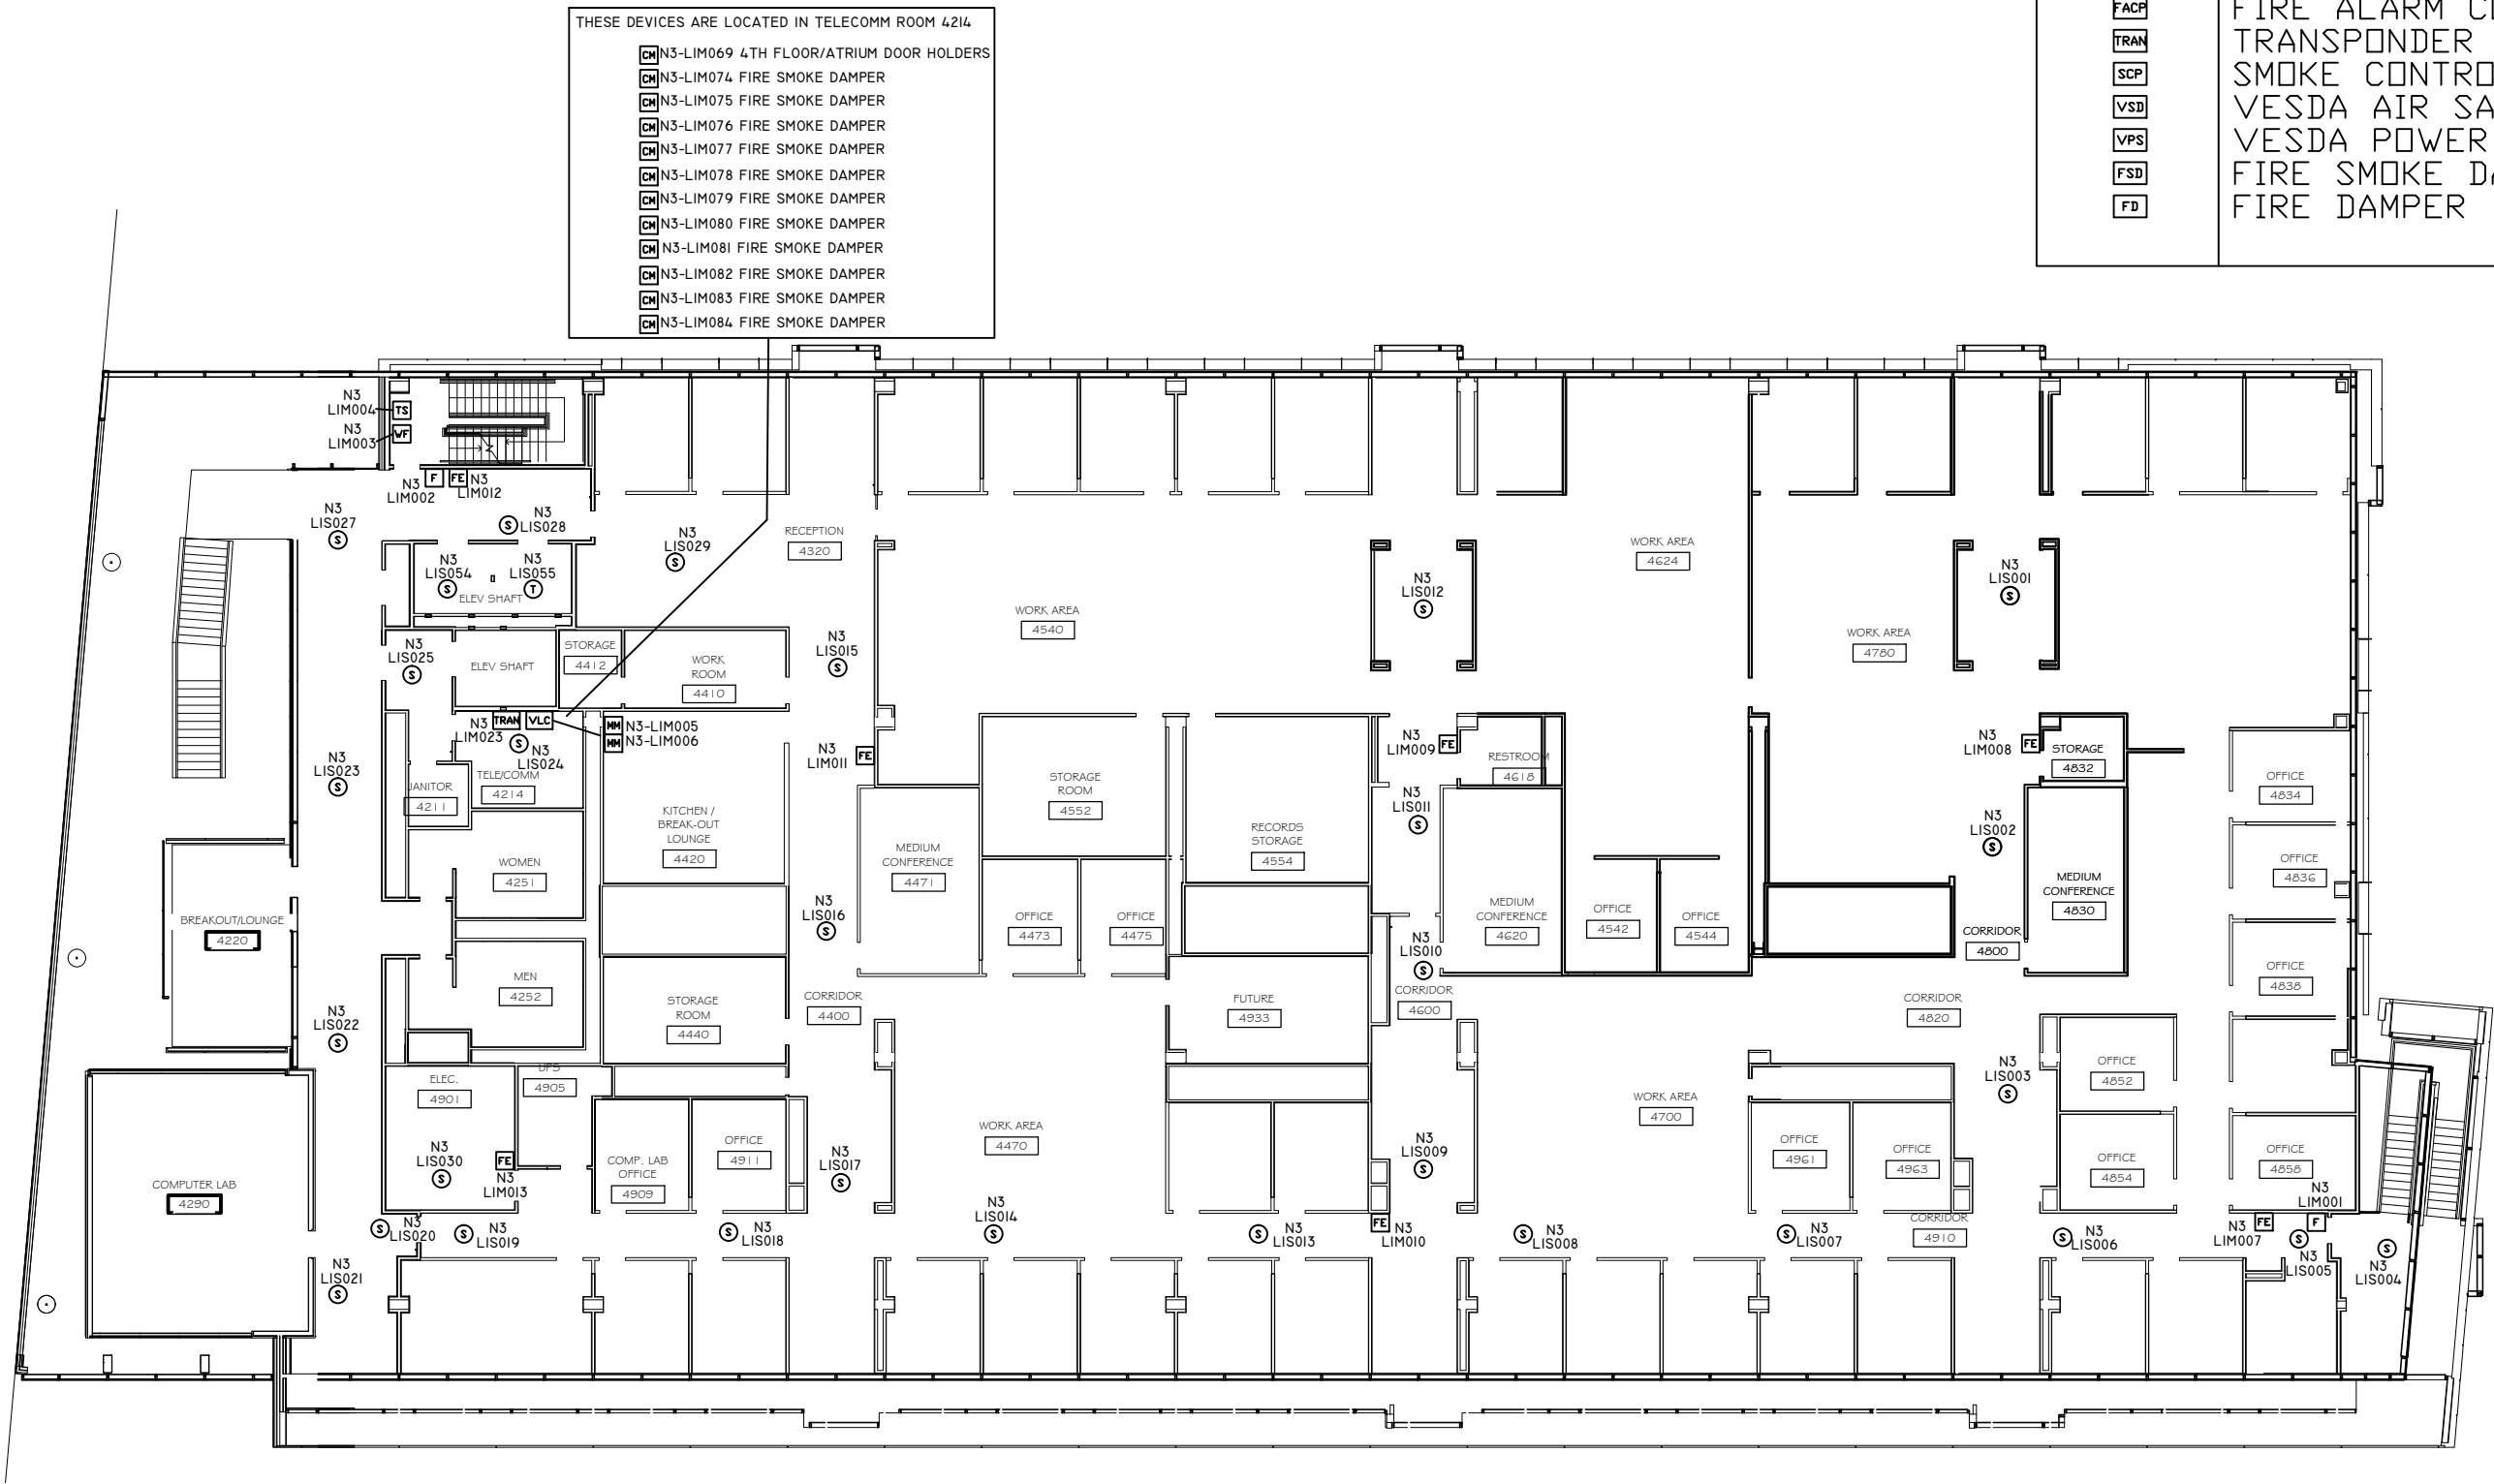

FOURTH FLOOR

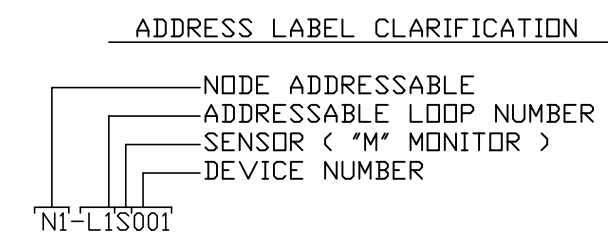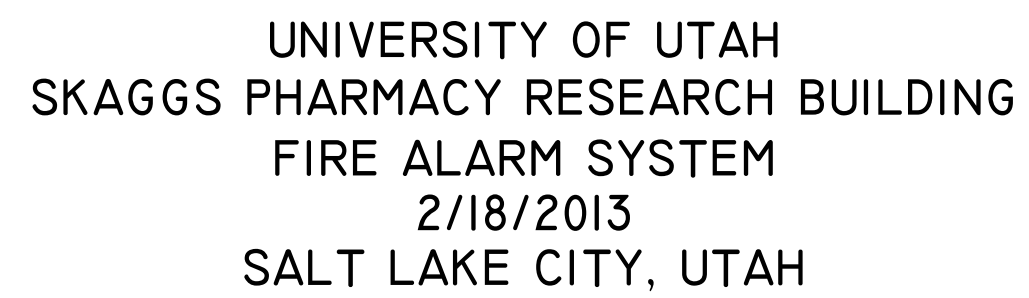

DEVICE LEGEND	
SYMBOL	DESCRIPTION
③	SMOKE DETECTOR
①	THERMAL DETECTOR
F	MANUAL PULL STATION
DD	DUCT SMOKE DETECTOR
WF	WATERFLOW SWITCH
TS	TAMPER SWITCH
MM	MONITOR MODULE
CM	CONTROL MODULE
FE	MIJA W/ MONITOR MODULE
RA	REMOTE ANNUNCIATOR
FACP	FIRE ALARM CONTROL PANEL
TRAN	TRANSPONDER PANEL
SCP	SMOKE CONTROL PANEL
VSD	VESDA AIR SAMPLING DETECTOR
VPS	VESDA POWER SUPPLY
FSD	FIRE SMOKE DAMPER
FD	FIRE DAMPER

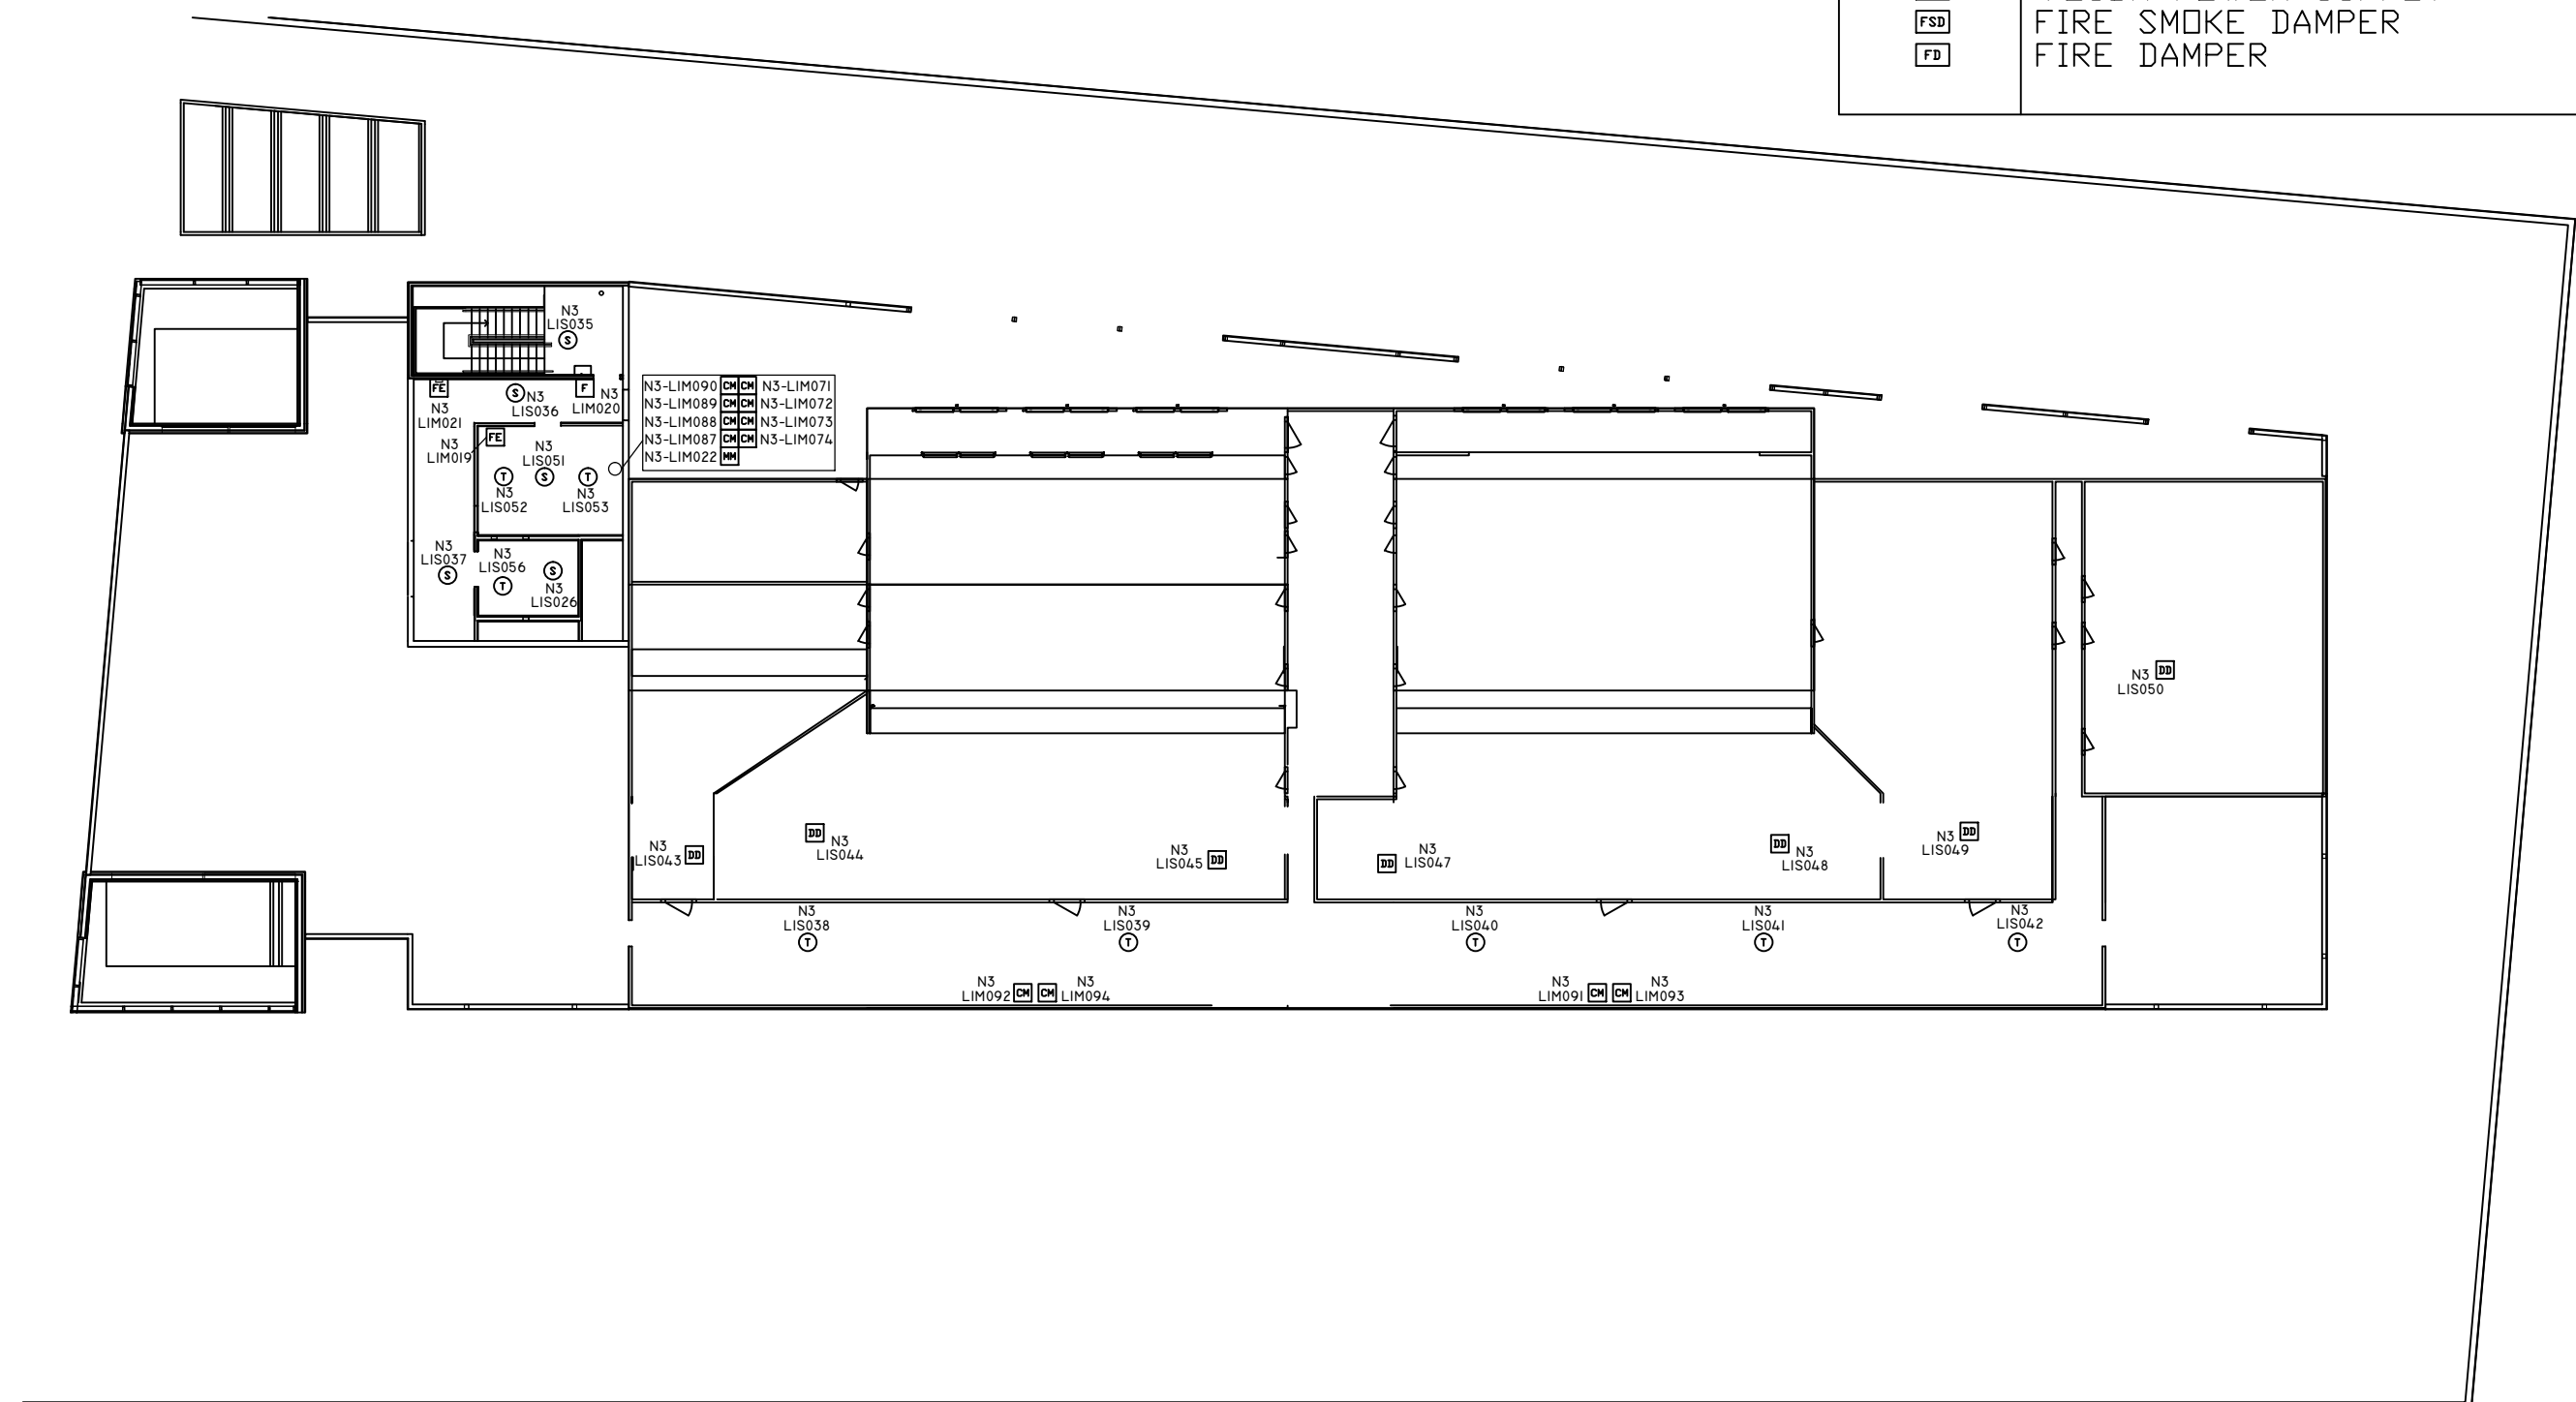

PENTHOUSE