


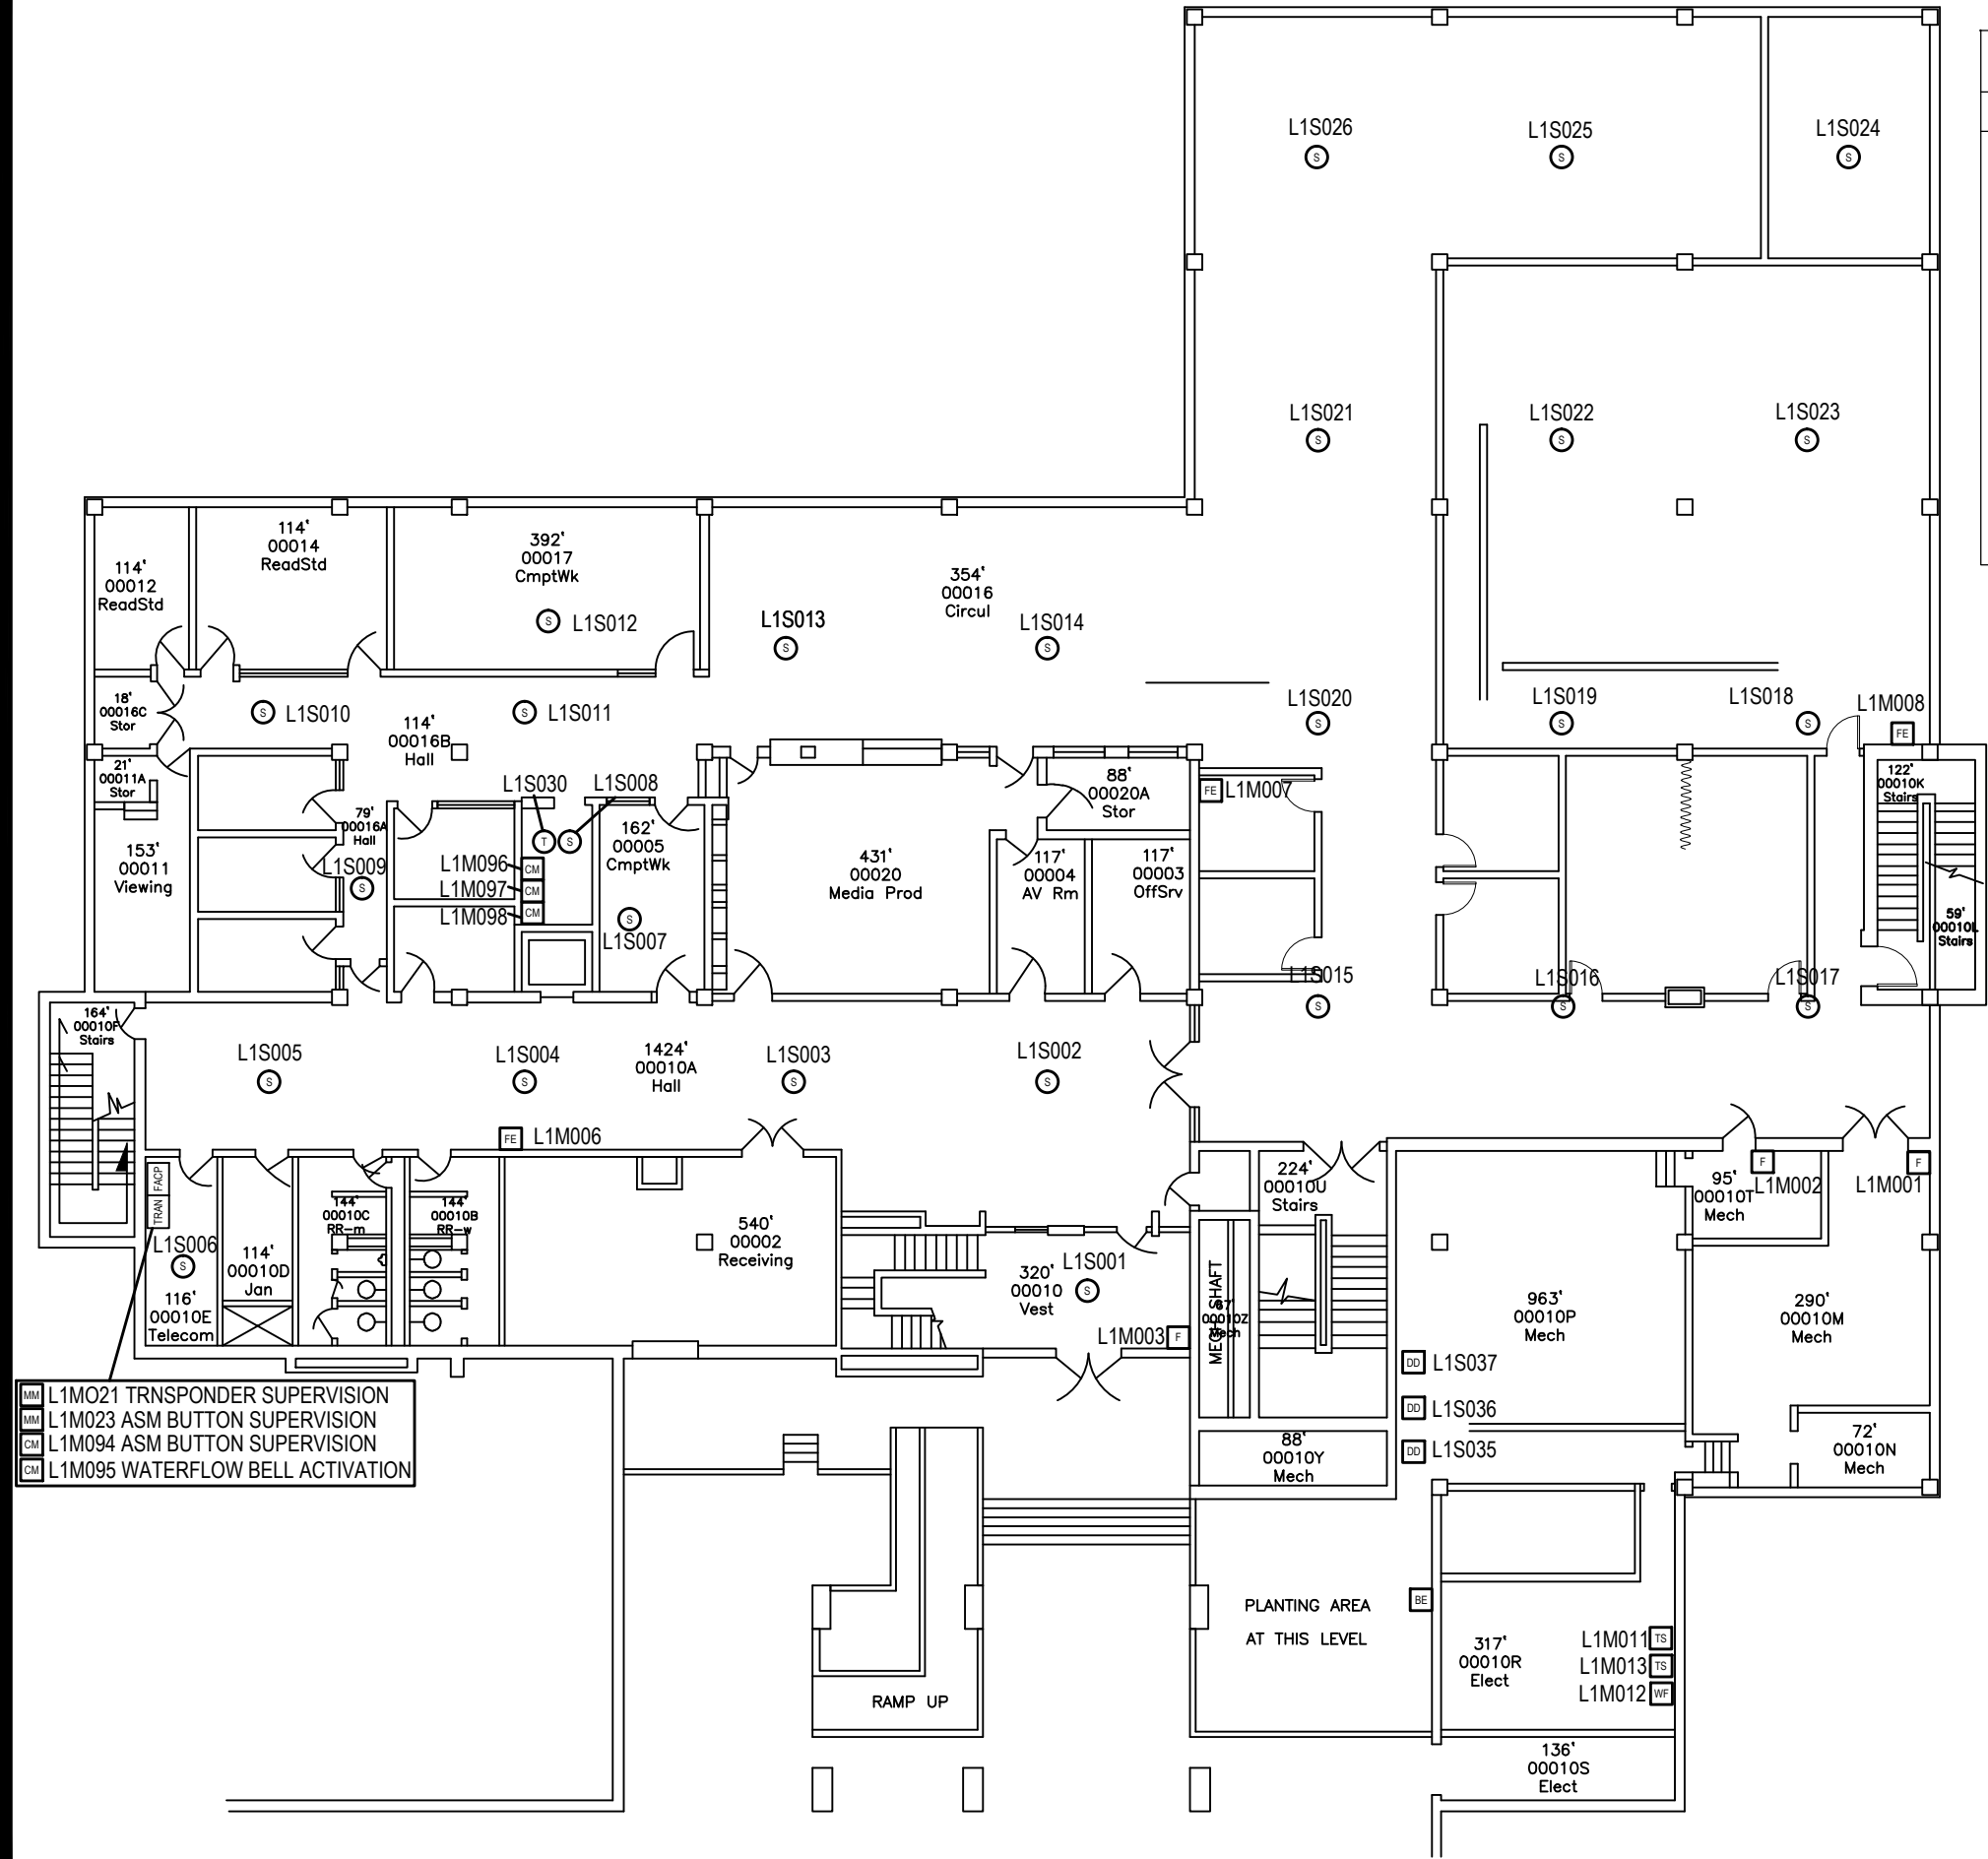


DEVICE LEGEND	
SYMBOL	DESCRIPTION
	SMOKE DETECTOR
	SMOKE DETECTOR ABOVE CEILING
	HEAT DETECTOR
	DUCT DETECTOR
	MANUAL PULL STATION
	HORN/STROBE
	STROBE
	WATERFLOW SWITCH
	TAMPER SWITCH
	MONITOR MODULE
	CONTROL MODULE
	WATERFLOW BELL
	FIRE EXTINGUISHER W/ EN-GAUGE
	REMOTE ANNUNCIATOR
	FIRE ALARM CONTROL PANEL
	TRANSPONDER

WIRE SCHEDULE		
SYMBOL	DESCRIPTION	SIZE
A	ADDRESSABLE CIRCUIT	1 PAIR #14 TWISTED
B	HORN/STROBE CIRCUIT	2 #14'S
C	FAN/DAMPER CONTROL RELAY CIRCUIT	2 #14'S
D	24V DC AUX POWER	2 #14'S
E	REMOTE ANNUNCIATOR	4 PAIR #16'S TWISTED
F	120 VAC POWER WITH GROUND	3 #12'S
G	BELL	24#14'S

SYSTEM NOTES:

- TO LOWER LEVEL TRANSPONDER
- TO FACP
- TO 120 VAC WITH GROUND

- L1M021 TRNSPONDER SUPERVISION
- L1M023 ASM BUTTON SUPERVISION
- L1M094 ASM BUTTON SUPERVISION
- L1M095 WATERFLOW BELL ACTIVATION

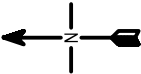

NOTE:
NFS DRAWINGS ARE BASED ON THE PROJECT
ARCHITECT/ENGINEER (A/E) PLANS AND SPECIFICATIONS
FURNISHED TO NFS. A/E IS SOLELY RESPONSIBLE
(NOT NFS) FOR THE TYPE, SIZE, LOCATION, AND
SUITABILITY OF ALL FIRE ALARMS, CONTROL PANELS,
AND OTHER DEVICES SHOWN ON THE A/E PLANS.
NFS DRAWINGS ARE TO SHOW ONLY THE WIRING
DIAGRAMS BETWEEN FIRE ALARM DEVICES AND
CONTROL PANELS. NFS IS NOT RESPONSIBLE FOR
THE INFORMATION SHOWN ON THE A/E PLANS.

ECCLES HEALTH SCIENCES LIBRARY
UNIVERSITY OF UTAH
LOWER LEVEL
FIRE ALARM SYSTEM

NFS


NELSON FIRE SYSTEMS
801-468-8300

DRAWN BY:	DS
DESIGNED BY:	XXXX
CHECKED BY:	KGE
DATE:	11/29/2010
SCALE:	N.T.S.
PROJECT NO:	XXXX
REV NO:	XXXX
DRAWING NAME:	HEALTH SCIENCES LOWER.DWG

FIRE ALARM SYSTEM

ADDRESSABLE NUMBERS


PAGE:

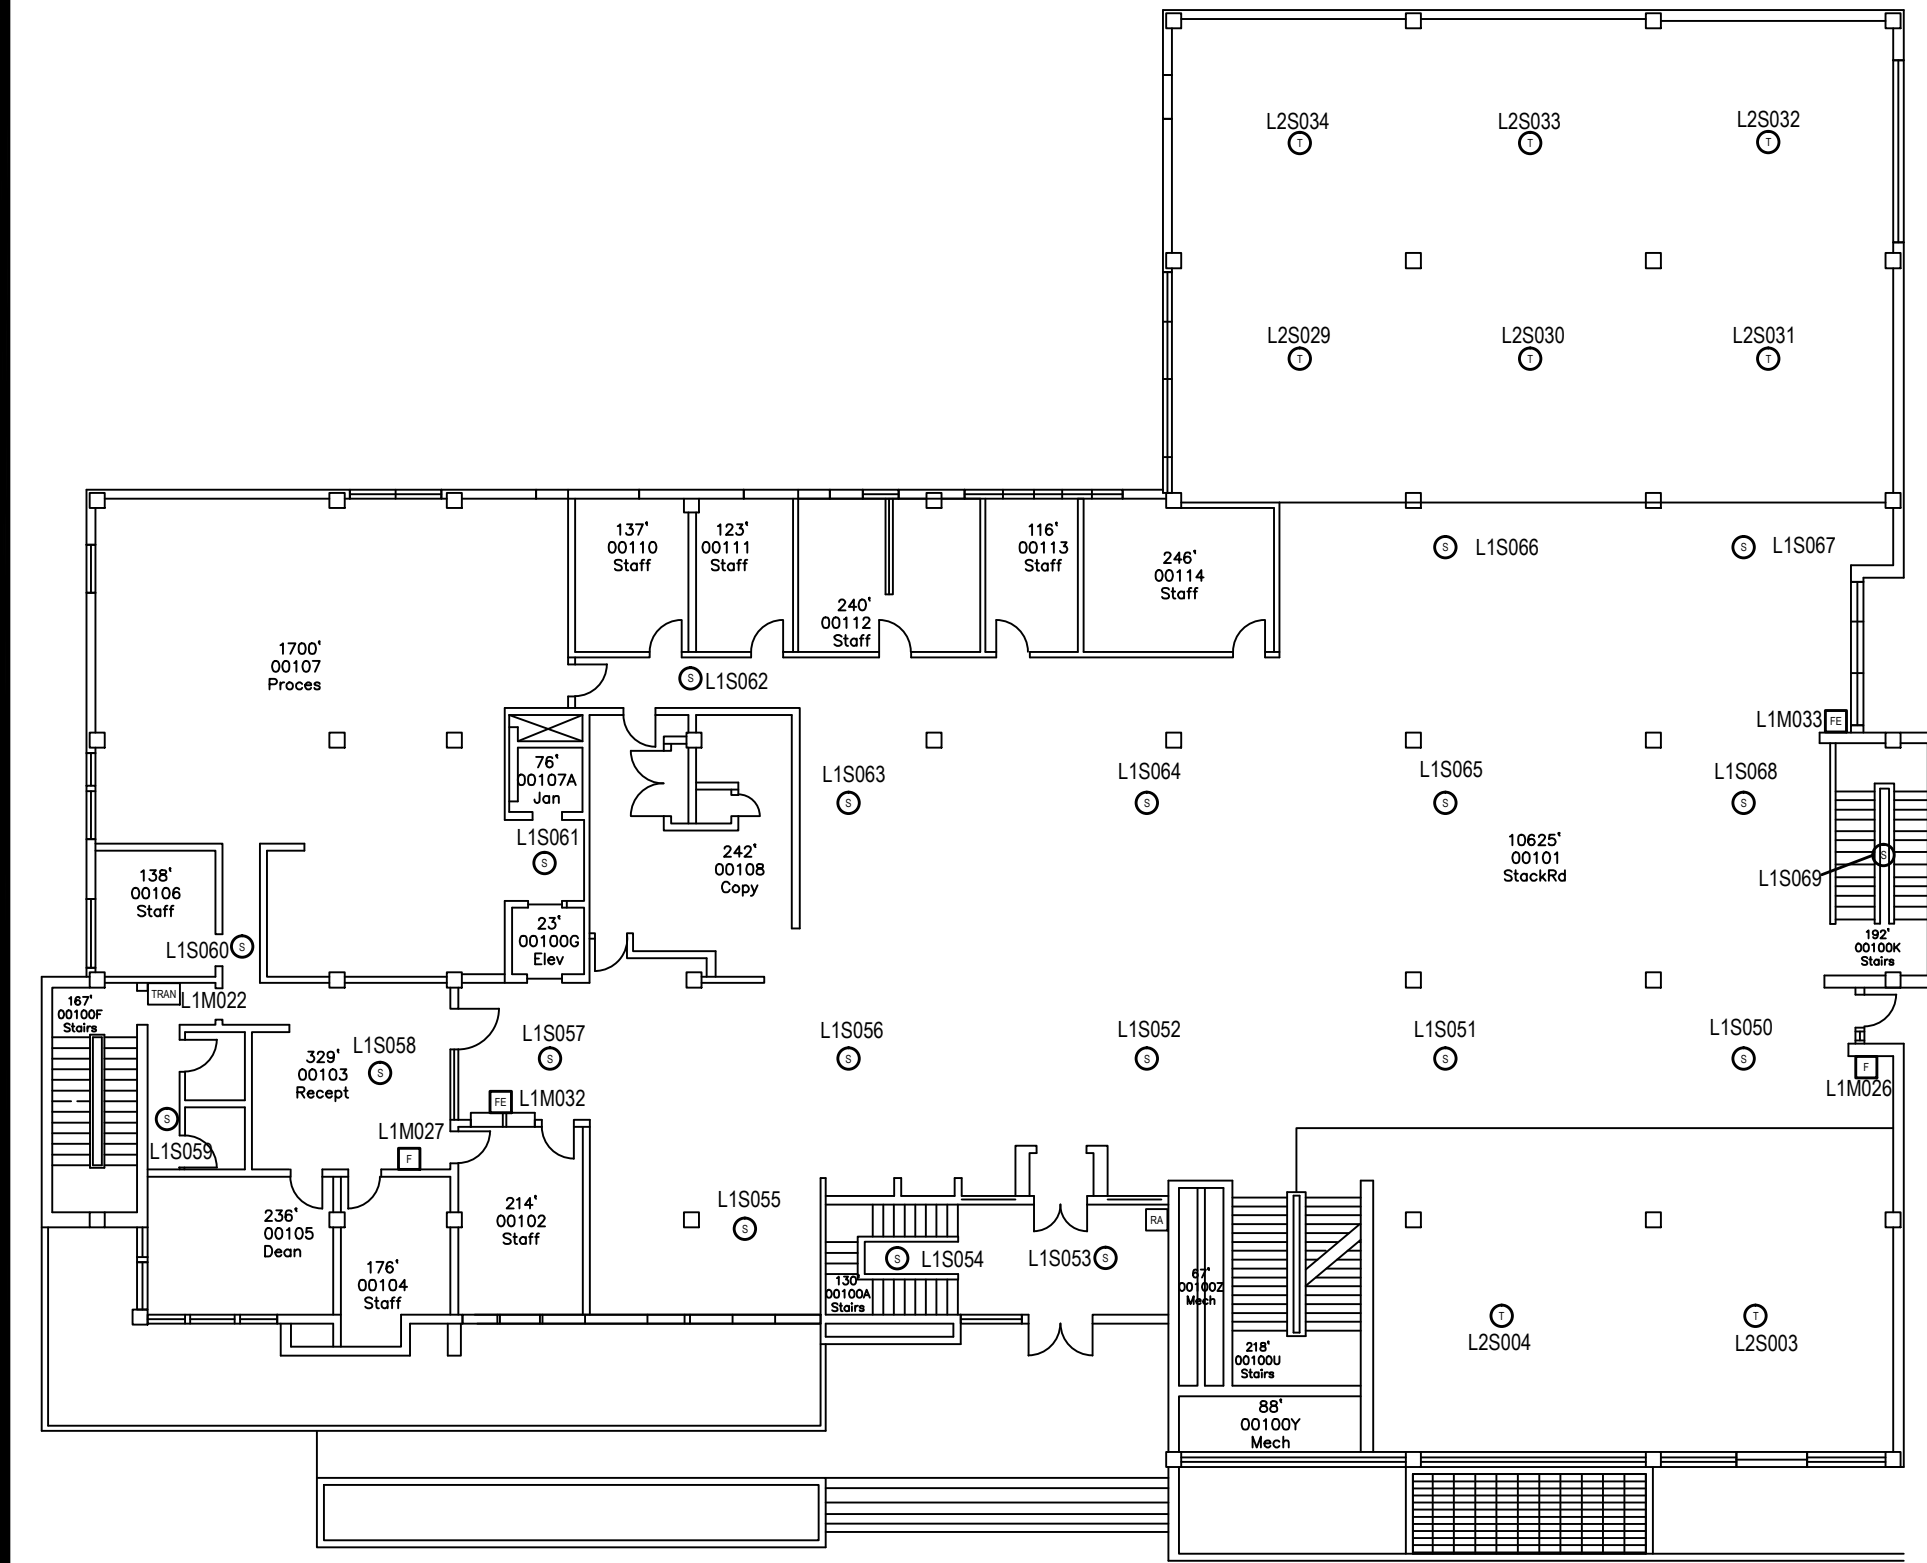

DEVICE LEGEND	
SYMBOL	DESCRIPTION
	SMOKE DETECTOR
	SMOKE DETECTOR ABOVE CEILING
	HEAT DETECTOR
	DUCT DETECTOR
	MANUAL PULL STATION
	HORN/STROBE
	STROBE
	WATERFLOW SWITCH
	TAMPER SWITCH
	MONITOR MODULE
	CONTROL MODULE
	WATERFLOW BELL
	FIRE EXTINGUISHER W/ EN-GAUGE
	REMOTE ANNUNCIATOR
	FIRE ALARM CONTROL PANEL
	TRANSPONDER

WIRE SCHEDULE		
SYMBOL	DESCRIPTION	SIZE
A	ADDRESSABLE CIRCUIT	1 PAIR #14 TWISTED
B	HORN/STROBE CIRCUIT	2 #14'S
C	FAN/DAMPER CONTROL RELAY CIRCUIT	2 #14'S
D	24V DC AUX POWER	2 #14'S
E	REMOTE ANNUNCIATOR	4 PAIR #16'S TWISTED
F	120 VAC POWER WITH GROUND	3 #12'S
G	BELL	24#14'S

- SYSTEM NOTES:
- TO MAIN LEVEL TRANSPONDER
 - TO FACP
 - TO 120 VAC WITH GROUND

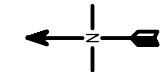

NOTE:
NFS DRAWINGS ARE BASED ON THE PROJECT ARCHITECT/ENGINEER (A/E) PLANS AND SPECIFICATIONS. NFS IS NOT RESPONSIBLE FOR THE ACCURACY OF THE INFORMATION SHOWN ON THE A/E PLANS. NFS IS SOLELY RESPONSIBLE FOR THE ACCURACY OF THE INFORMATION SHOWN ON THE A/E PLANS. NFS IS NOT RESPONSIBLE FOR THE ACCURACY OF THE INFORMATION SHOWN ON THE A/E PLANS. NFS IS SOLELY RESPONSIBLE FOR THE ACCURACY OF THE INFORMATION SHOWN ON THE A/E PLANS.

ECCLES HEALTH SCIENCES LIBRARY
UNIVERSITY OF UTAH
MAIN LEVEL
FIRE ALARM SYSTEM

NFS
NELSON FIRE SYSTEMS
801-468-8300

DRAWN BY: DS
DESIGNED BY: KGE
CHECKED BY: XXXX
DATE: 1/5/2012
SCALE: N.T.S.
PROJECT NO: XXXX
REV NO: XXXX
DRAWING NAME:
HEALTH SCIENCES MAIN.DWG

FIRE ALARM SYSTEM

ADDRESSABLE NUMBERS



PAGE:

DEVICE LEGEND	
SYMBOL	DESCRIPTION
	SMOKE DETECTOR
	SMOKE DETECTOR ABOVE CEILING
	HEAT DETECTOR
	DUCT DETECTOR
	MANUAL PULL STATION
	HORN/STROBE
	STROBE
	WATERFLOW SWITCH
	TAMPER SWITCH
	MONITOR MODULE
	CONTROL MODULE
	WATERFLOW BELL
	FIRE EXTINGUISHER W/ EN-GAUGE
	REMOTE ANNUNCIATOR
	FIRE ALARM CONTROL PANEL
	TRANSPONDER

WIRE SCHEDULE		
SYMBOL	DESCRIPTION	SIZE
A	ADDRESSABLE CIRCUIT	1 PAIR #14 TWISTED
B	HORN/STROBE CIRCUIT	2 #14'S
C	FAN/DAMPER CONTROL RELAY CIRCUIT	2 #14'S
D	24V DC AUX POWER	2 #14'S
E	REMOTE ANNUNCIATOR	4 PAIR #16'S TWISTED
F	120 VAC POWER WITH GROUND	3 #12'S
G	BELL	24#14'S

SYSTEM NOTES:

- TO UPPER LEVEL TRANSPONDER
- TO FACP
- TO 120 VAC WITH GROUND

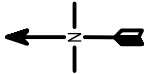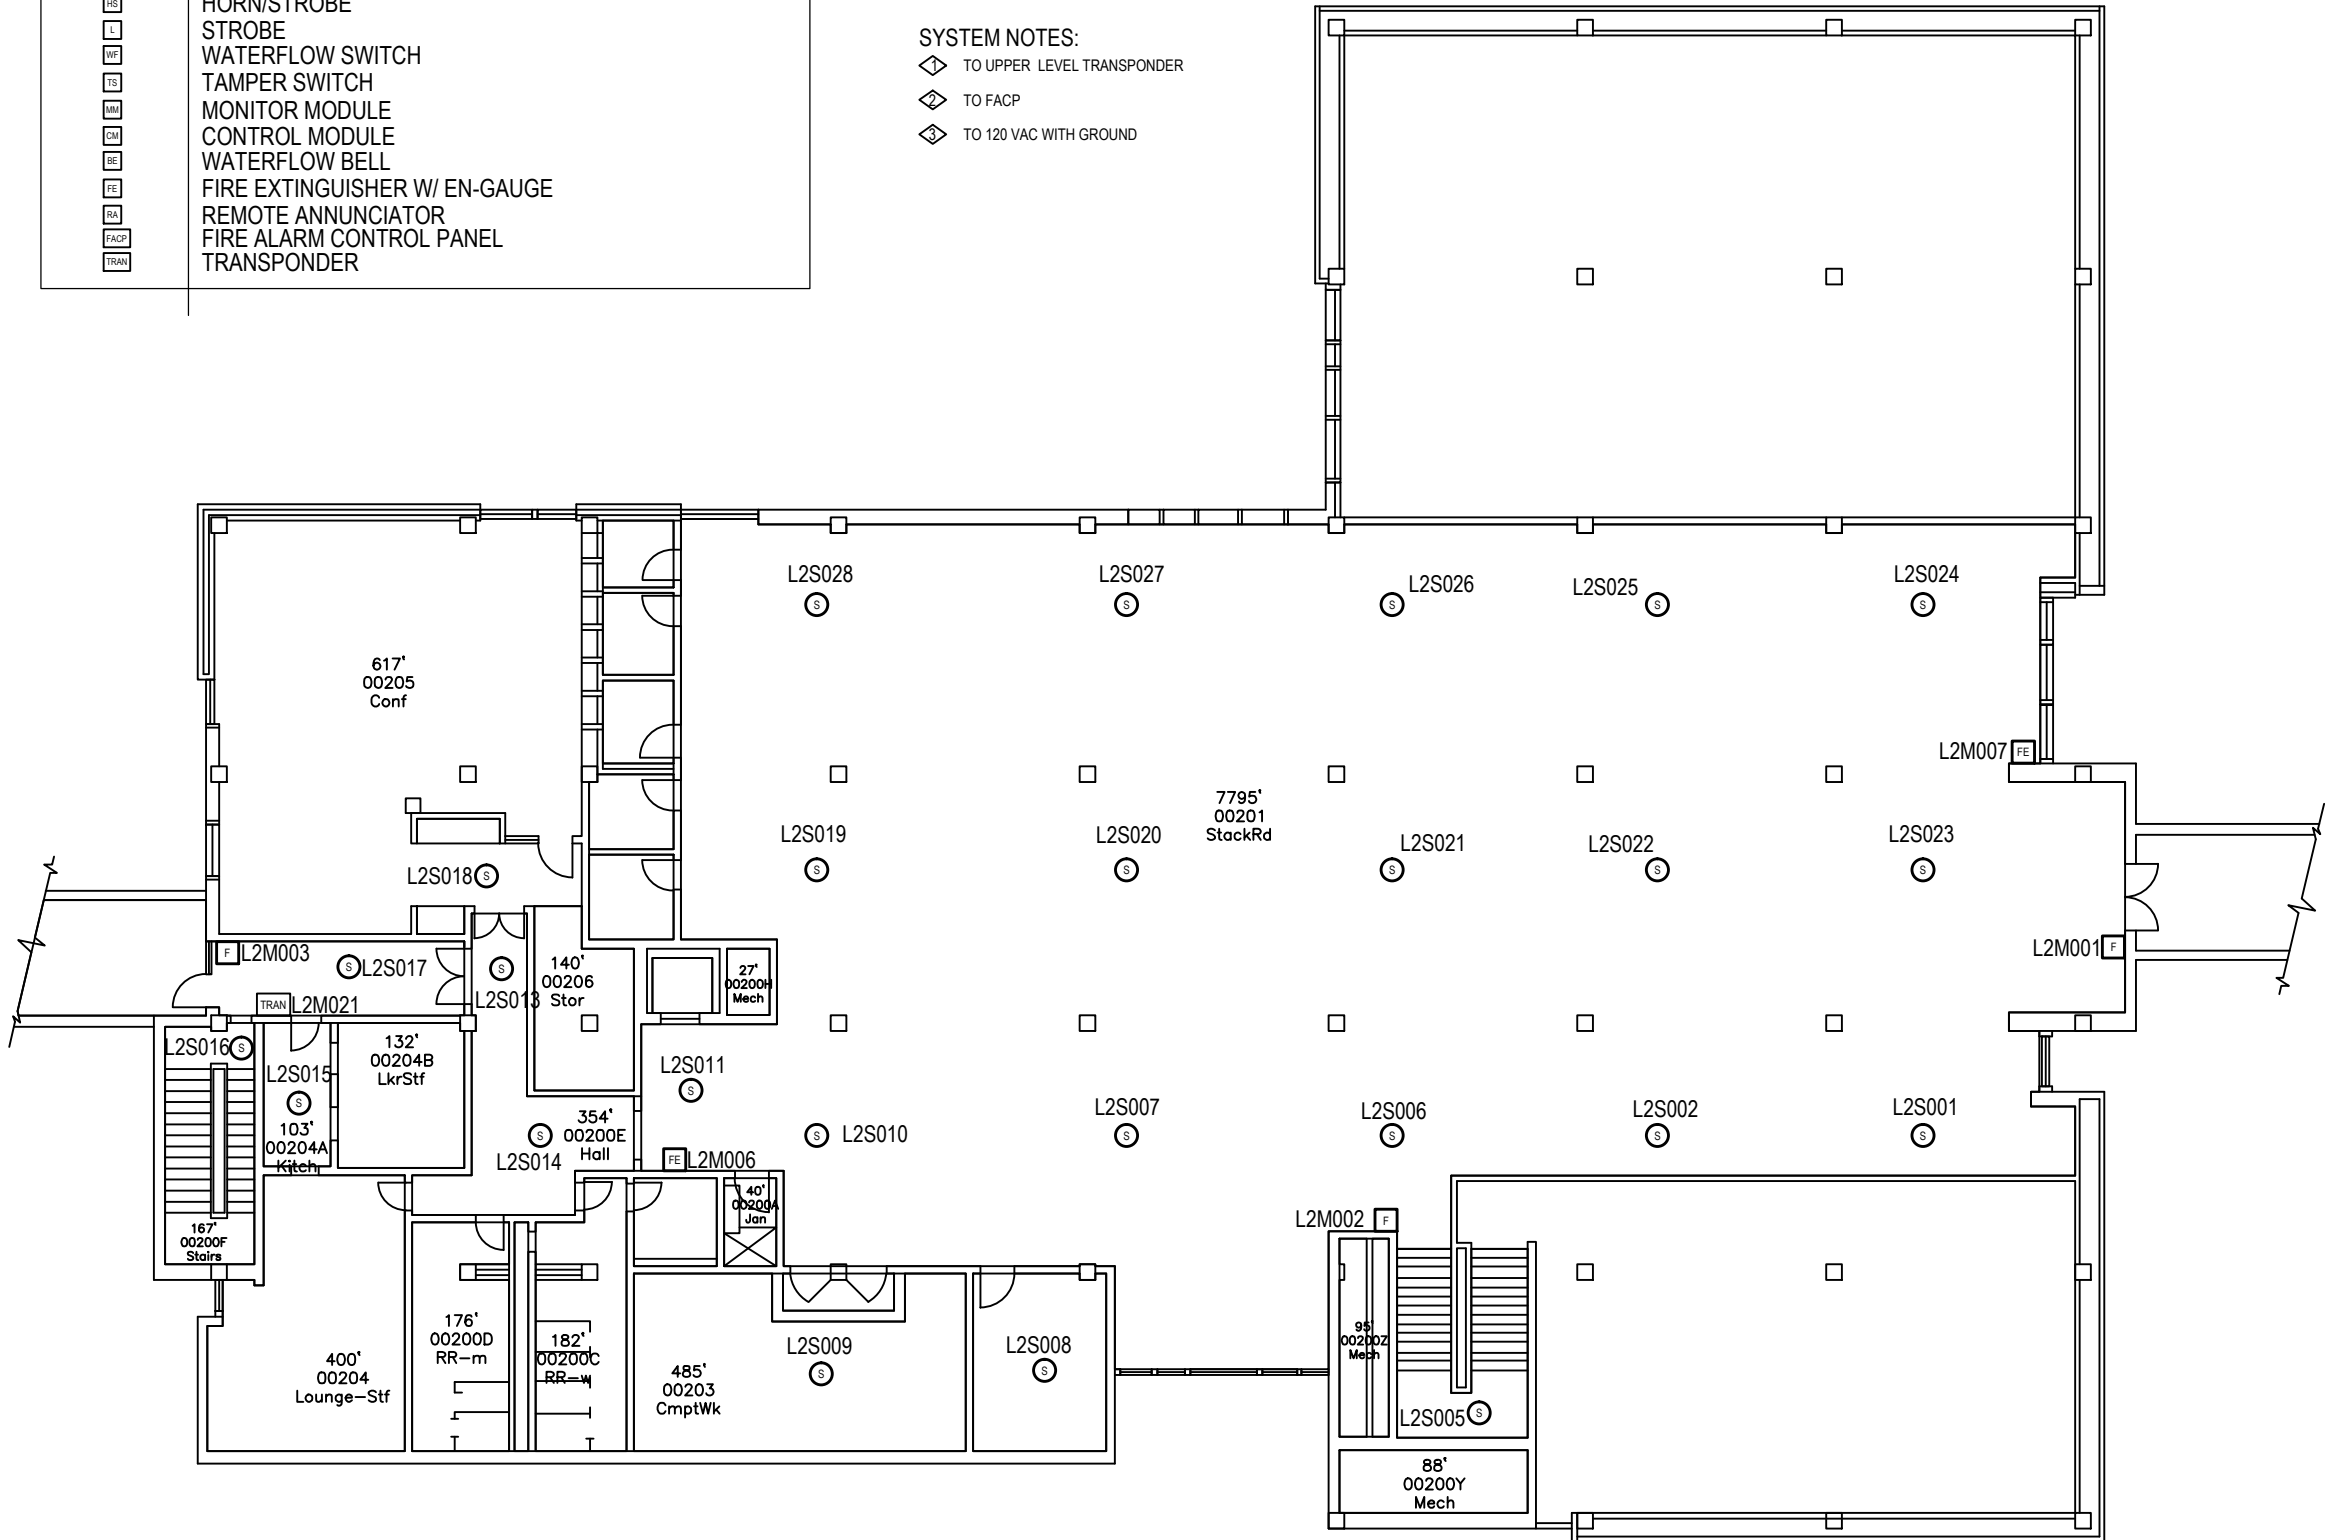

NOTE:
NFS DRAWINGS ARE BASED ON THE PROJECT
ARCHITECT/ENGINEER (A/E) PLANS AND SPECIFICATIONS
FURNISHED TO NFS. A/E IS SOLELY RESPONSIBLE
(NOT NFS) FOR THE TYPE, SIZE, LOCATION, AND
SUITABILITY OF ALL FIRE ALARMS, CONTROL PANELS,
AND OTHER DEVICES SHOWN ON THE A/E PLANS.
NFS DRAWINGS ARE TO SHOW ONLY THE WIRING
DIAGRAMS BETWEEN FIRE ALARM DEVICES AND
CONTROL PANELS. NFS IS NOT RESPONSIBLE FOR
THE INFORMATION SHOWN ON THE A/E PLANS.

ECCLES HEALTH SCIENCES LIBRARY
UNIVERSITY OF UTAH
UPPER LEVEL
FIRE ALARM SYSTEM

NFS

NELSON FIRE SYSTEMS
801-468-8300

DRAWN BY: DS
DESIGNED BY: KGE
CHECKED BY: XXXX
DATE: 1/5/2012
SCALE: N.T.S.
PROJECT NO: XXXX
REV NO: XXXX
DRAWING NAME:
HEALTH SCIENCES UPPER.DWG

FIRE ALARM SYSTEM

ADDRESSABLE NUMBERS

PAGE: