
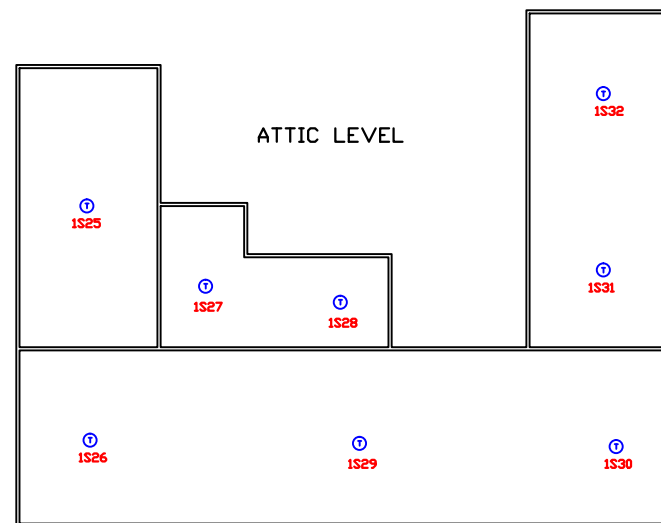


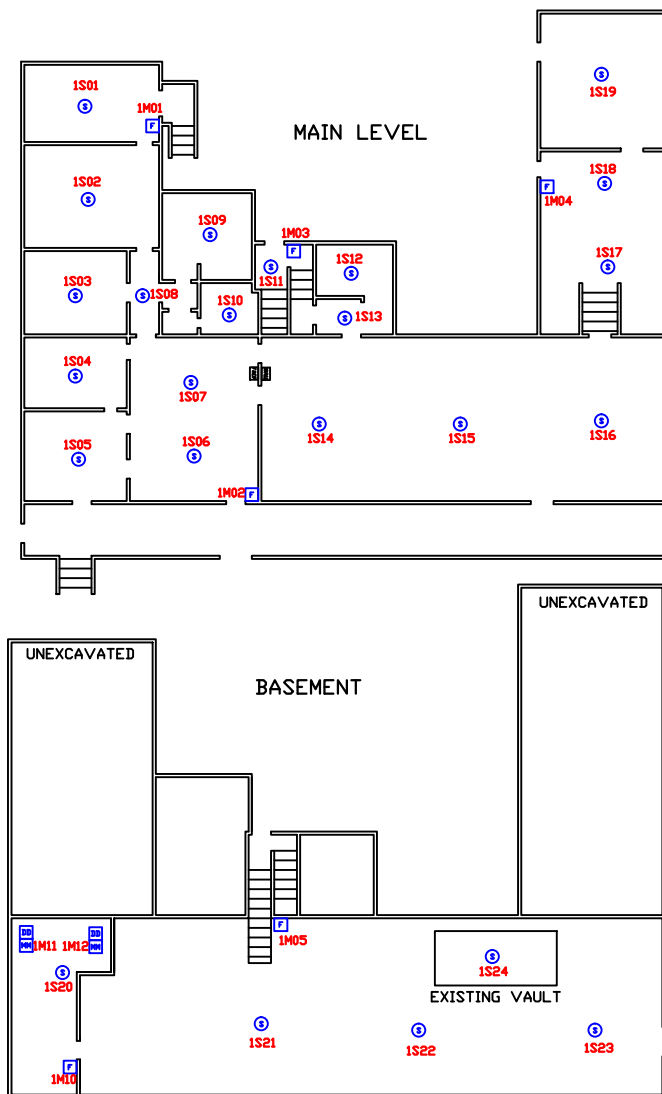

ADDRESS LABEL CLARIFICATION

ADDRESSABLE LOOP NUMBER
SENSOR ("M" MONITOR)
DEVICE NUMBER

1S01

DEVICE LEGEND	
SYMBOL	DESCRIPTION
	SMOKE DETECTOR W/BASE
	THERMAL DETECTOR
	MANUAL PULL STATION
	FIRE ALARM CONTROL PANEL
	TRANSPONDER PANEL



NOTES:
NFS'S DRAWINGS ARE BASED ON THE PROJECT ARCHITECT/ENGINEER LATEST PLANS AND SPECIFICATIONS. NFS IS NOT RESPONSIBLE FOR THE ACCURACY OF THE INFORMATION SHOWN ON THE A/E PLANS. NFS IS NOT RESPONSIBLE FOR THE WIRING AND OTHER DEVICES SHOWN ON THE A/E PLANS. NFS DRAWINGS ARE TO SHOW ONLY THE WIRING AND OTHER DEVICES SHOWN ON THE A/E PLANS. THE INFORMATION SHOWN ON THE A/E PLANS.

FORT DOUGLAS MUSEUM
UNIVERSITY OF UTAH
FIRE ALARM SYSTEM

NFS
NELSON FIRE SYSTEMS
801-468-8300

DRAWN BY: DS
DESIGNED BY: DS
APPROVED BY: DS
DATE: 6/22/2009
SCALE: N.T.S.
PROJECT NO: XXXX
REV NO: XXXX
DRAWING NAME: XXXX.DWG

FIRE ALARM SYSTEM
ADDRESSABLE LOOP NUMBERS

PAGE:
NFS