



0' 10' 20' 25'
SCALE

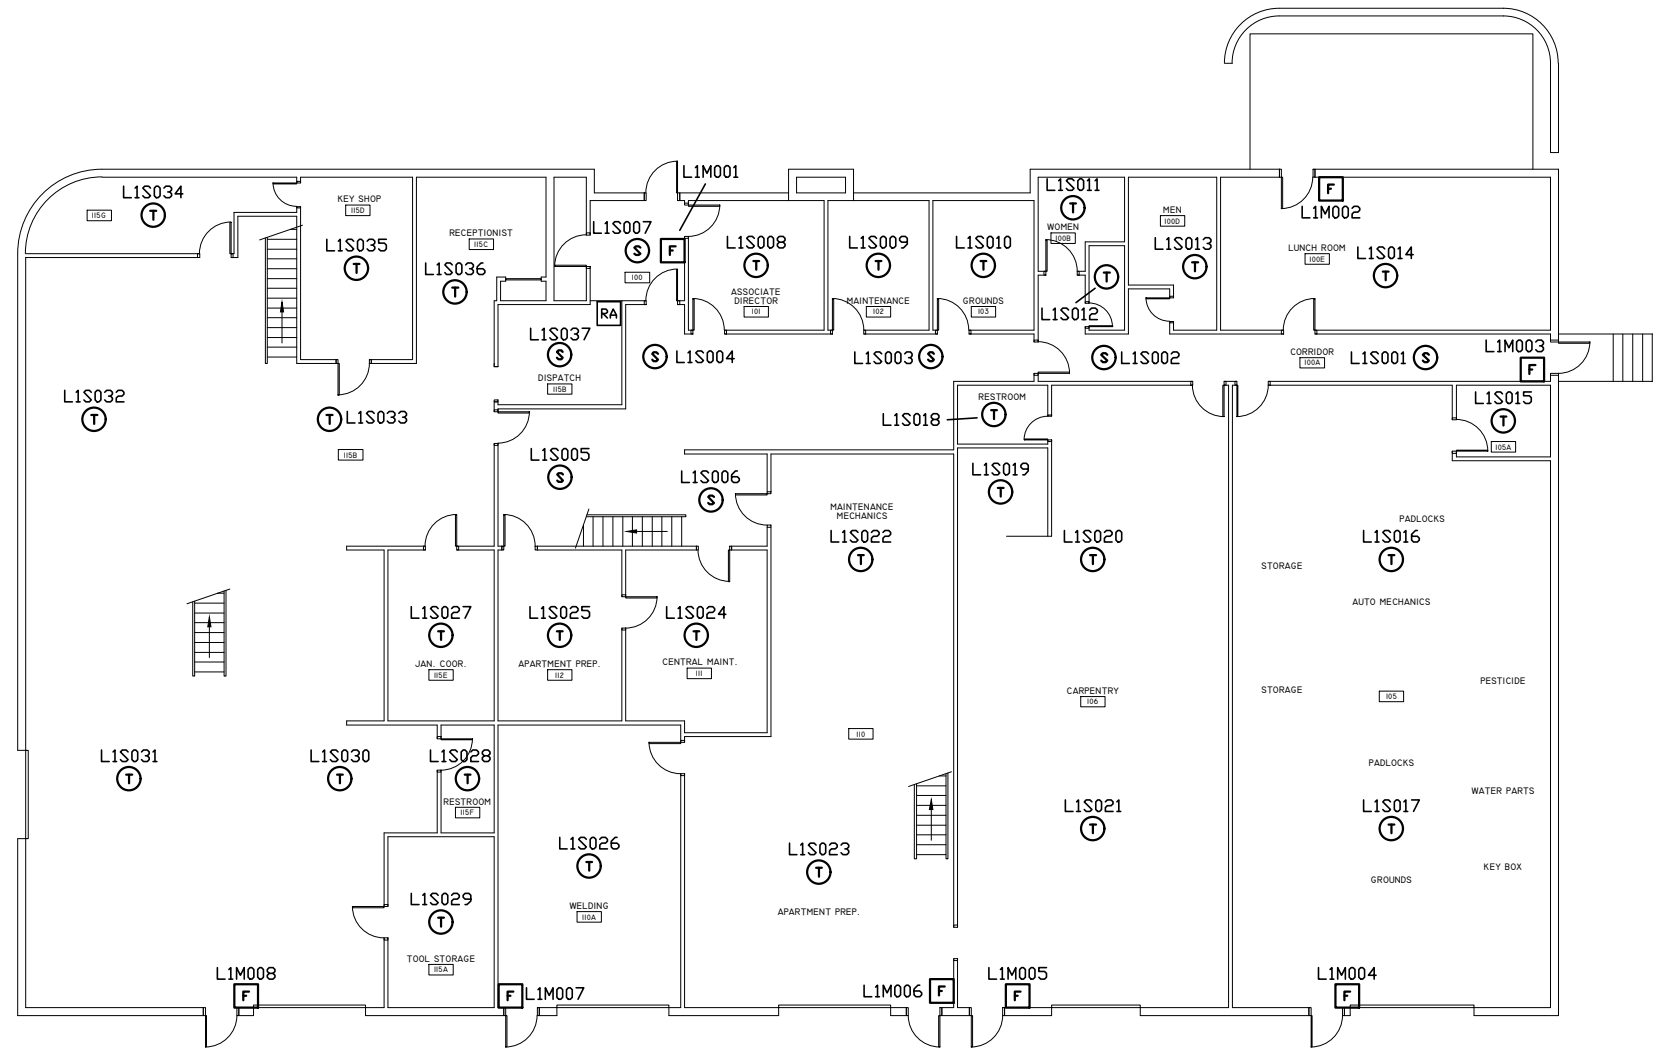

DEVICE LEGEND	
SYMBOL	DESCRIPTION
(S)	SMOKE DETECTOR
(T)	HEAT DETECTOR
(F)	PULL STATION
(L)	STROBE ONLY
(HS)	HORN/STROBE- WALL
(HSC)	HORN/STROBE- CEILING
(HWP)	WEATHERPROOF HORN ONLY
(RA)	REMOTE ANNUNCIATOR
(FACU)	FIRE ALARM CONTROL UNIT
(TRAN)	TRANSPONDER PANEL
(EX)	EXISTING DEVICE LOCATION

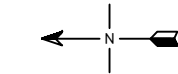

NOTE:
NFS DRAWINGS ARE BASED ON THE PROJECT
ARCHITECTURE/ENGINEER (A/E) PLANS AND
SPECIFICATIONS FURNISHED BY THE A/E. NFS IS SOLELY
RESPONSIBLE (NOT NFS) FOR THE TYPE, SIZE,
LOCATION AND SUITABILITY OF FIRE ALARMS,
CONTROL PANELS AND OTHER DEVICES SHOWN ON
THESE PLANS. NFS DRAWINGS ARE TO SHOW ONLY
THE WIRING DIAGRAMS BETWEEN FIRE ALARM
DEVICES AND CONTROL PANELS. NFS IS NOT
RESPONSIBLE FOR THE INFORMATION SHOWN ON THE
A/E PLANS.

UNIVERSITY OF UTAH
STUDENT APARTMENTS MAINTENANCE FACILITY
BUILDING 720 - MAIN LEVEL
1945 SUNNYSIDE AVE.
SALT LAKE CITY, UTAH 84108
FIRE ALARM SYSTEM

NFS

NELSON FIRE SYSTEMS
801-468-8300

DRAWN BY: AK
DESIGNED BY: XXXX
APPROVED BY: DPS
DATE: 1/5/2016
SCALE: (ANSI B) 1/16" = 1'
PROJECT NO: XXXX
REVISION NO: XXXX
DRAWING NAME:
UofU SAMF BLDG 720 I.DWG



NELSON FIRE SYSTEMS

MAIN LEVEL
NUMBERS


PAGE:

FA-I-04



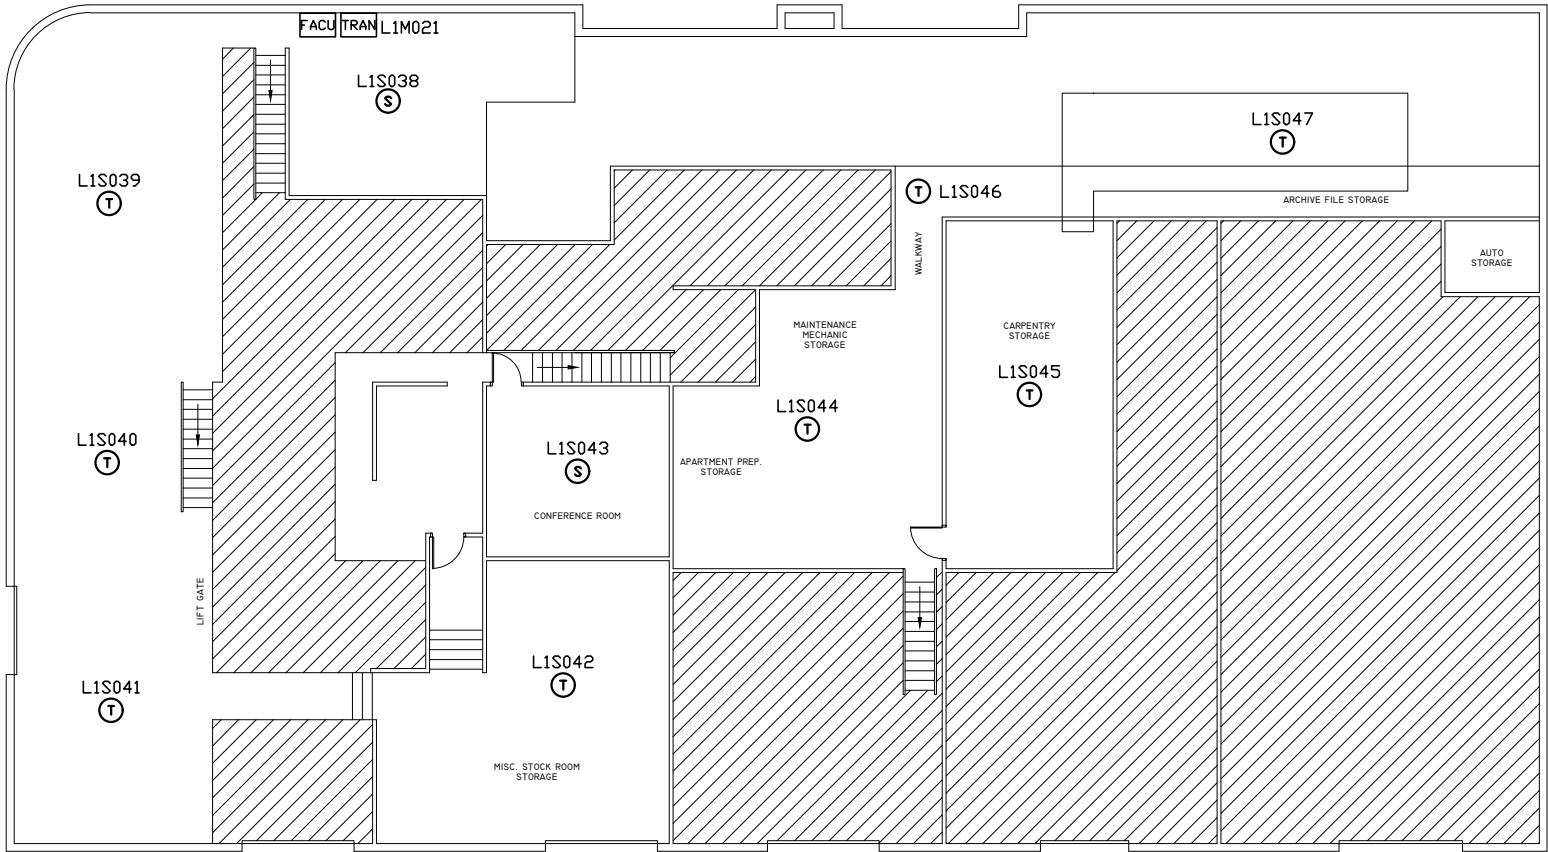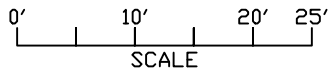

DEVICE LEGEND	
SYMBOL	DESCRIPTION
(S)	SMOKE DETECTOR
(T)	HEAT DETECTOR
F	PULL STATION
L	STROBE ONLY
HS	HORN/STROBE- WALL
HS _C	HORN/STROBE- CEILING
H _{WP}	WEATHERPROOF HORN ONLY
RA	REMOTE ANNUNCIATOR
FACU	FIRE ALARM CONTROL UNIT
TRAN	TRANSPONDER PANEL
EX	EXISTING DEVICE LOCATION

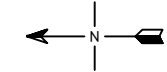

NOTE:
NFS DRAWINGS ARE BASED ON THE PROJECT
ARCHITECTURE/ENGINEER (A/E) PLANS AND
SPECIFICATIONS FURNISHED BY THE A/E. NFS IS SOLELY
RESPONSIBLE (NOT NFS) FOR THE TYPE, SIZE,
LOCATION AND SUBMITTAL OF FIRE ALARMS,
CONTROL PANELS AND OTHER DEVICES SHOWN ON
THESE PLANS. NFS DRAWINGS ARE TO SHOW ONLY
THE WIRING DIAGRAMS BETWEEN FIRE ALARM
DEVICES AND CONTROL PANELS. NFS IS NOT
RESPONSIBLE FOR THE INFORMATION SHOWN ON THE
A/E PLANS.

UNIVERSITY OF UTAH
STUDENT APARTMENTS MAINTENANCE FACILITY
BUILDING 720 - UPPER LEVEL
1945 SUNNYSIDE AVE.
SALT LAKE CITY, UTAH 84108
FIRE ALARM SYSTEM

NFS

NELSON FIRE SYSTEMS
801-468-8300

DRAWN BY:	AK
DESIGNED BY:	XXXX
APPROVED BY:	DPS
DATE:	1/5/2016
SCALE:	(ANSI B) 1/16" = 1'
PROJECT NO:	XXXX
REVISION NO:	XXXX
DRAWING NAME:	UoFU SAMF BLDG 720 2.DWG

NELSON FIRE SYSTEMS
UPPER LEVEL
NUMBERS

PAGE:

FA-2-03

