


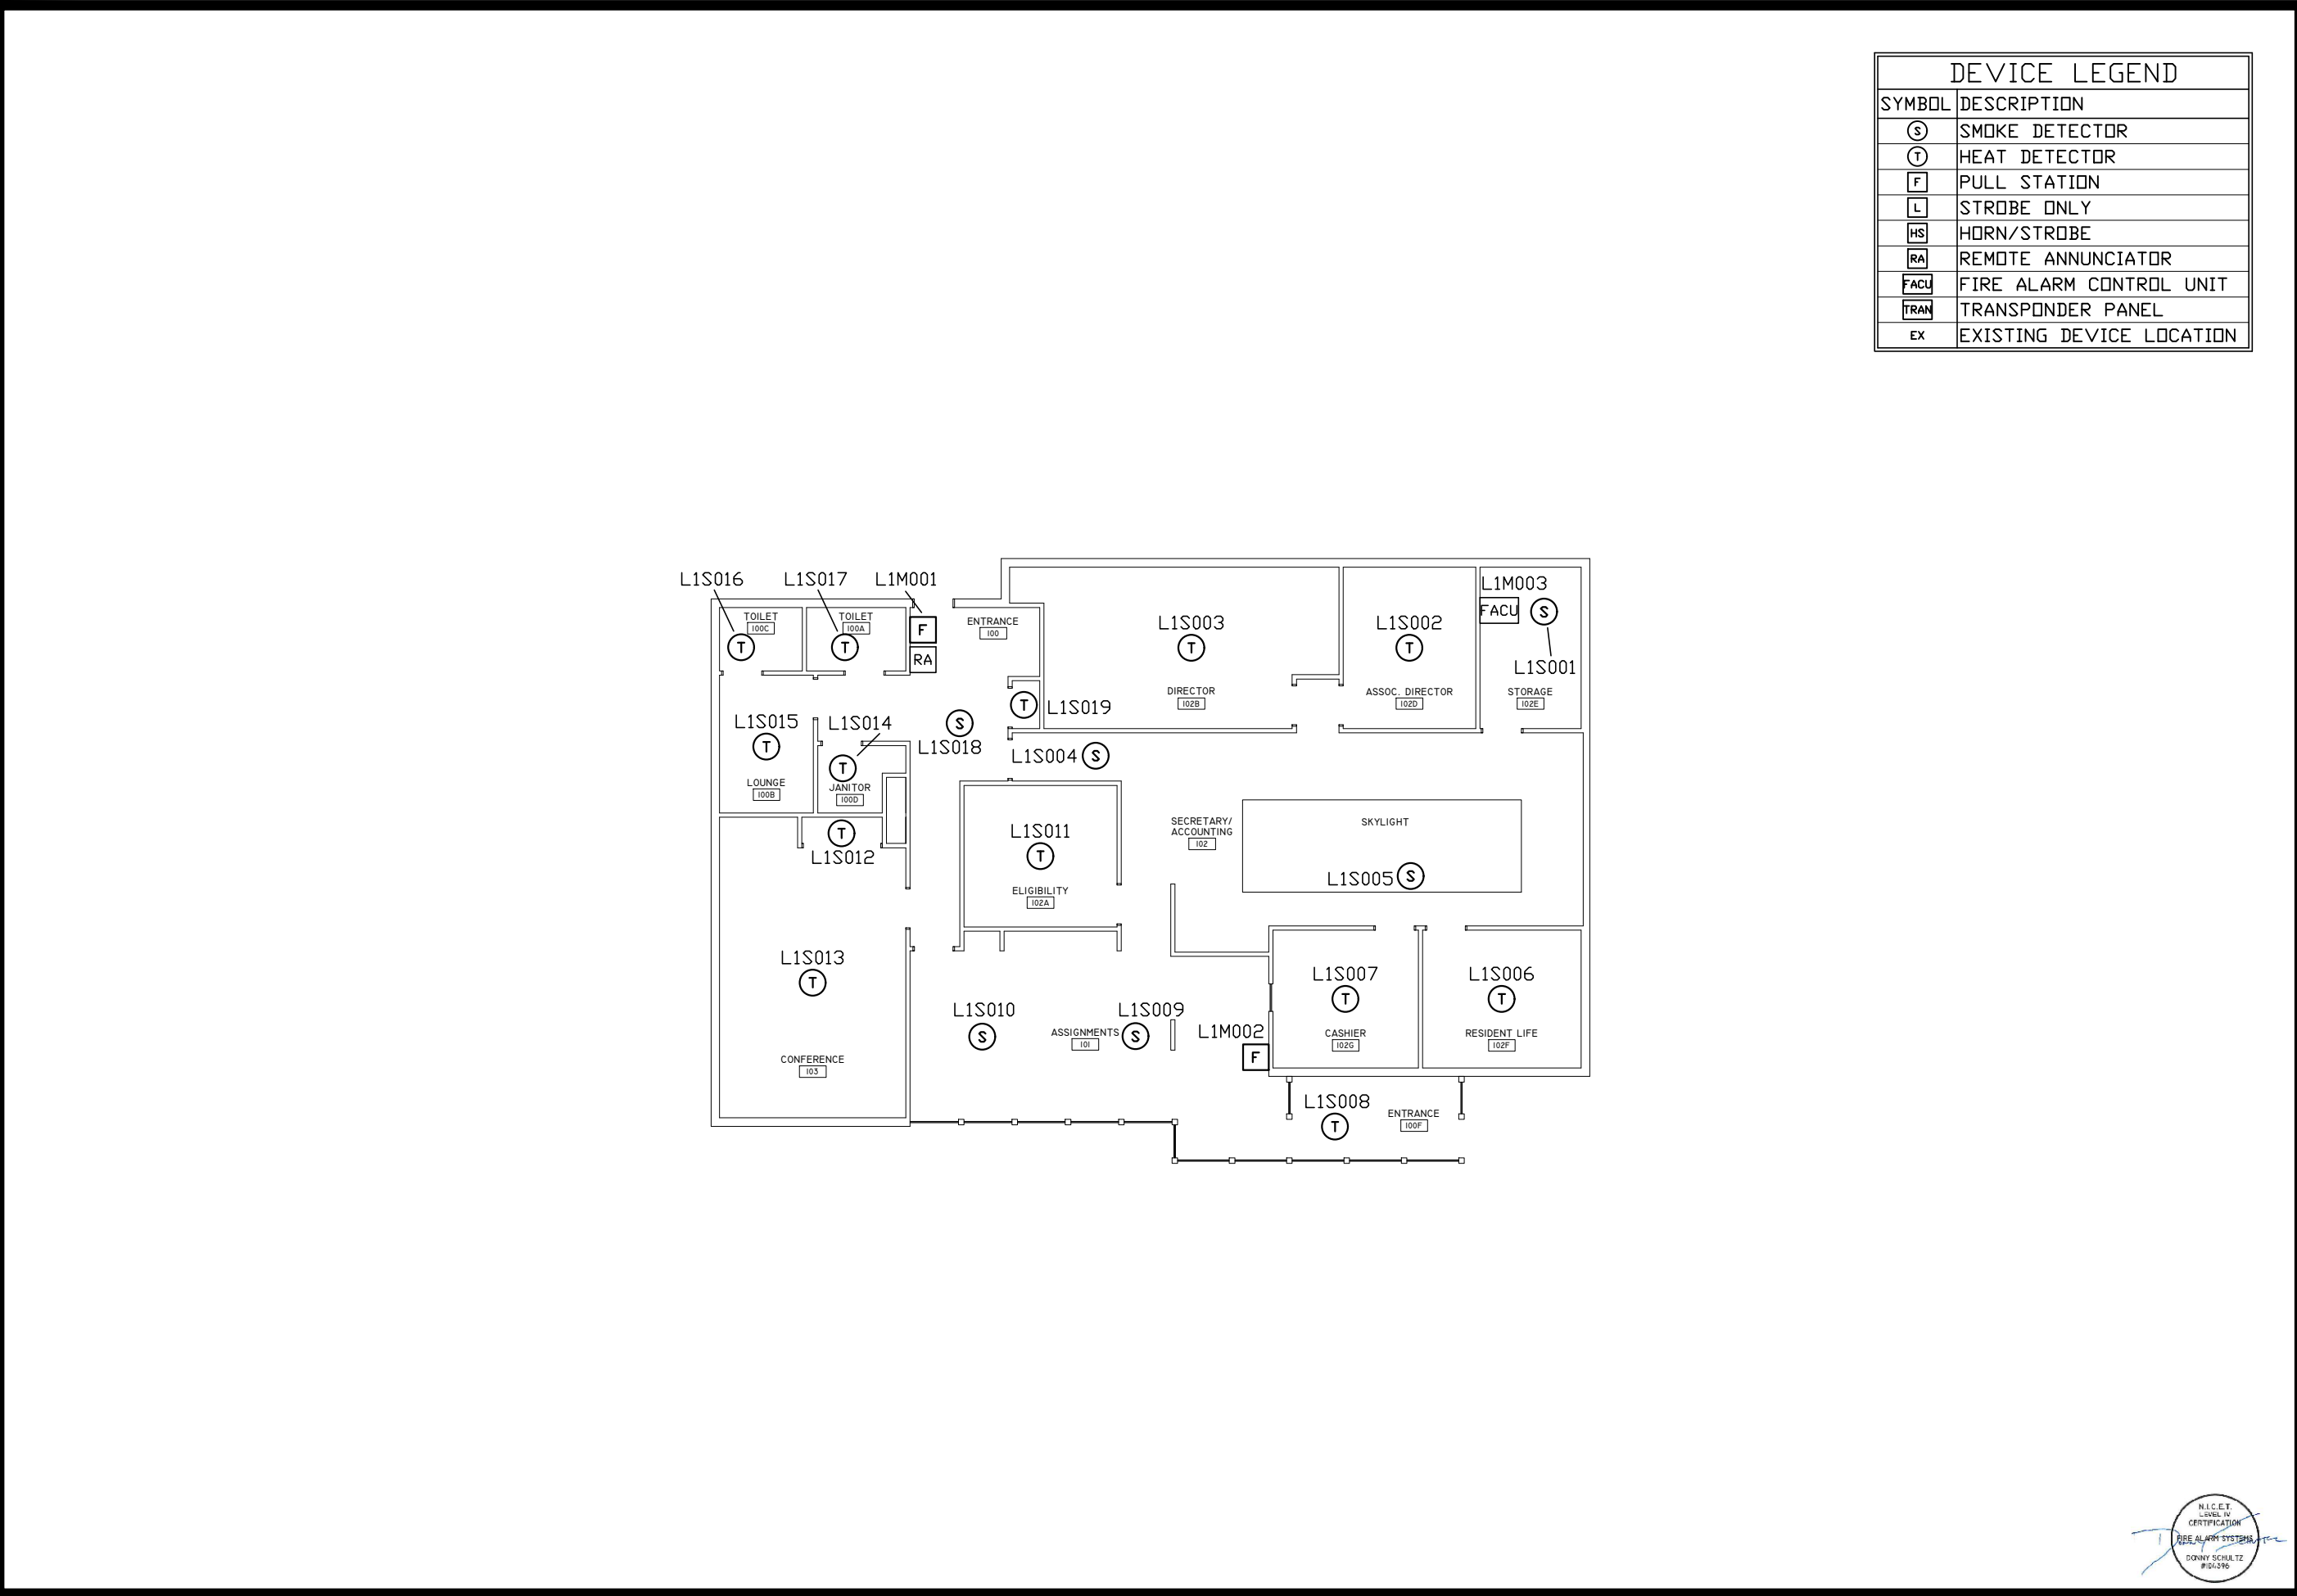

DEVICE LEGEND	
SYMBOL	DESCRIPTION
(S)	SMOKE DETECTOR
(T)	HEAT DETECTOR
F	PULL STATION
L	STROBE ONLY
HS	HORN/STROBE
RA	REMOTE ANNUNCIATOR
FACU	FIRE ALARM CONTROL UNIT
TRAN	TRANSPONDER PANEL
EX	EXISTING DEVICE LOCATION

NOTE:
NFS DRAWINGS ARE BASED ON THE PROJECT ARCHITECTURE/ENGINEER (A/E) PLANS AND SPECIFICATIONS FURNISHED TO NFS. NFS IS SOLELY RESPONSIBLE (NOT NFS) FOR THE TYPE, SIZE, LOCATION AND LABELING OF FIRE ALARMS, CONTROL PANELS AND OTHER DEVICES SHOWN ON THE A/E PLANS. NFS DRAWINGS ARE TO SHOW ONLY THE WIRING DIAGRAMS BETWEEN FIRE ALARM DEVICES AND CONTROL PANELS. NFS IS NOT RESPONSIBLE FOR THE INFORMATION SHOWN ON THE A/E PLANS.

UNIVERSITY OF UTAH
STUDENT APARTMENTS OFFICE
BUILDING 721 - MAIN LEVEL
1945 SUNNYSIDE AVE.
SALT LAKE CITY, UTAH 84108
FIRE ALARM SYSTEM

NFS

NELSON FIRE SYSTEMS
801-468-8300

DRAWN BY:	AK
DESIGNED BY:	XXXX
APPROVED BY:	DPS
DATE:	1/21/2016
SCALE:	NTS
PROJECT NO:	XXXX
REVISION NO:	XXXX
DRAWING NAME:	UofU SAO BLDG 721.DWG

NELSON FIRE SYSTEMS
MAIN LEVEL
FINAL MAP

PAGE:

