



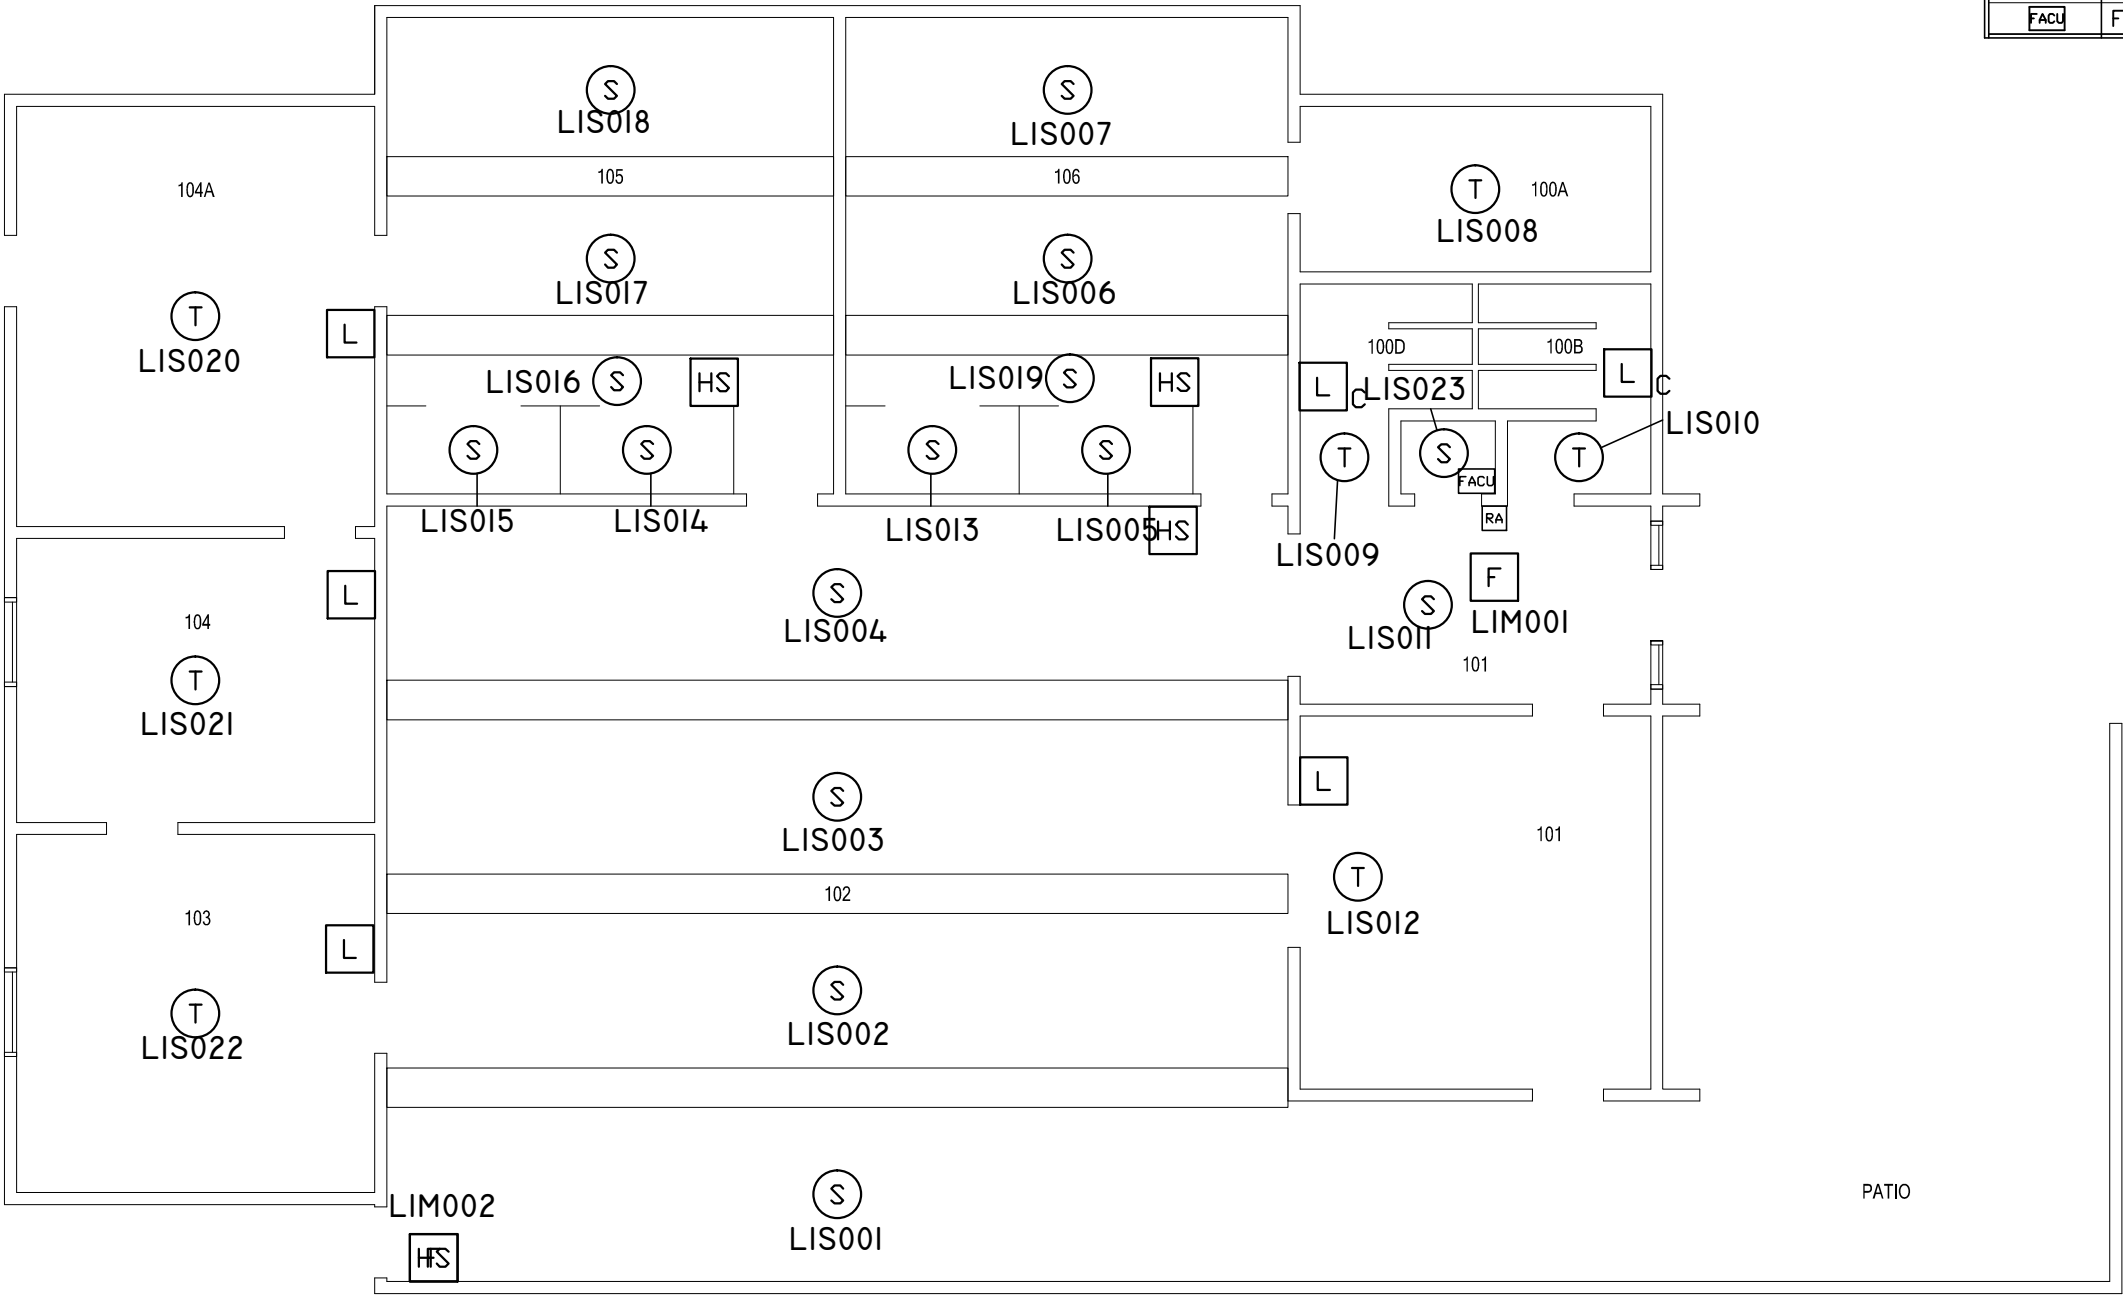

DEVICE LEGEND	
SYMBOL	DESCRIPTION
(S)	SMOKE DETECTOR
(T)	HEAT DETECTOR
[F]	MANUAL PULL STATION
[L]	STROBE ONLY
[HS]	HORN/STROBE
[RA]	REMOTE ANNUNCIATOR
[FACU]	FIRE ALARM CONTROL UNIT

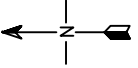

NOTE:
NFS DRAWINGS ARE BASED ON THE PROJECT
ARCHITECT/ENGINEER (A/E) PLANS AND SPECIFICATIONS
FURNISHED TO NFS. A/E IS SOLELY RESPONSIBLE
(NOT NFS) FOR THE TYPE, SIZE, LOCATION, AND
SUITABILITY OF ALL FIRE ALARMS, CONTROL PANELS,
AND OTHER DEVICES SHOWN ON THE A/E PLANS.
NFS DRAWINGS ARE TO SHOW ONLY THE WIRING
DIAGRAMS BETWEEN FIRE ALARM DEVICES AND
CONTROL PANELS. NFS IS NOT RESPONSIBLE FOR
THE INFORMATION SHOWN ON THE A/E PLANS.

BUILDING 760
UNIVERSITY OF UTAH
LEVEL I
FIRE ALARM SYSTEM

NFS

NELSON FIRE SYSTEMS

801-468-8300

DRAWN BY:	AK
DESIGNED BY:	XXXX
APPROVED BY:	BN
DATE:	8/5/14
SCALE:	(ANSI B) 1/16"=1'
PROJECT NO:	XXXX
REV NO:	XXXX
DRAWING NAME:	BUILDING 760.DWG

FIRE ALARM SYSTEM
LEVEL I
NUMBERS

