



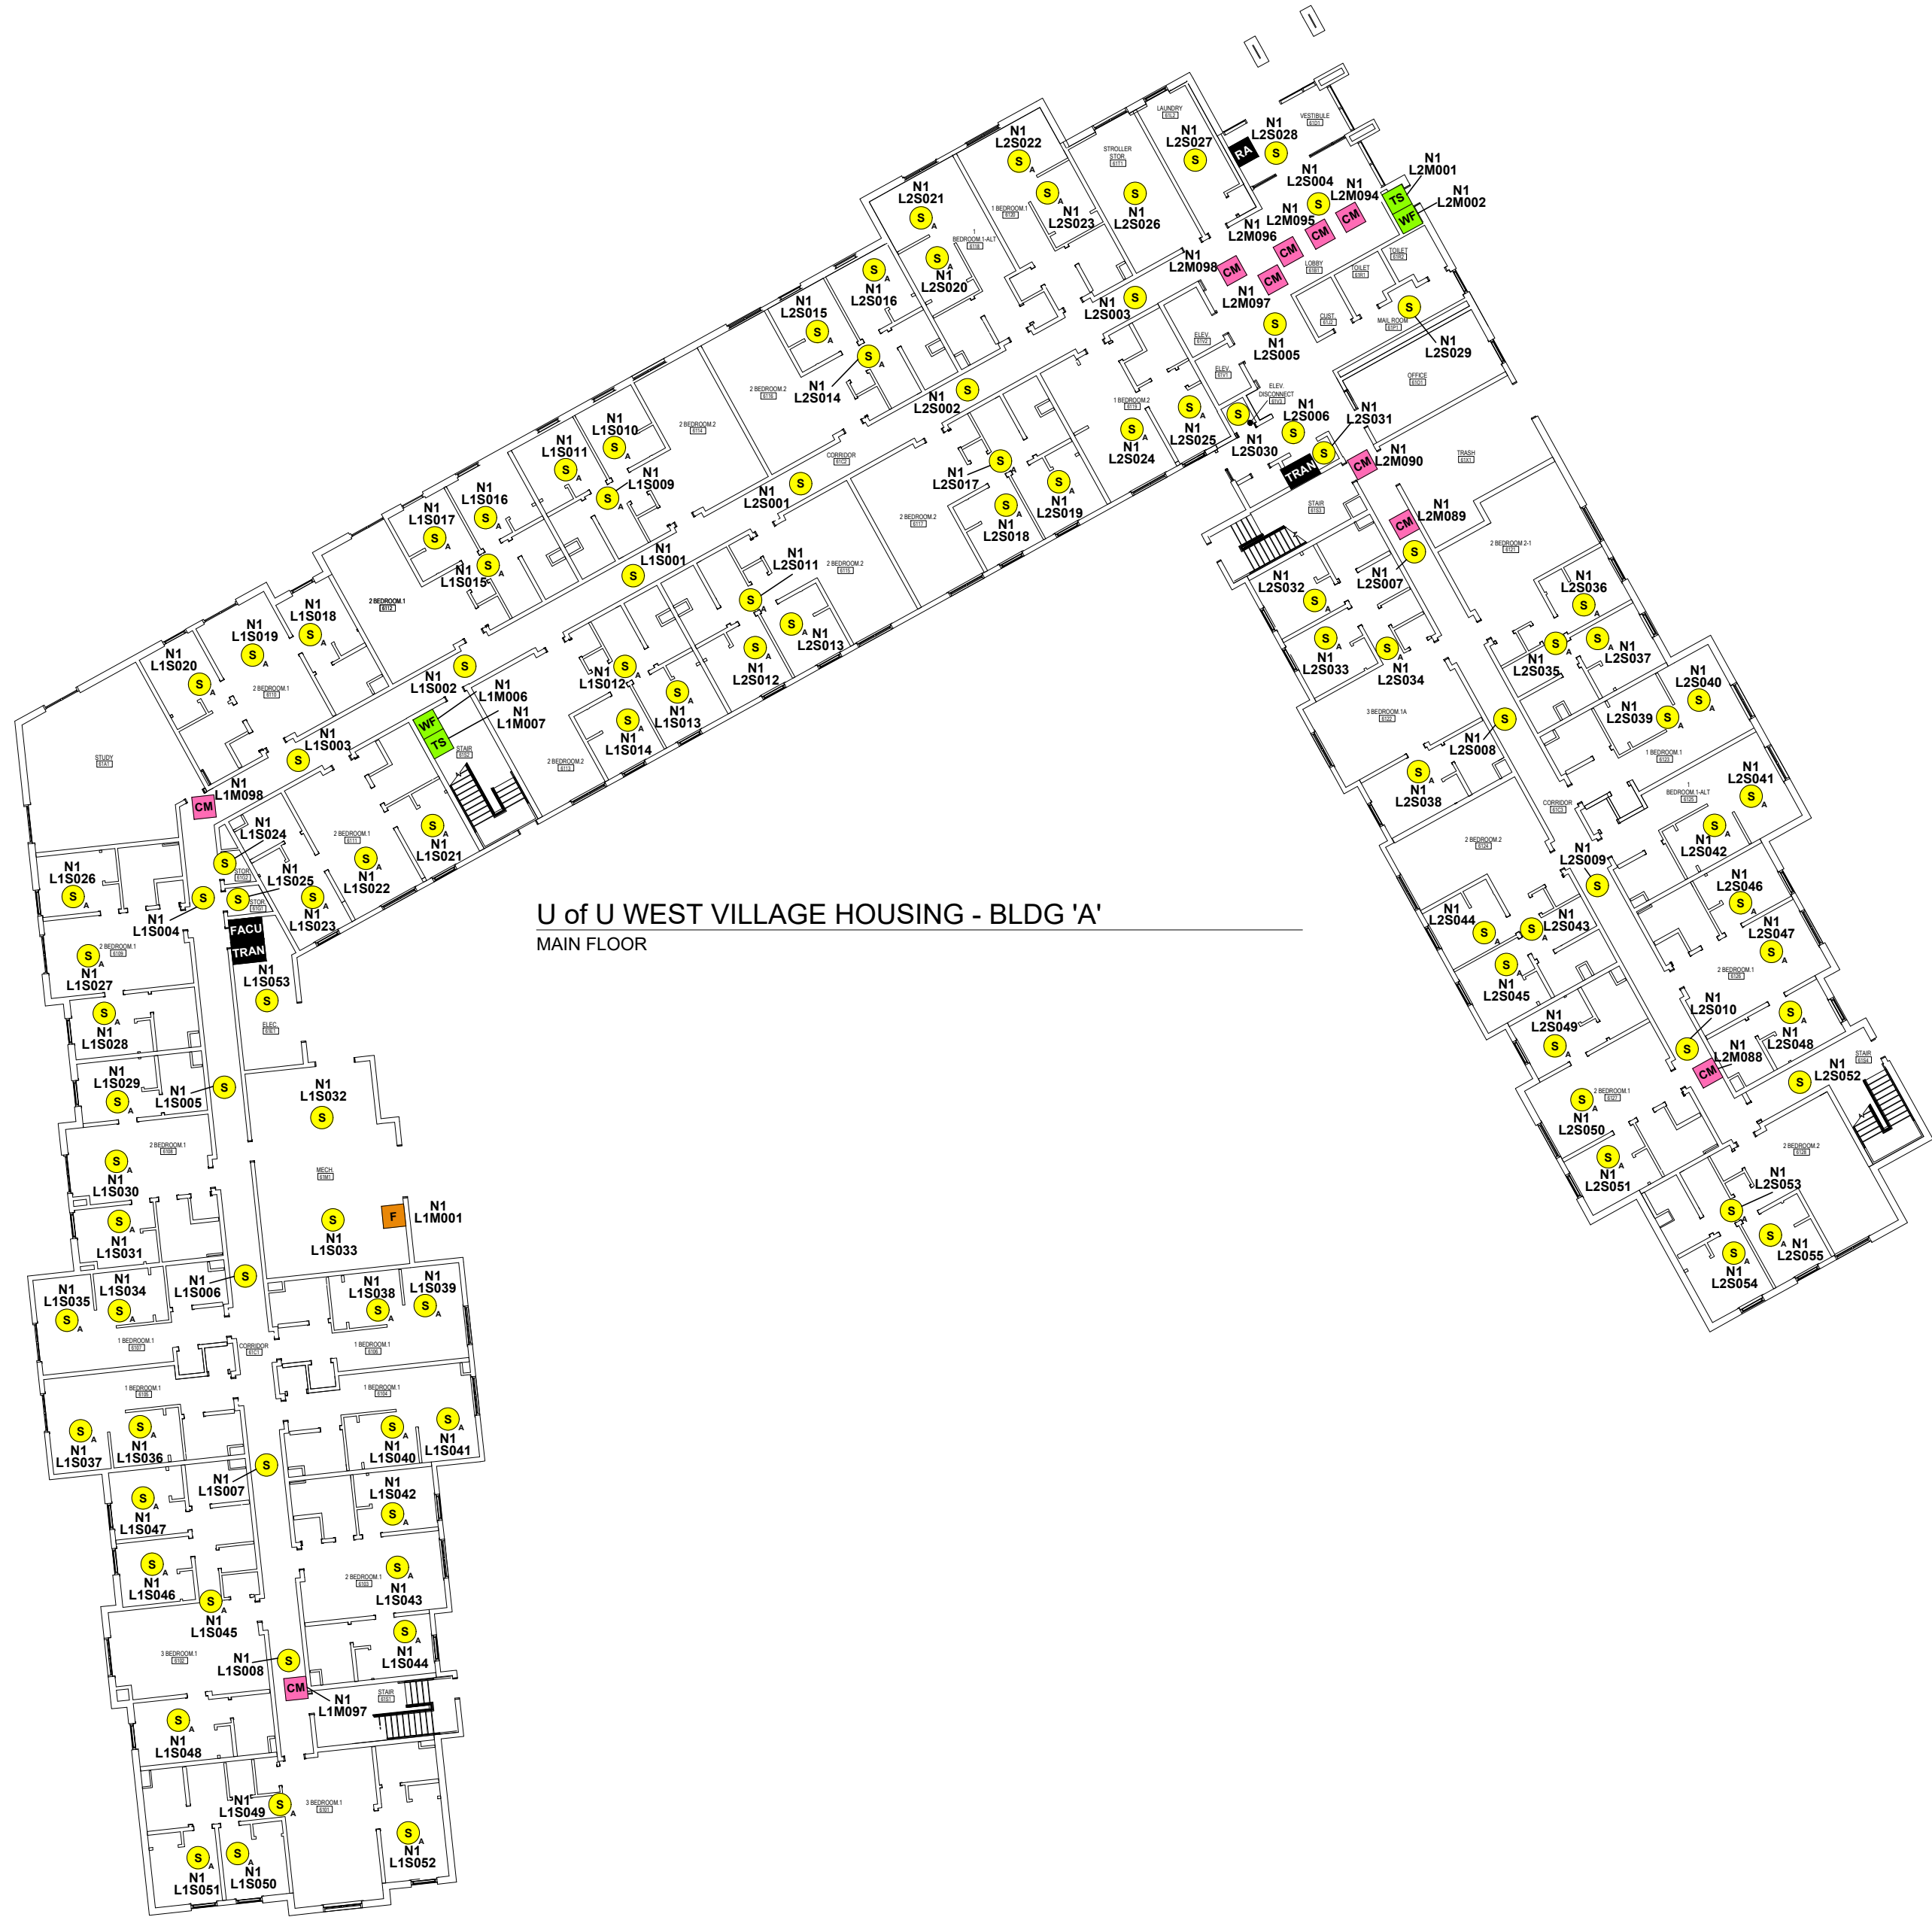


U of U WEST VILLAGE HOUSING - BLDG 'A'
MAIN FLOOR

KEY PLAN

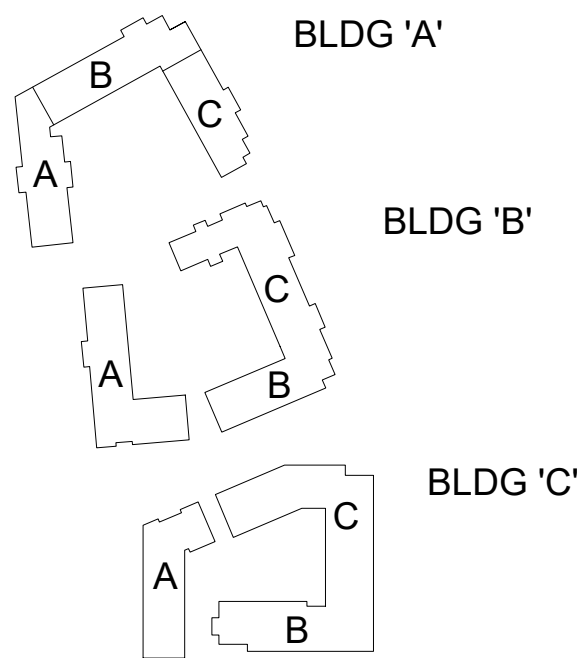

DEVICE LEGEND	
SYMBOL	DESCRIPTION
	SMOKE DETECTOR
	SMOKE DETECTOR- AUDIBLE BASE
	PULL STATION
	DUCT DETECTOR
	WATER FLOW SWITCH MODULE
	TAMPER SWITCH MODULE
	CONTROL MODULE
	REMOTE ANNUNCIATOR
	FIRE ALARM CONTROL UNIT
	TRANSPONDER PANEL

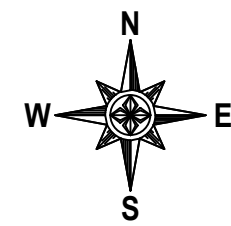

NOTE: ALL DRAWINGS ARE BASED ON THE PROJECT ARCHITECTURE (A/E) PLANS AND SPECIFICATIONS FURNISHED TO NFS. NFS IS SOLELY RESPONSIBLE (NOT NFS) FOR THE TYPE, SIZE, LOCATION, AND SUITABILITY OF ALL FIRE ALARMS, CONTROL PANELS, AND OTHER DEVICES SHOWN ON THE A/E PLANS. NFS DRAWINGS ARE TO SHOW ONLY THE WIRING DIAGRAMS BETWEEN FIRE ALARM DEVICES AND CONTROL PANELS. NFS IS NOT RESPONSIBLE FOR THE INFORMATION SHOWN ON THE A/E PLANS.

WEST VILLAGE HOUSING - BUILDING 'A'
UNIVERSITY OF UTAH
SUNNYSIDE AVENUE AND FOOTHILL DRIVE
SALT LAKE CITY, UTAH 84108
FIRE ALARM SYSTEM


NFS
NELSON FIRE SYSTEMS
801-468-8300

DRAWN BY: BH
DESIGNED BY: XXXX
APPROVED BY: KK
DATE: 09/04/2023
SCALE: N.T.S.
PROJECT NO: XXXX
REVISION NO: XXXX
DRAWING NAME:
BUILDING A 1ST FLOOR FM.DWG


NELSON FIRE SYSTEMS
MAIN LEVEL

PAGE:
FINAL MAP



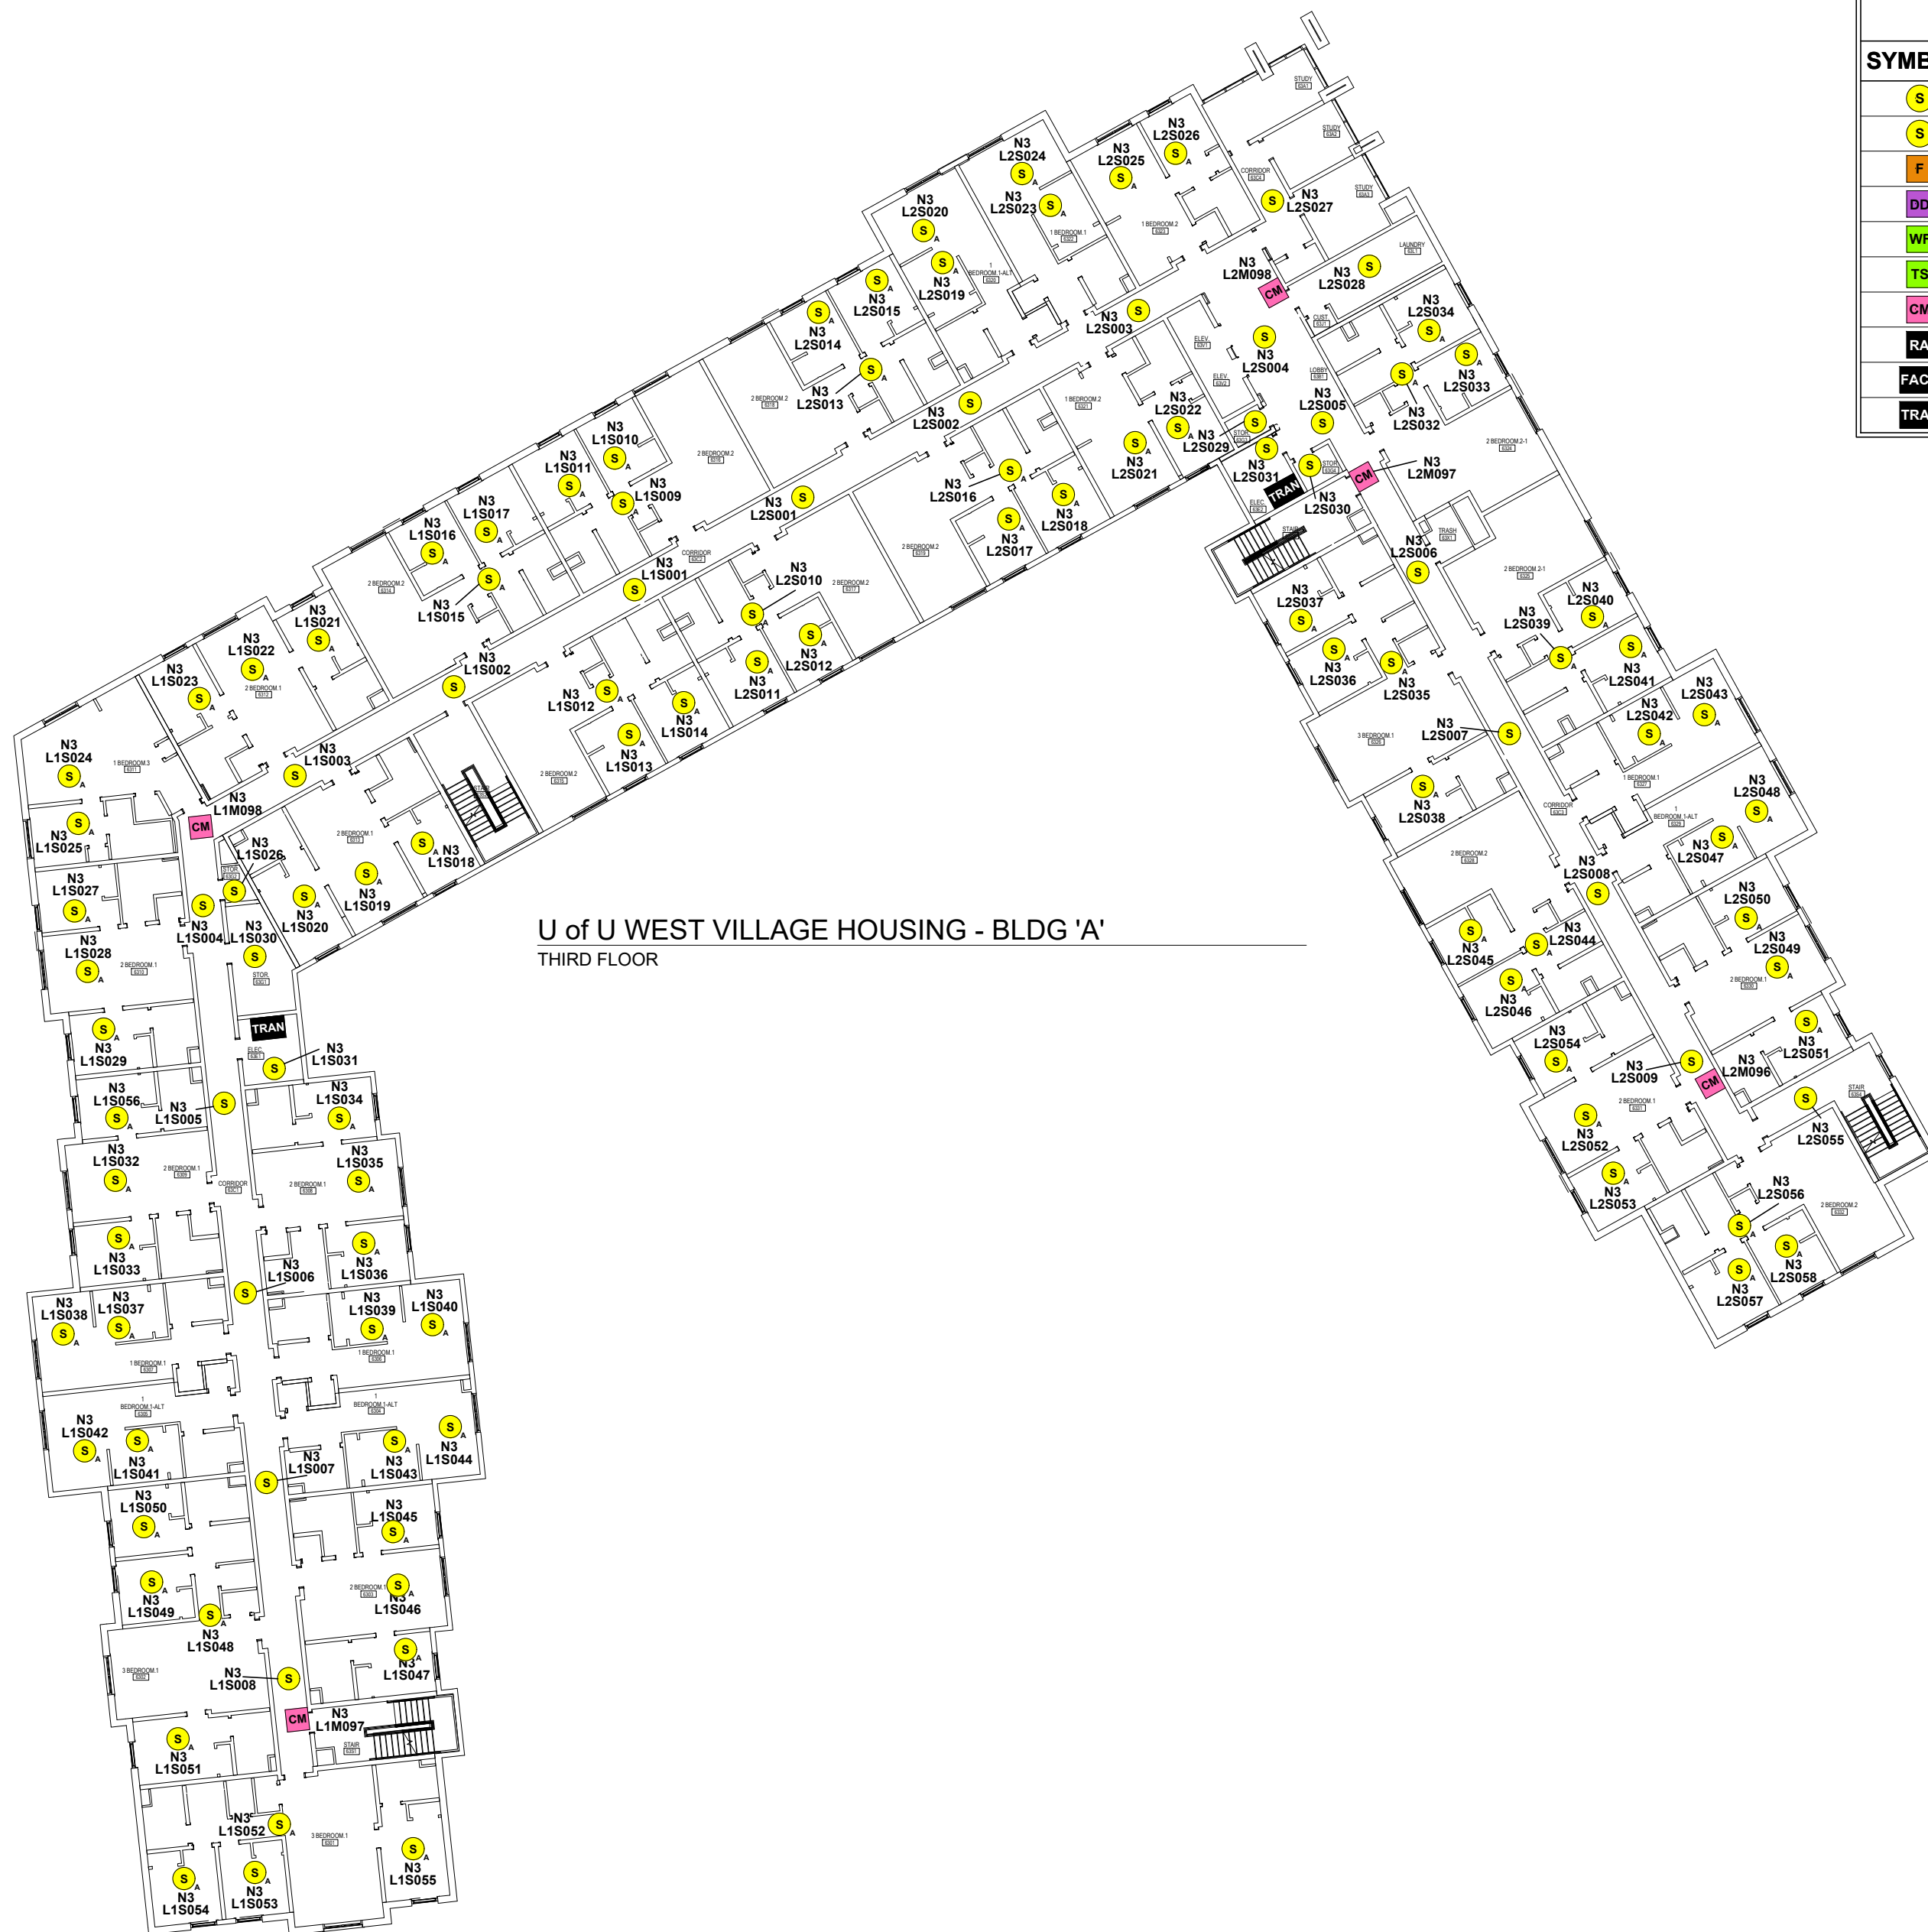

DEVICE LEGEND	
SYMBOL	DESCRIPTION
	SMOKE DETECTOR
	SMOKE DETECTOR- AUDIBLE BASE
	PULL STATION
	DUCT DETECTOR
	WATER FLOW SWITCH MODULE
	TAMPER SWITCH MODULE
	CONTROL MODULE
	REMOTE ANNUNCIATOR
	FIRE ALARM CONTROL UNIT
	TRANSPONDER PANEL

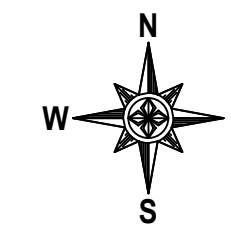

NOTE: ALL DRAWINGS ARE BASED ON THE PROJECT ARCHITECTURE (A/E) PLANS AND SPECIFICATIONS FURNISHED TO NFS. NFS IS SOLELY RESPONSIBLE (NOT NFS) FOR THE TYPE, SIZE, LOCATION, AND SUITABILITY OF ALL FIRE ALARMS, CONTROL PANELS, AND OTHER DEVICES SHOWN ON THE A/E PLANS. NFS DRAWINGS ARE TO SHOW ONLY THE WIRING DIAGRAMS BETWEEN FIRE ALARM DEVICES AND CONTROL PANELS. NFS IS NOT RESPONSIBLE FOR THE INFORMATION SHOWN ON THE A/E PLANS.

WEST VILLAGE HOUSING - BUILDING 'A'
UNIVERSITY OF UTAH
SUNNYSIDE AVENUE AND FOOTHILL DRIVE
SALT LAKE CITY, UTAH 84108
FIRE ALARM SYSTEM

NFS
NELSON FIRE SYSTEMS
801-468-8300


DRAWN BY: BH
DESIGNED BY: XXXX
APPROVED BY: KK
DATE: 09/05/2023
SCALE: N.T.S.
PROJECT NO: XXXX
REVISION NO: XXXX
DRAWING NAME:
BUILDING A 3RD FLOOR FM.DWG


NELSON FIRE SYSTEMS
LEVEL 3

PAGE:
FINAL MAP




KEY PLAN

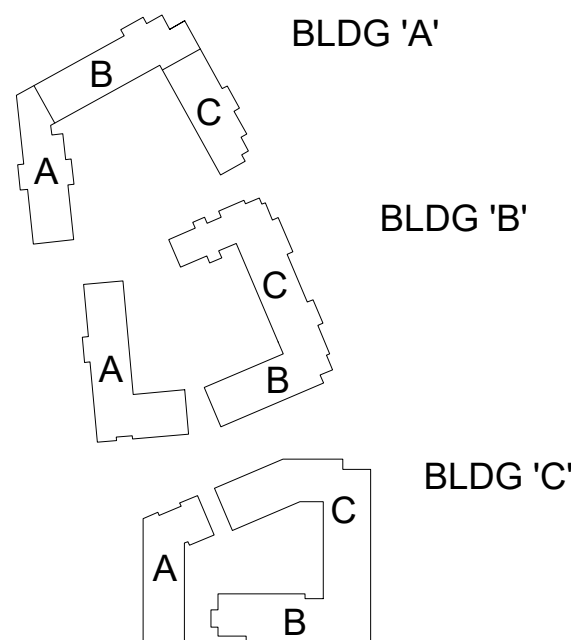

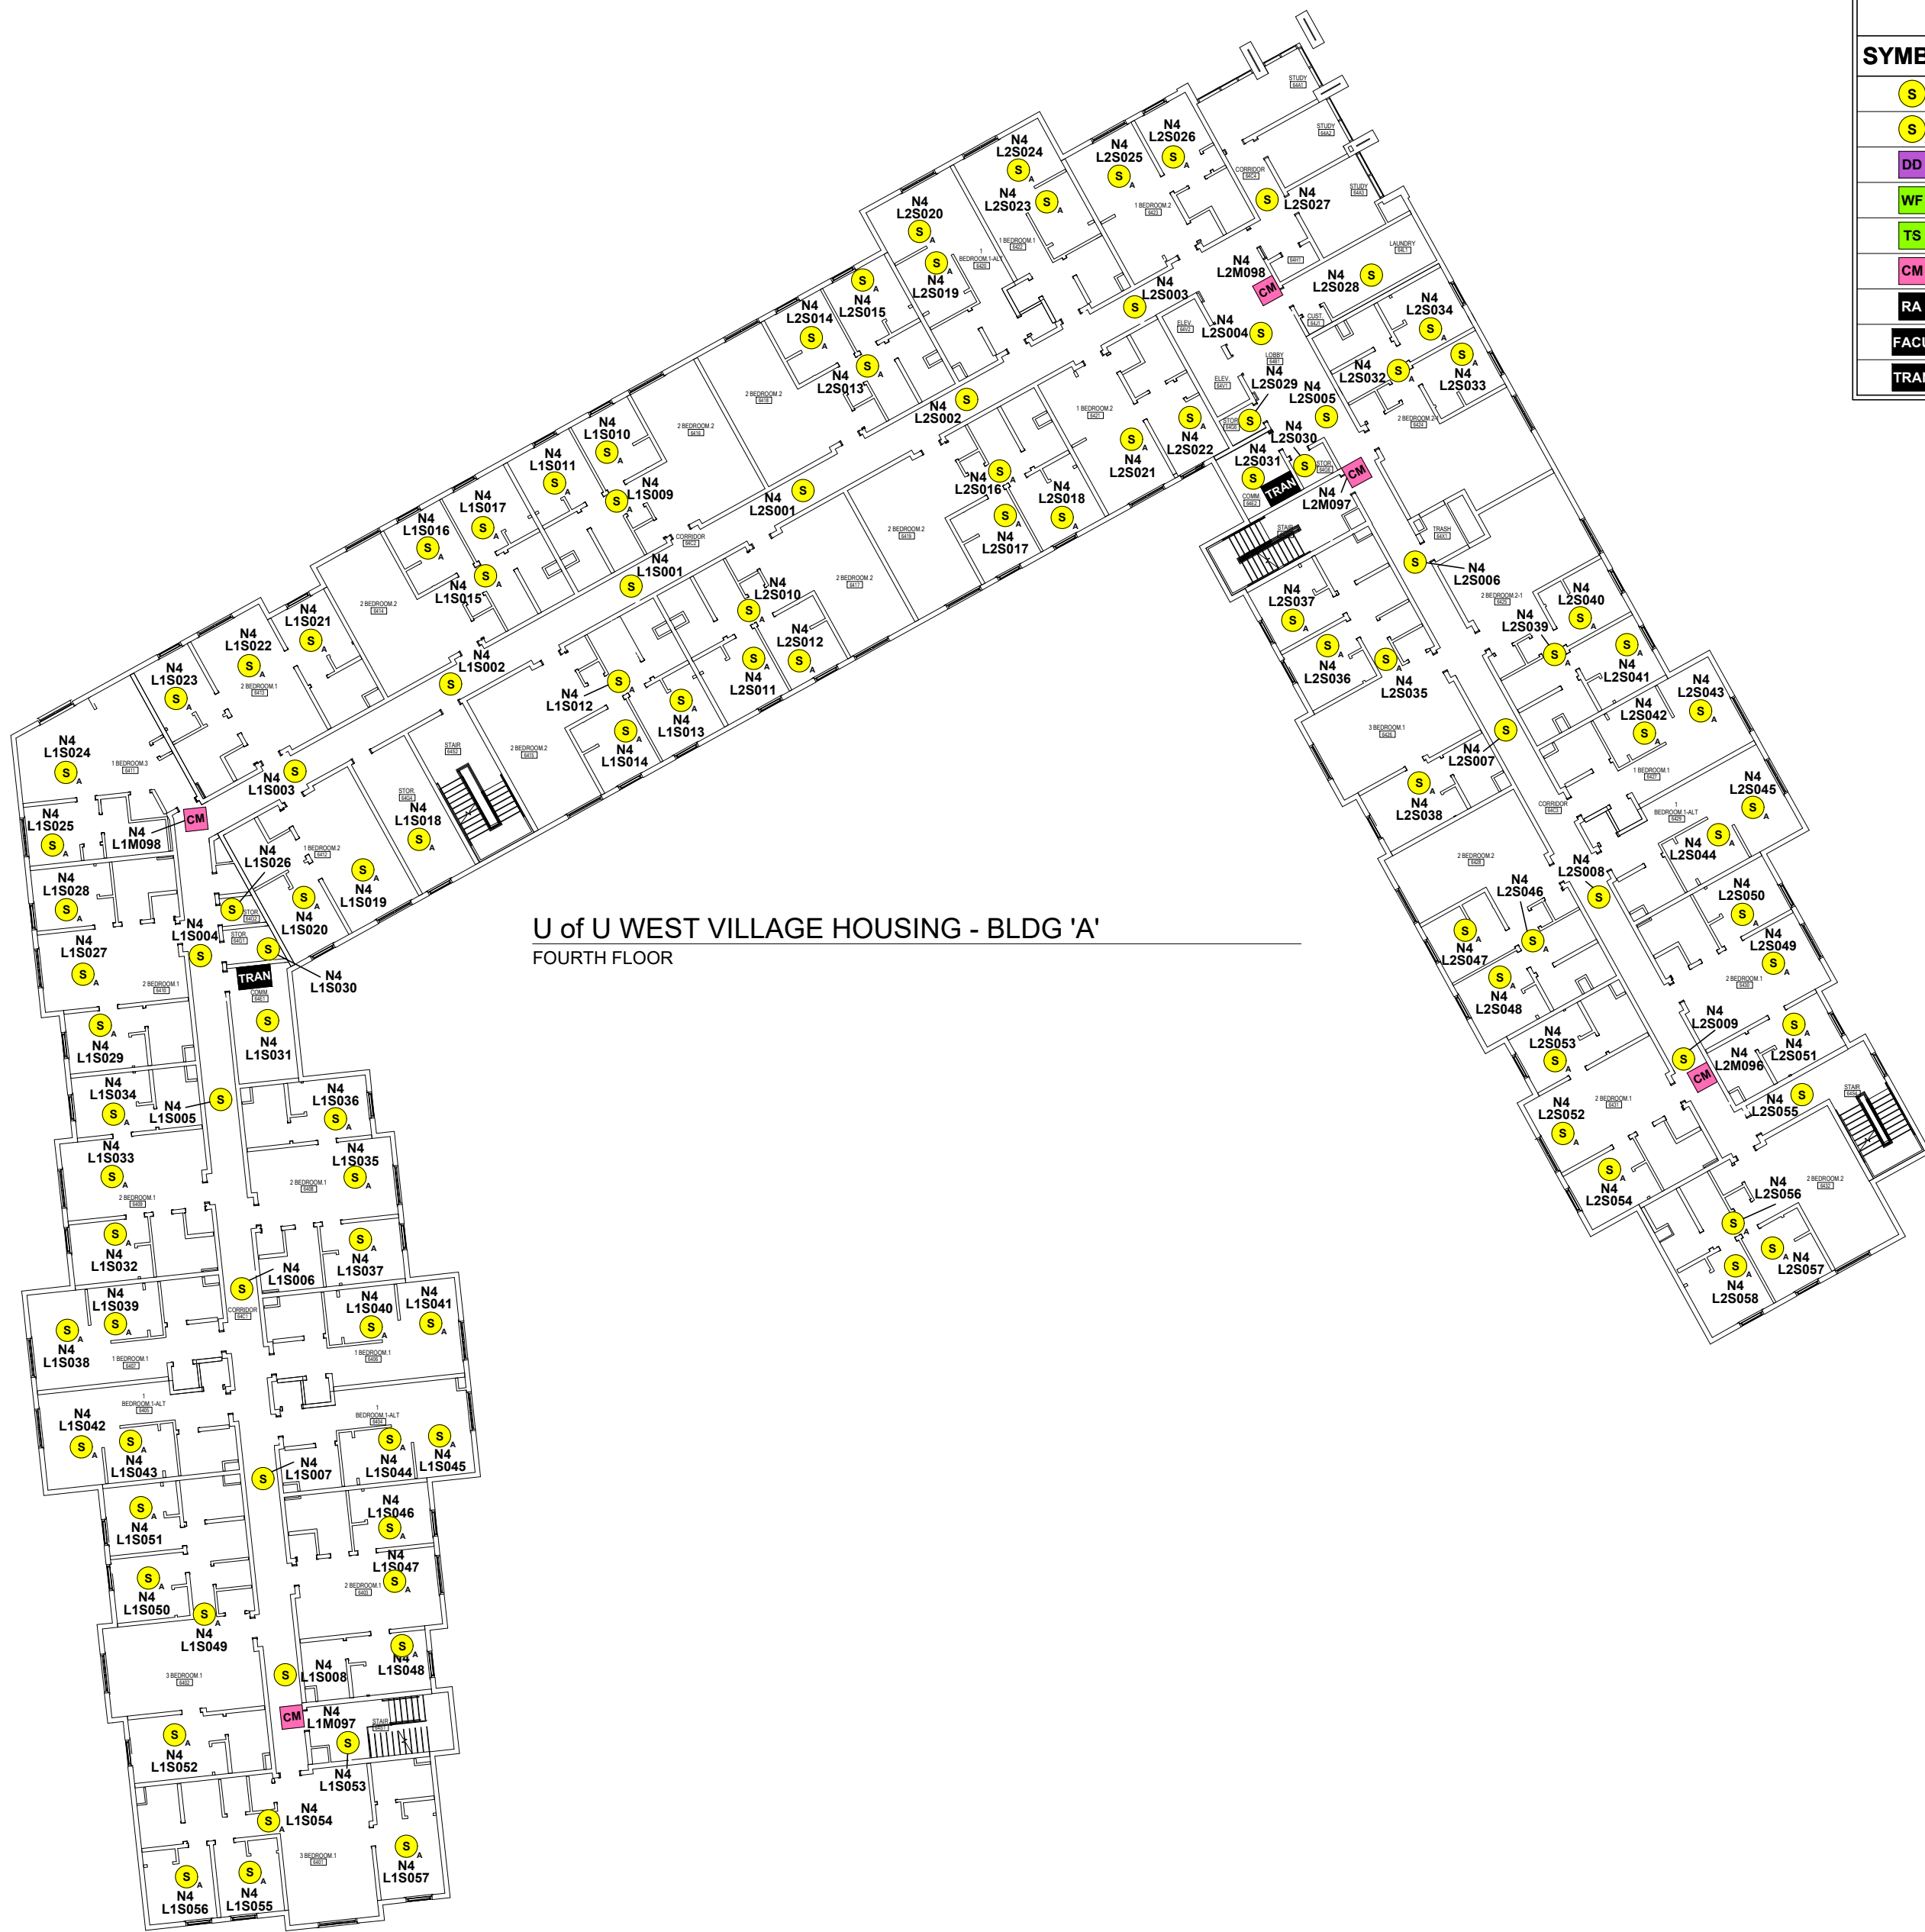

DEVICE LEGEND	
SYMBOL	DESCRIPTION
	SMOKE DETECTOR
	SMOKE DETECTOR- AUDIBLE BASE
	DUCT DETECTOR
	WATER FLOW SWITCH MODULE
	TAMPER SWITCH MODULE
	CONTROL MODULE
	REMOTE ANNUNCIATOR
	FIRE ALARM CONTROL UNIT
	TRANSPONDER PANEL

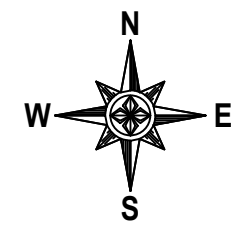

NOTE:
NFS DRAWINGS ARE BASED ON THE PROJECT ARCHITECTURE (A/E) PLANS AND SPECIFICATIONS FURNISHED TO NFS. A/E IS SOLELY RESPONSIBLE (NOT NFS) FOR THE TYPE, SIZE, LOCATION, AND SUITABILITY OF ALL FIRE ALARMS, CONTROL PANELS, AND OTHER DEVICES SHOWN ON THE A/E PLANS. NFS DRAWINGS ARE TO SHOW ONLY THE WIRING DIAGRAMS BETWEEN FIRE ALARM DEVICES AND CONTROL PANELS. NFS IS NOT RESPONSIBLE FOR THE INFORMATION SHOWN ON THE A/E PLANS.

WEST VILLAGE HOUSING - BUILDING 'A'
UNIVERSITY OF UTAH
SUNNYSIDE AVENUE AND FOOTHILL DRIVE
SALT LAKE CITY, UTAH 84108
FIRE ALARM SYSTEM

NFS
NELSON FIRE SYSTEMS
801-468-8300

DRAWN BY: BH
DESIGNED BY: XXXX
APPROVED BY: KK
DATE: 09/05/2023
SCALE: N.T.S.
PROJECT NO: XXXX
REVISION NO: XXXX
DRAWING NAME:
BUILDING A 4TH FLOOR FM.DWG

NELSON FIRE SYSTEMS
LEVEL 4

PAGE:
FINAL MAP



KEY PLAN

