



KEY PLAN

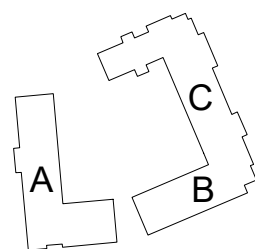

BLDG B



DEVICE LEGEND	
SYMBOL	DESCRIPTION
	SMOKE DETECTOR
	SMOKE DETECTOR- AUDIBLE BASE
	PULL STATION
	WATER FLOW SWITCH MODULE
	TAMPER SWITCH MODULE
	MONITOR MODULE
	CONTROL MODULE
	REMOTE ANNUNCIATOR
	ELEVATOR RECALL CABINET

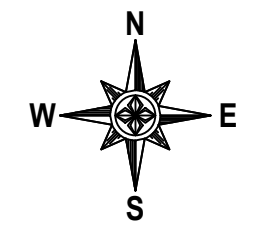

NOTE:
NFS DRAWINGS ARE BASED ON THE PROJECT ARCHITECTURE (A/E) PLANS AND SPECIFICATIONS FURNISHED TO NFS. A/E IS SOLELY RESPONSIBLE (NOT NFS) FOR THE TYPE, SIZE, LOCATION, AND SUITABILITY OF ALL FIRE ALARMS, CONTROL PANELS, AND OTHER DEVICES SHOWN ON THE A/E PLANS. NFS DRAWINGS ARE TO SHOW ONLY THE WIRING DIAGRAMS BETWEEN FIRE ALARM DEVICES AND CONTROL PANELS. NFS IS NOT RESPONSIBLE FOR THE INFORMATION SHOWN ON THE A/E PLANS.

UNIVERSITY OF UTAH
WEST VILLAGE HOUSING
BUILDING B
MAIN FLOOR
FIRE ALARM SYSTEM

NFS

NELSON FIRE SYSTEMS
801-468-8300


DRAWN BY: BH
DESIGNED BY: XXXX
APPROVED BY: KK
DATE: 09/05/2023
SCALE: N.T.S.
PROJECT NO: XXXX
REVISION NO: XXXX
DRAWING NAME:
BUILDING B LEVEL 1 FM.DWG

NELSON FIRE SYSTEMS
LEVEL 1

PAGE:
FINAL MAP



DEVICE LEGEND	
SYMBOL	DESCRIPTION
	SMOKE DETECTOR
	SMOKE DETECTOR- AUDIBLE BASE
	CONTROL MODULE
	FIRE ALARM CONTROL UNIT
	TRANSPONDER PANEL

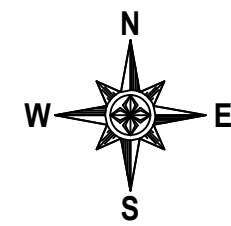

NOTE: DRAWINGS ARE BASED ON THE PROJECT ARCHITECTURE/ENGINEER (A/E) PLANS AND SPECIFICATIONS FURNISHED TO NFS. A/E IS SOLELY RESPONSIBLE (NOT NFS) FOR THE TYPE, SIZE, LOCATION, AND SUITABILITY OF ALL FIRE ALARMS, CONTROL PANELS, AND OTHER DEVICES SHOWN ON THE A/E PLANS. NFS DRAWINGS ARE TO SHOW ONLY THE WIRING DIAGRAMS BETWEEN FIRE ALARM DEVICES AND CONTROL PANELS. NFS IS NOT RESPONSIBLE FOR THE INFORMATION SHOWN ON THE A/E PLANS.



UNIVERSITY OF UTAH
WEST VILLAGE HOUSING
BUILDING B
SECOND FLOOR
FIRE ALARM SYSTEM

NFS
NELSON FIRE SYSTEMS
801-468-8300

DRAWN BY:	BH
DESIGNED BY:	XXXX
APPROVED BY:	KK
DATE:	09/05/2023
SCALE:	N.T.S.
PROJECT NO:	XXXX
REVISION NO:	XXXX
DRAWING NAME:	BUILDING B LEVEL 2 FM.DWG


NELSON FIRE SYSTEMS
LEVEL 2

PAGE:
FINAL MAP

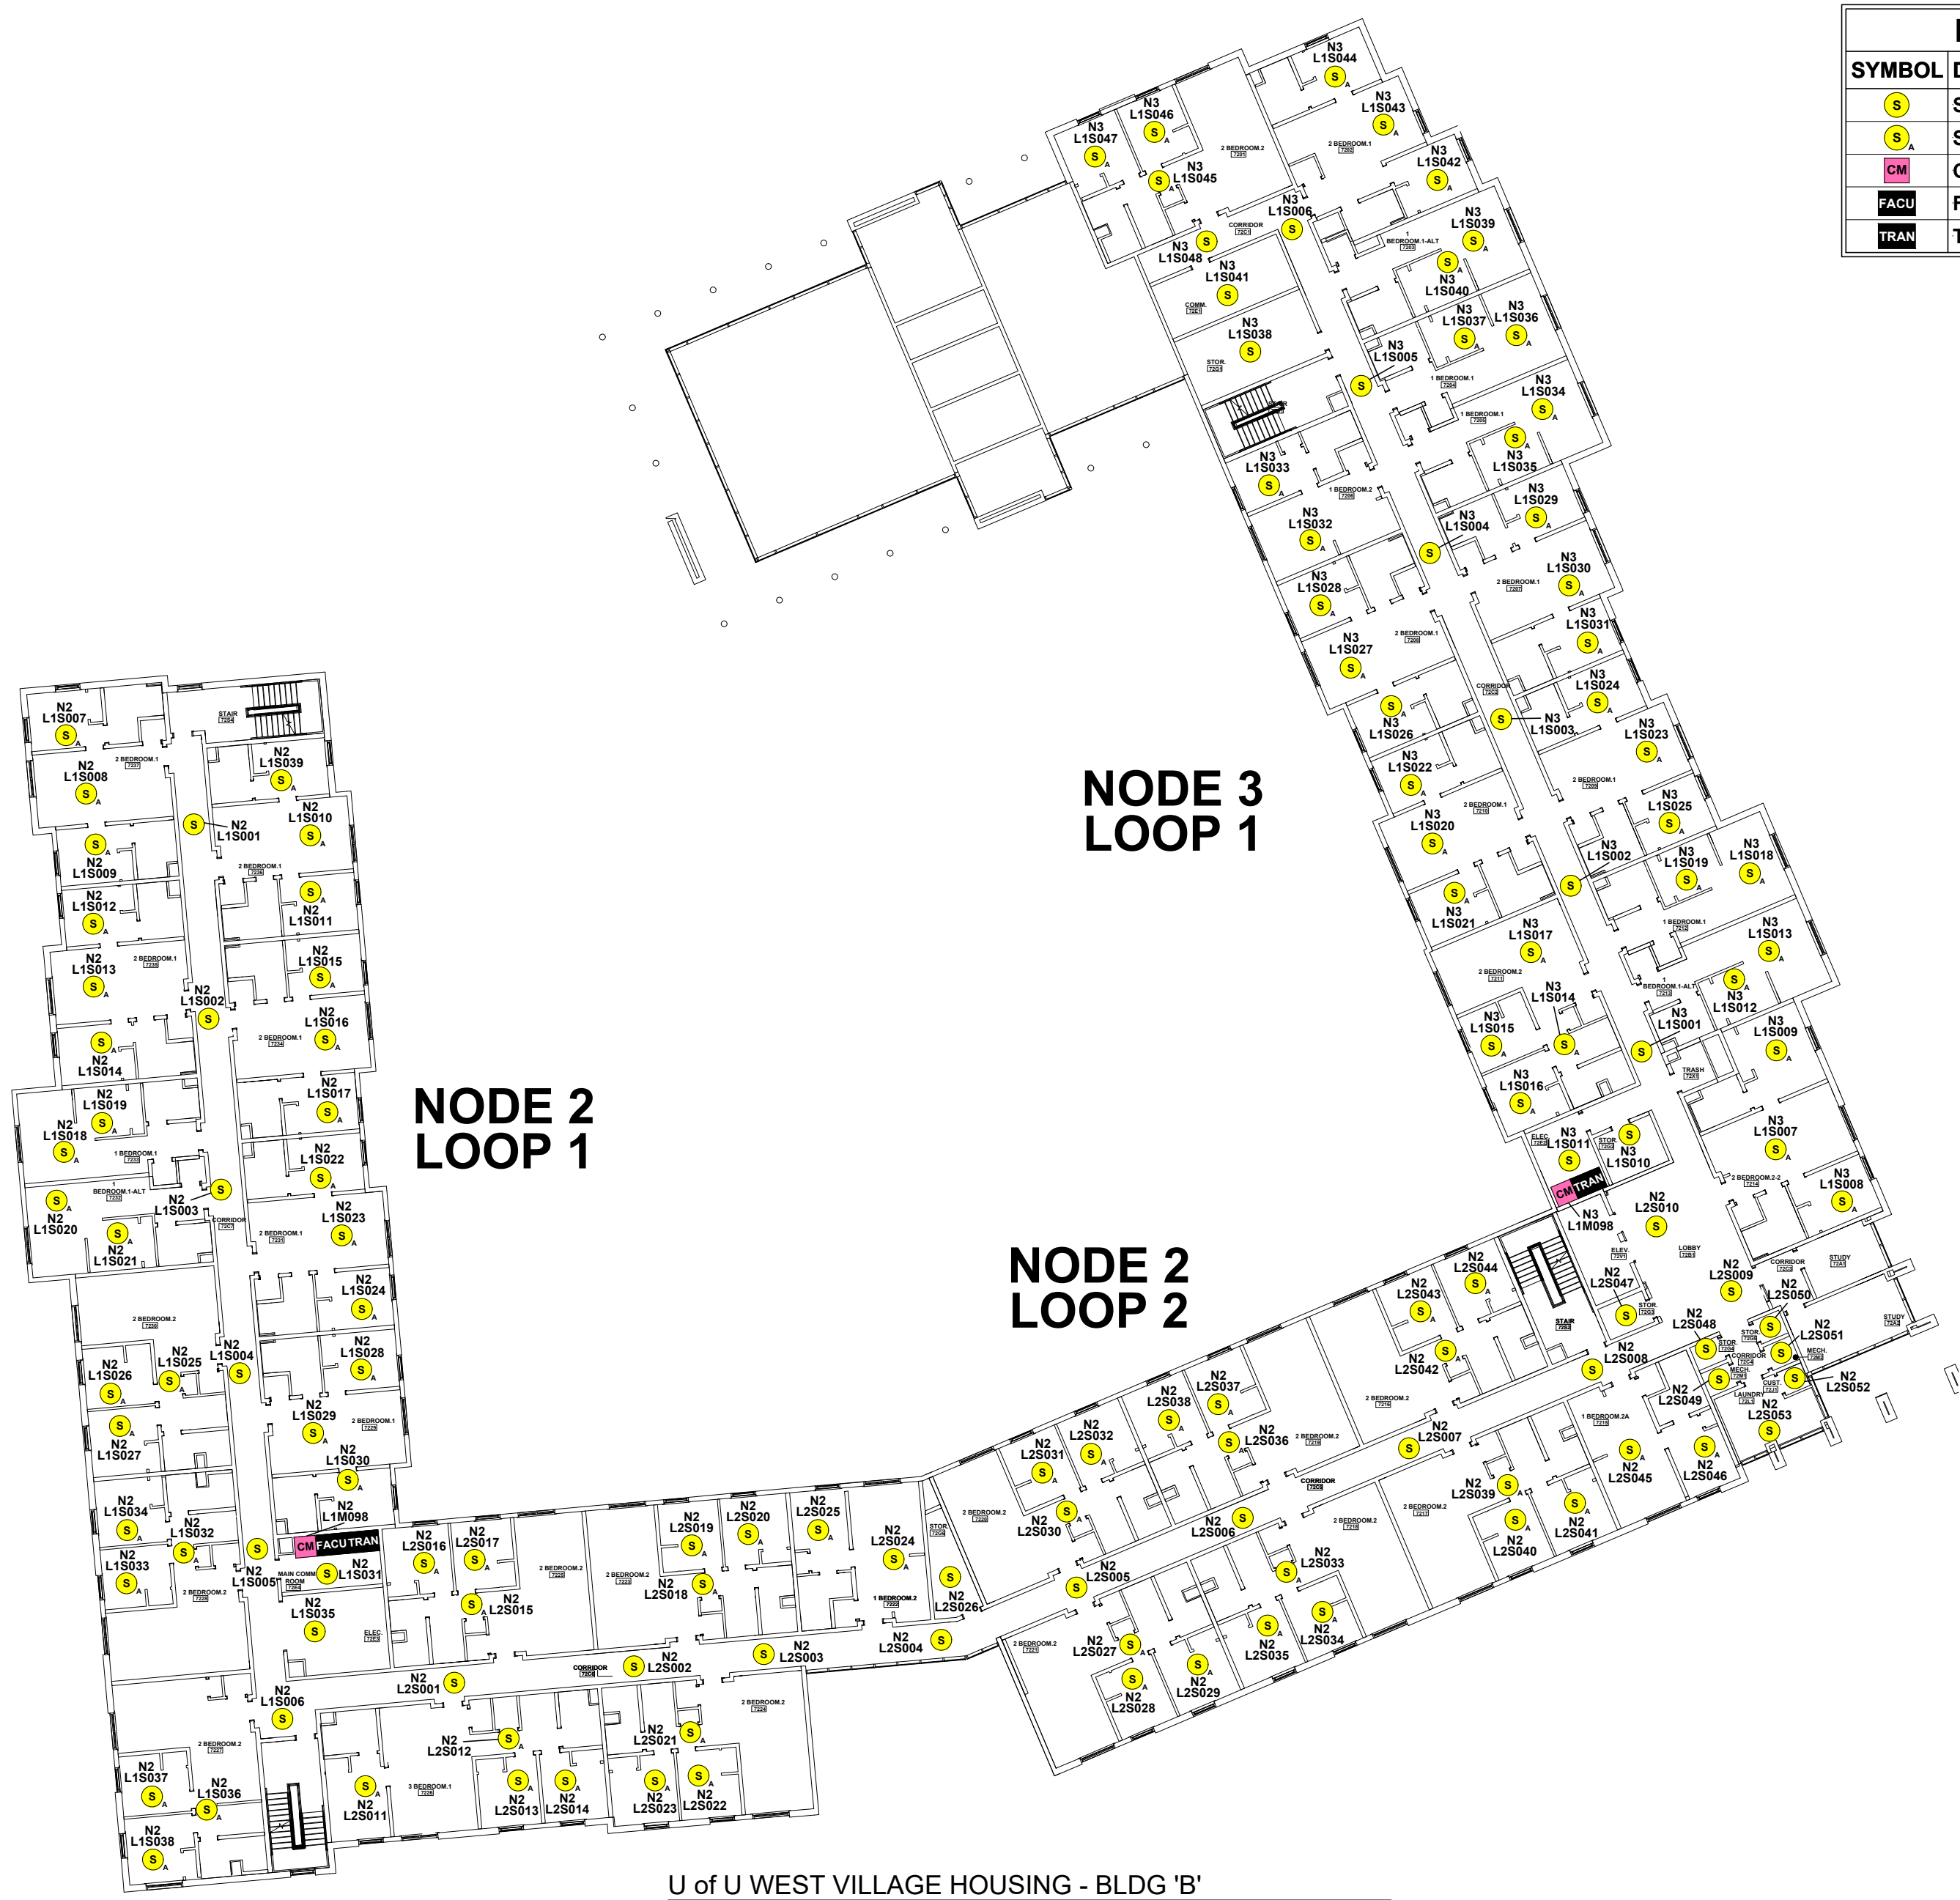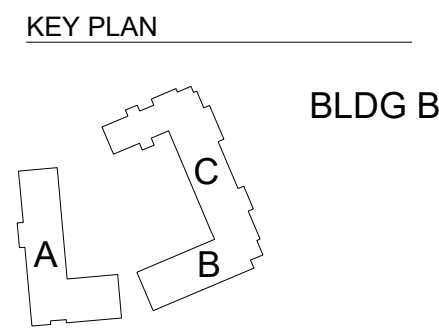

U of U WEST VILLAGE HOUSING - BLDG 'B'
SECOND FLOOR

DEVICE LEGEND	
SYMBOL	DESCRIPTION
	SMOKE DETECTOR
	SMOKE DETECTOR- AUDIBLE BASE
	CONTROL MODULE
	REMOTE ANNUNCIATOR
	FIRE ALARM CONTROL UNIT
	TRANSPONDER PANEL

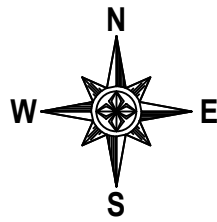

NOTE:
NFS DRAWINGS ARE BASED ON THE PROJECT ARCHITECTURE (A/E) PLANS AND SPECIFICATIONS FURNISHED TO NFS. A/E IS SOLELY RESPONSIBLE (NOT NFS) FOR THE TYPE, SIZE, LOCATION, AND SUITABILITY OF ALL FIRE ALARMS, CONTROL PANELS, AND OTHER DEVICES SHOWN ON THE A/E PLANS. NFS DRAWINGS ARE TO SHOW ONLY THE WIRING DIAGRAMS BETWEEN FIRE ALARM DEVICES AND CONTROL PANELS. NFS IS NOT RESPONSIBLE FOR THE INFORMATION SHOWN ON THE A/E PLANS.

UNIVERSITY OF UTAH
WEST VILLAGE HOUSING
BUILDING B
THIRD FLOOR
FIRE ALARM SYSTEM

NFS
NELSON FIRE SYSTEMS
801-468-8300


DRAWN BY: BH
DESIGNED BY: XXXX
APPROVED BY: KK
DATE: 09/05/2023
SCALE: N.T.S.
PROJECT NO: XXXX
REVISION NO: XXXX
DRAWING NAME:
BUILDING B LEVEL 3 FM.DWG

NELSON FIRE SYSTEMS
FLOORPLAN LEVEL


PAGE:
FINAL MAP



KEY PLAN

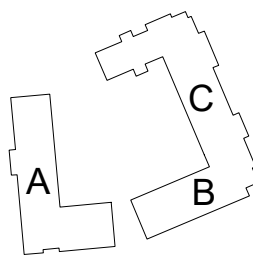


BLDG B

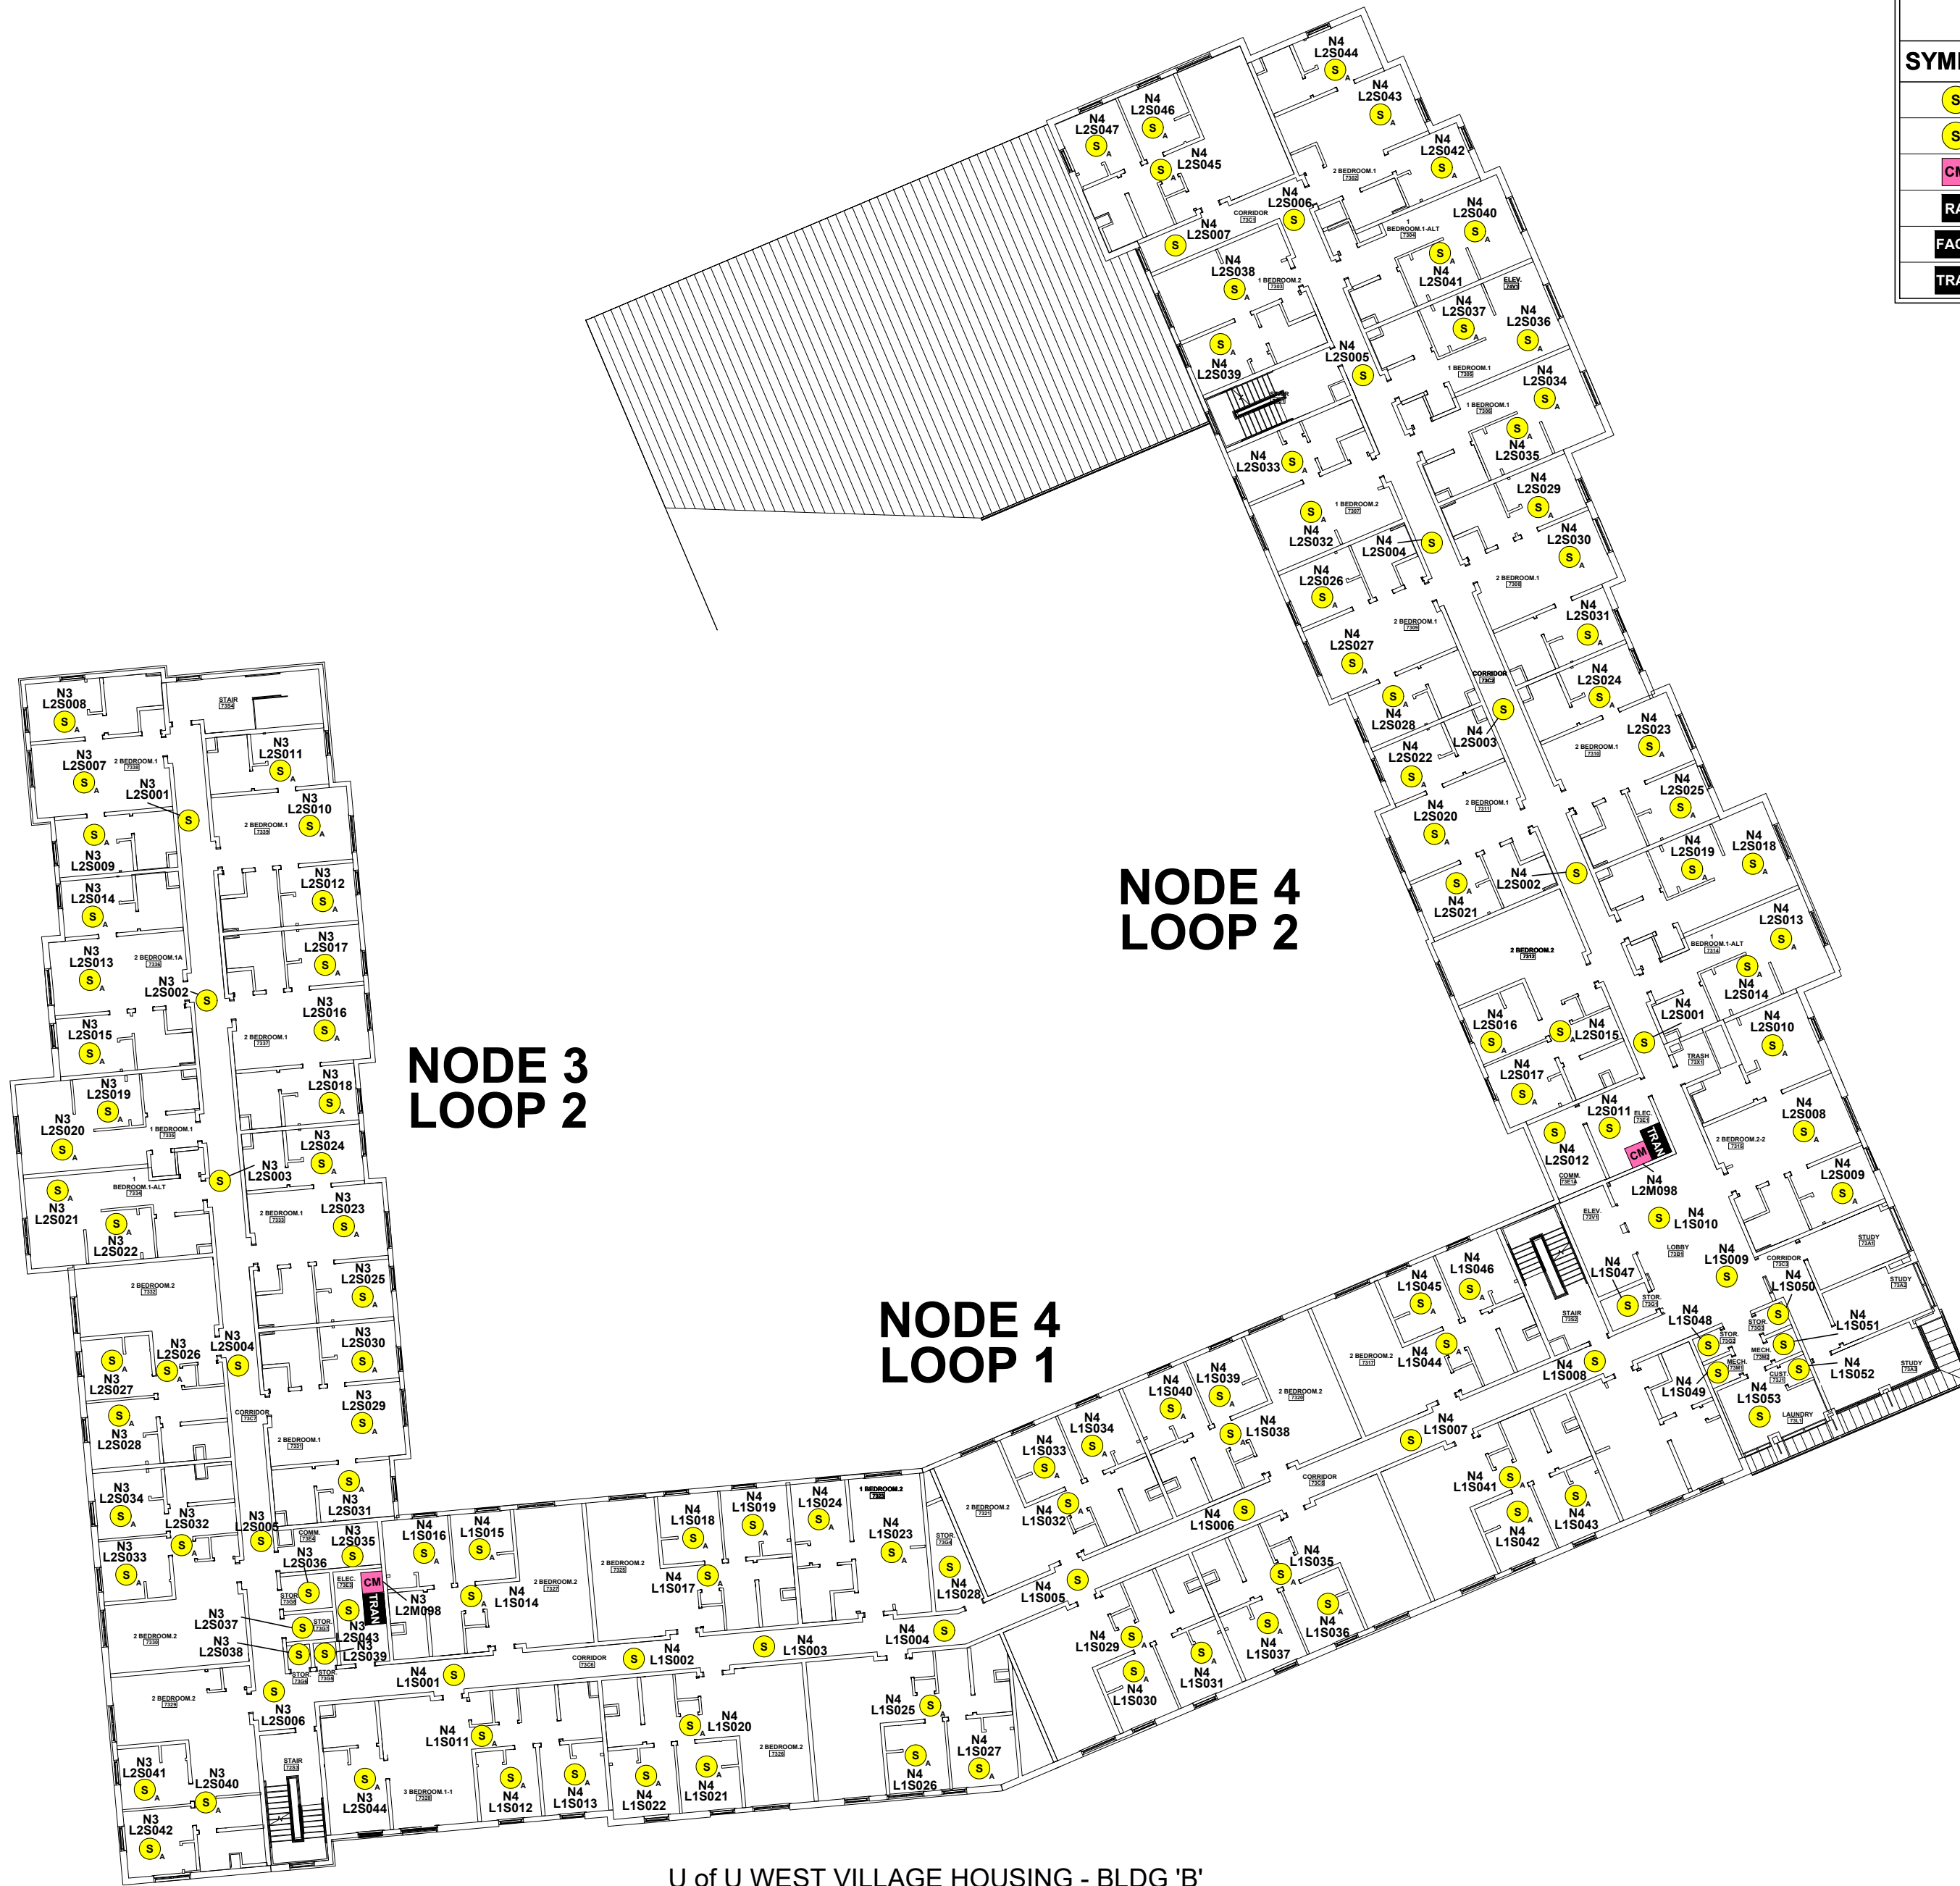

U of U WEST VILLAGE HOUSING - BLDG 'B'
THIRD FLOOR

KEY PLAN

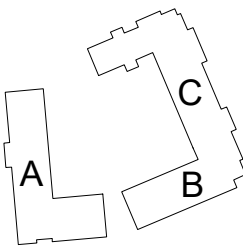


BLDG B



NODE 5
LOOP 1

NODE 5
LOOP 2

DEVICE LEGEND	
SYMBOL	DESCRIPTION
	SMOKE DETECTOR
	SMOKE DETECTOR- AUDIBLE BASE
	CONTROL MODULE
	TRANSPONDER PANEL

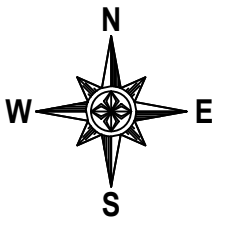

NOTE:
NFS DRAWINGS ARE BASED ON THE PROJECT ARCHITECTURE/ENGINEER (A/E) PLANS AND SPECIFICATIONS FURNISHED TO NFS. A/E IS SOLELY RESPONSIBLE (NOT NFS) FOR THE TYPE, SIZE, LOCATION, AND SUITABILITY OF ALL FIRE ALARMS, CONTROL PANELS, AND OTHER DEVICES SHOWN ON THE A/E PLANS. NFS DRAWINGS ARE TO SHOW ONLY THE WIRING DIAGRAMS BETWEEN FIRE ALARM DEVICES AND CONTROL PANELS. NFS IS NOT RESPONSIBLE FOR THE INFORMATION SHOWN ON THE A/E PLANS.

UNIVERSITY OF UTAH
WEST VILLAGE HOUSING
BUILDING B
FOURTH FLOOR
FIRE ALARM SYSTEM

NFS
NELSON FIRE SYSTEMS
801-468-8300

DRAWN BY: BH
DESIGNED BY: XXXX
APPROVED BY: KK
DATE: 09/05/2023
SCALE: N.T.S.
PROJECT NO: XXXX
REVISION NO: XXXX
DRAWING NAME:
BUILDING B LEVEL 4 FM.DWG

NELSON FIRE SYSTEMS
LEVEL 4

PAGE:
FINAL MAP

