

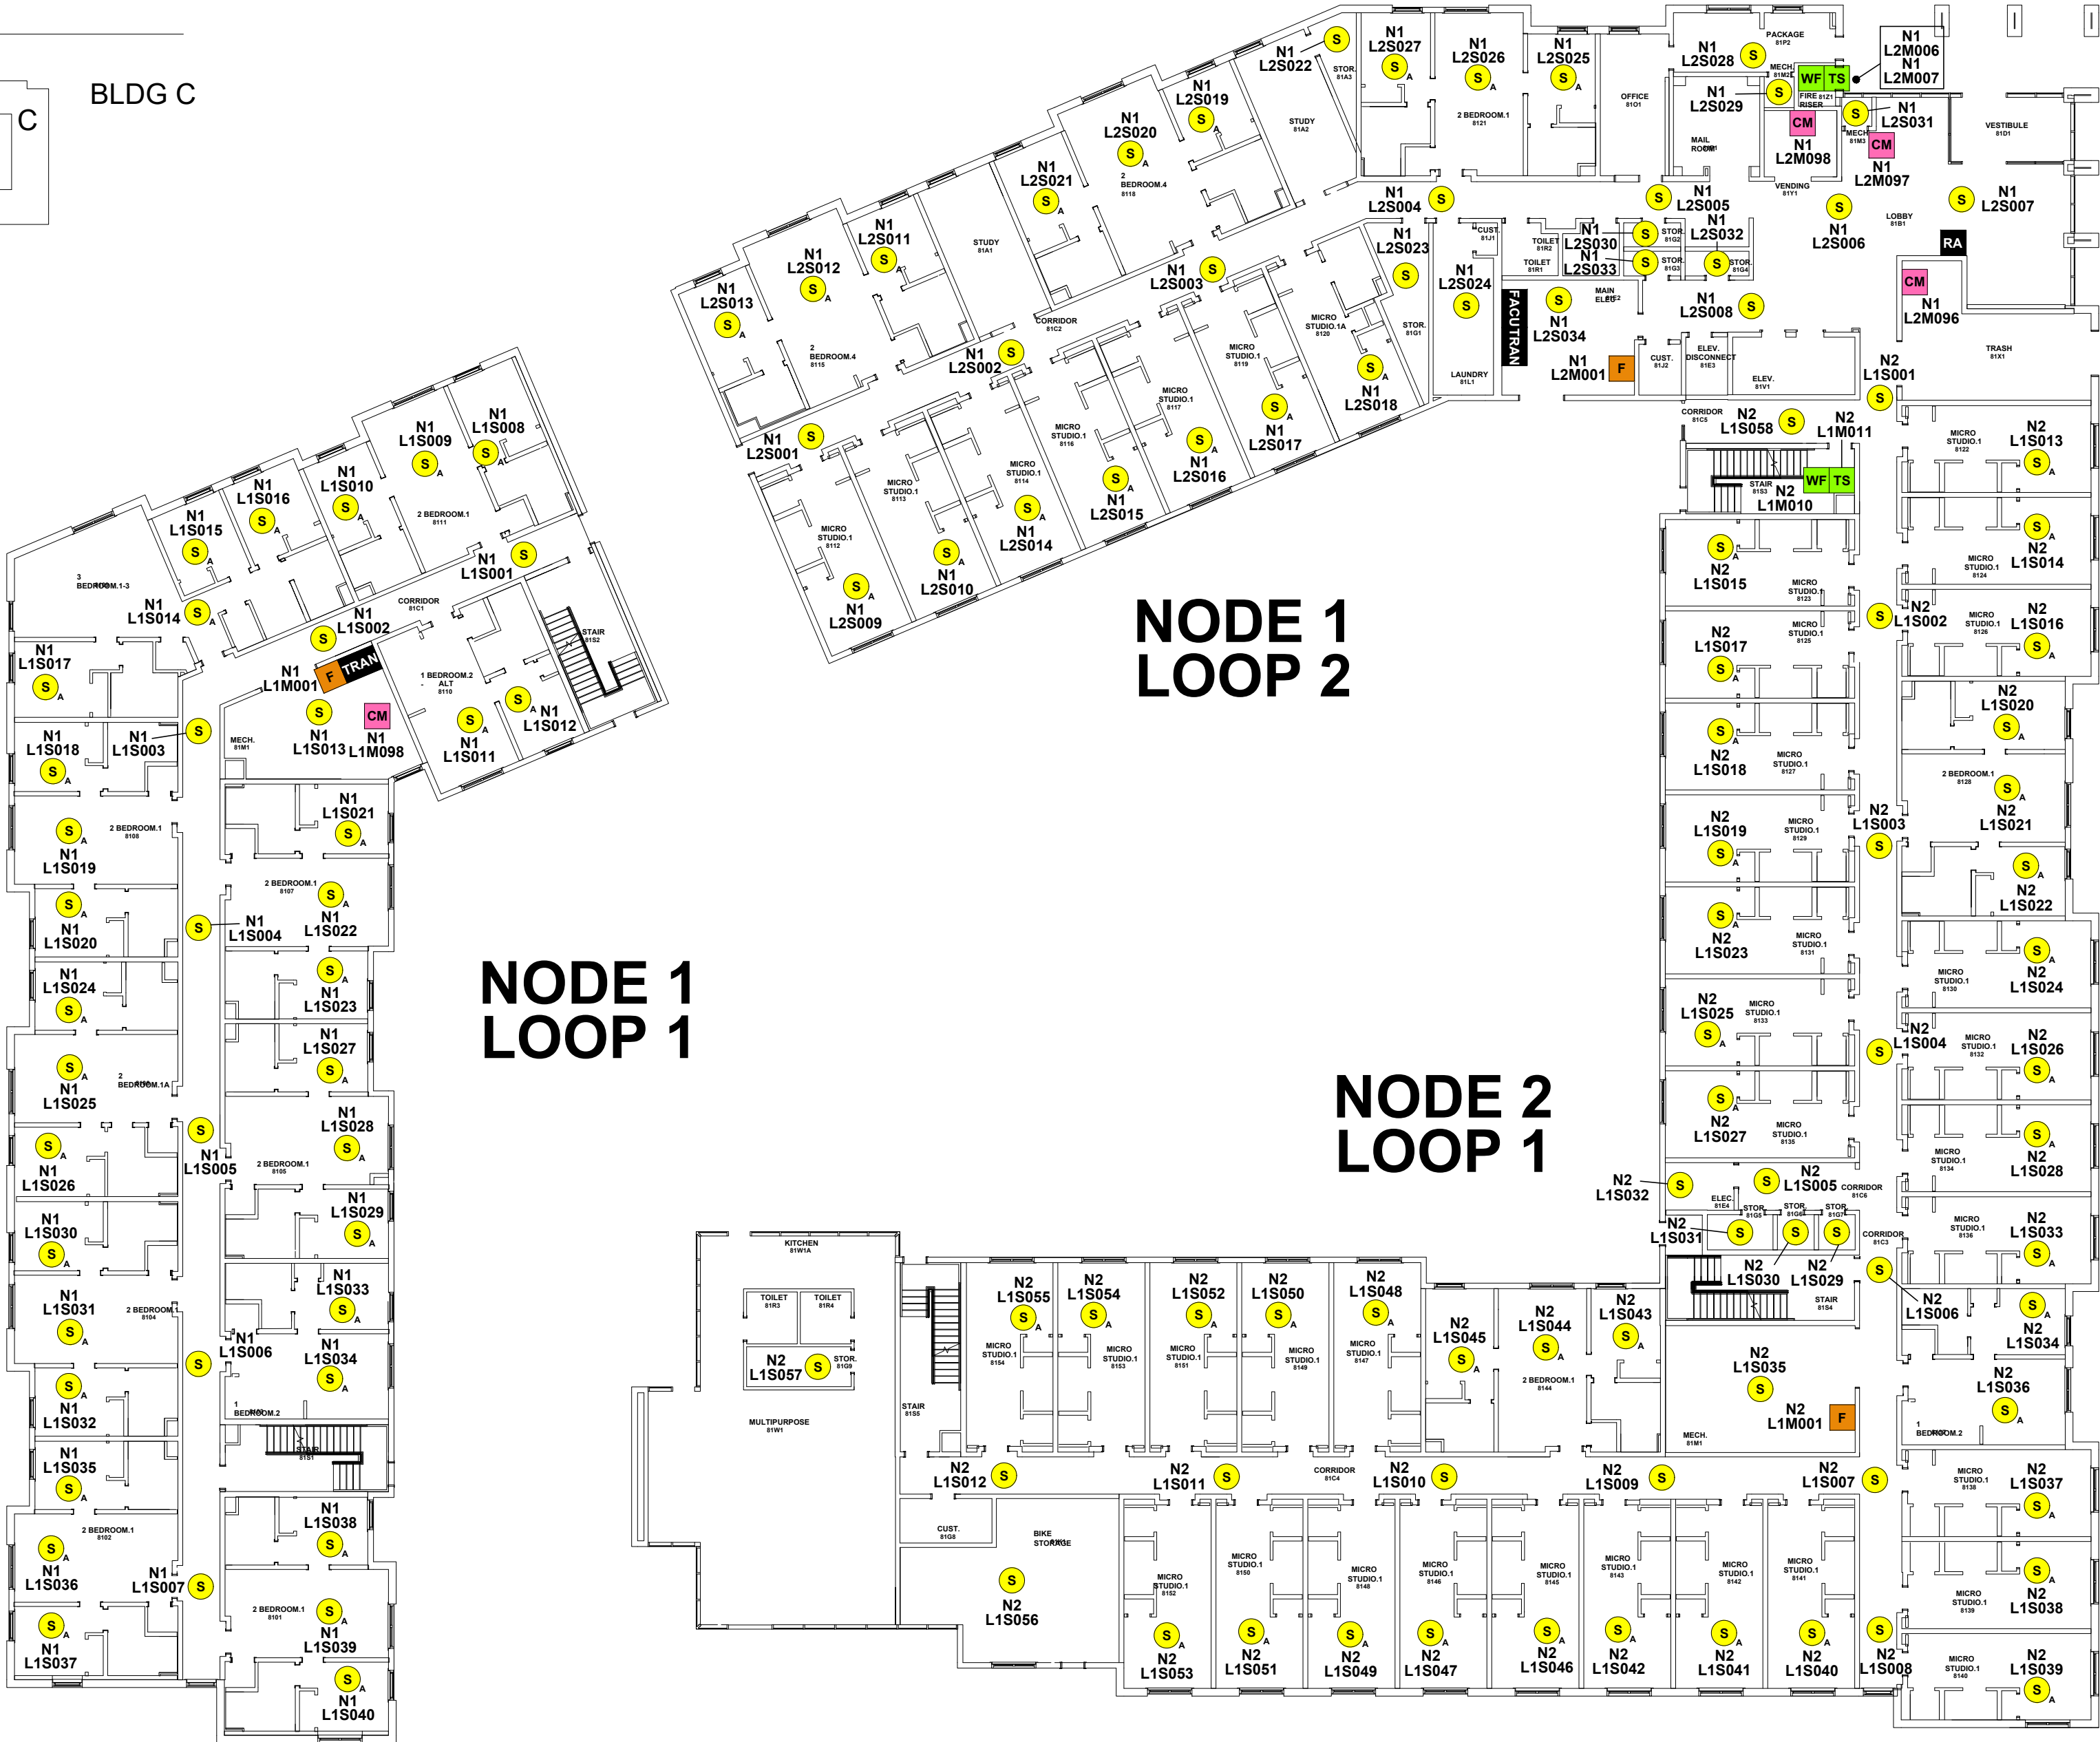


KEY PLAN

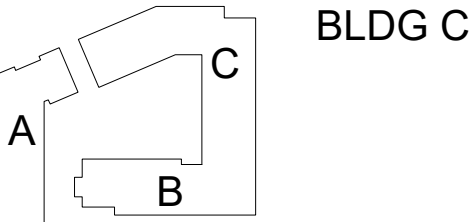

DEVICE LEGEND	
SYMBOL	DESCRIPTION
	SMOKE DETECTOR
	SMOKE DETECTOR- AUDIBLE BASE
	PULL STATION
	WATER FLOW SWITCH MODULE
	TAMPER SWITCH MODULE
	CONTROL MODULE
	REMOTE ANNUNCIATOR
	FIRE ALARM CONTROL UNIT
	TRANSPONDER PANEL

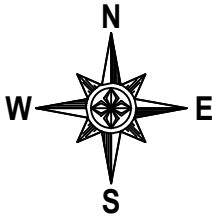

NOTE:
NFS DRAWINGS ARE BASED ON THE PROJECT ARCHITECTURE/ENGINEER (A/E) PLANS AND SPECIFICATIONS FURNISHED TO NFS. A/E IS SOLELY RESPONSIBLE (NOT NFS) FOR THE TYPE, SIZE, LOCATION, AND SUITABILITY OF ALL FIRE ALARMS, CONTROL PANELS, AND OTHER DEVICES SHOWN ON THE A/E PLANS. NFS DRAWINGS ARE TO SHOW ONLY THE WIRING DIAGRAMS BETWEEN FIRE ALARM DEVICES AND CONTROL PANELS. NFS IS NOT RESPONSIBLE FOR THE INFORMATION SHOWN ON THE A/E PLANS.

UNIVERSITY OF UTAH
WEST VILLAGE HOUSING
BUILDING C
FIRE ALARM SYSTEM

NFS
NELSON FIRE SYSTEMS
801-468-8300

DRAWN BY: BH
DESIGNED BY: XXXX
APPROVED BY: KK
DATE: 09/06/2023
SCALE: N.T.S.
PROJECT NO: XXXX
REVISION NO: XXXX
DRAWING NAME:
BUILDING C LEVEL 1 FM.DWG


NELSON FIRE SYSTEMS
LEVEL 1

PAGE:
FINAL MAP




U of U WEST VILLAGE HOUSING - BLDG 'C'
MAIN FLOOR


KEY PLAN

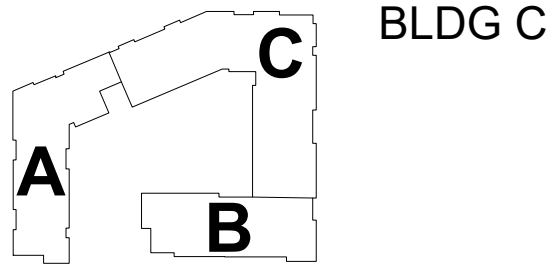

BLDG C

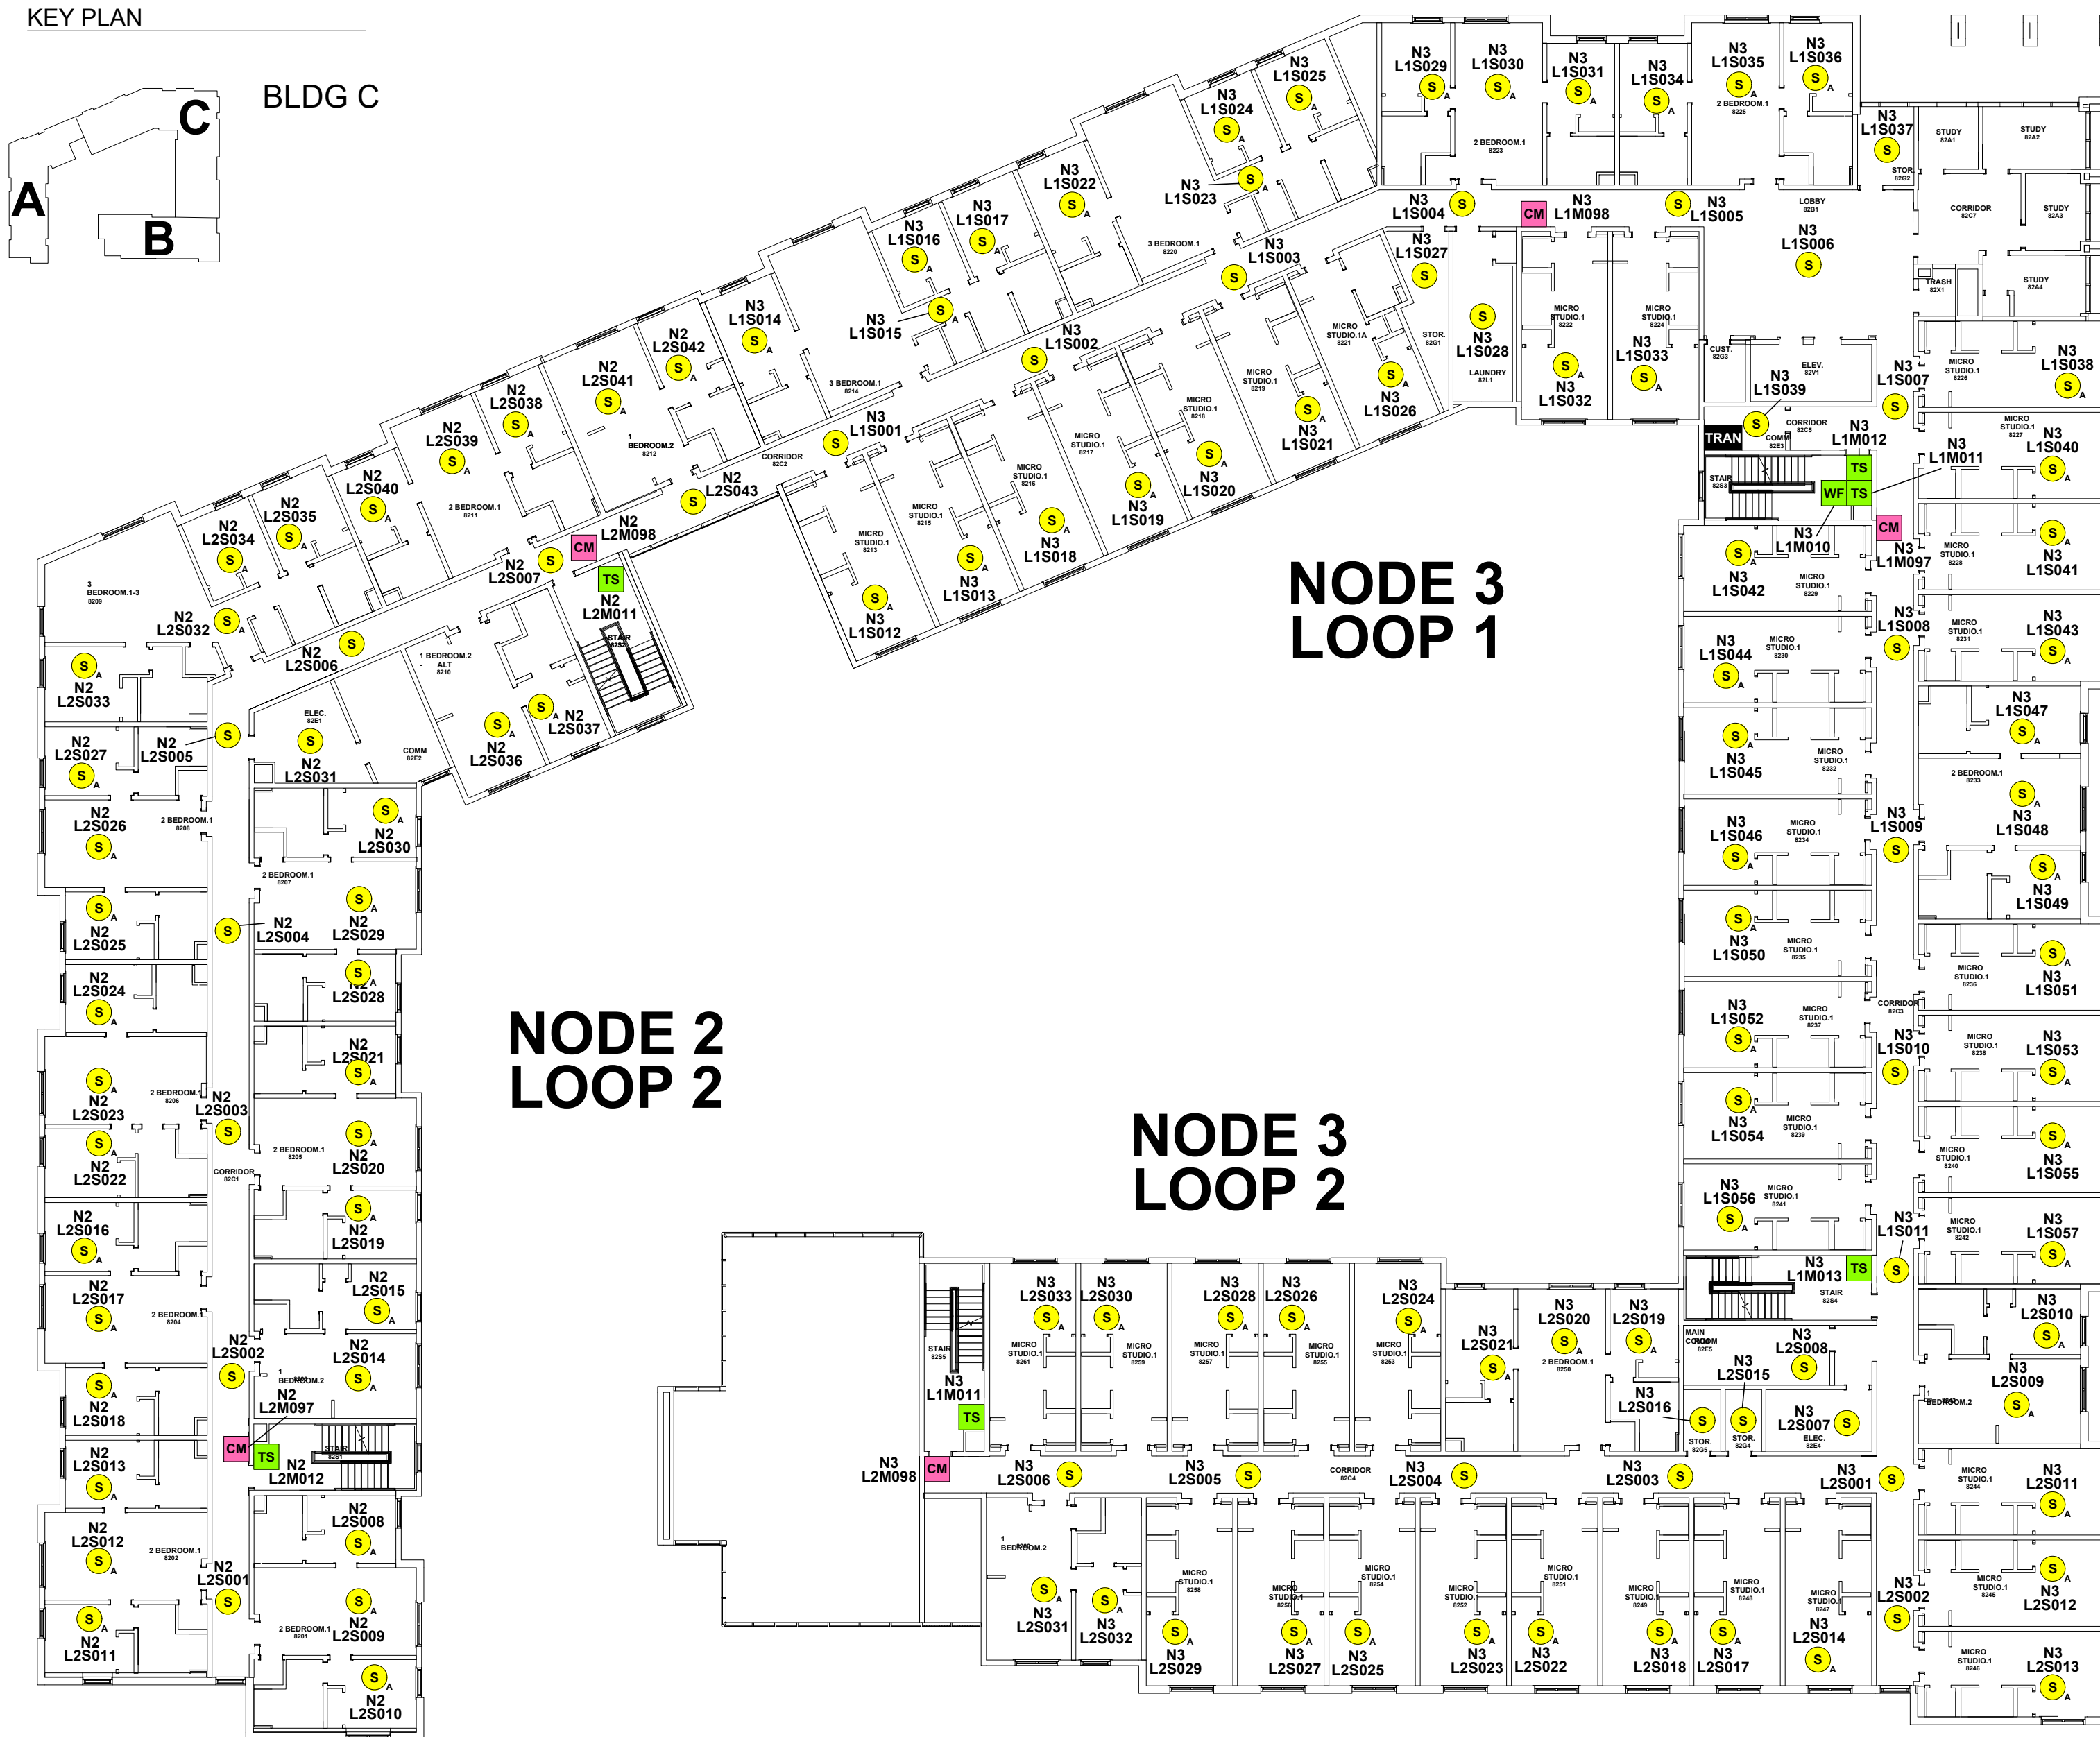

DEVICE LEGEND	
SYMBOL	DESCRIPTION
	SMOKE DETECTOR
	SMOKE DETECTOR- AUDIBLE BASE
	WATER FLOW SWITCH MODULE
	TAMPER SWITCH MODULE
	CONTROL MODULE
	TRANSPONDER PANEL

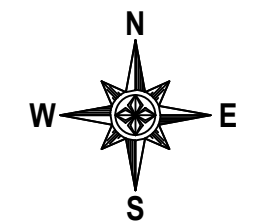

NOTE: ALL DRAWINGS ARE BASED ON THE PROJECT ARCHITECTURE (A/E) PLANS AND SPECIFICATIONS FURNISHED TO NFS. NFS IS SOLELY RESPONSIBLE (NOT NFS) FOR THE TYPE, SIZE, LOCATION, AND SUITABILITY OF ALL FIRE ALARMS, CONTROL PANELS, AND OTHER DEVICES SHOWN ON THE A/E PLANS. NFS DRAWINGS ARE TO SHOW ONLY THE WIRING DIAGRAMS BETWEEN FIRE ALARM DEVICES AND CONTROL PANELS. NFS IS NOT RESPONSIBLE FOR THE INFORMATION SHOWN ON THE A/E PLANS.

UNIVERSITY OF UTAH
WEST VILLAGE HOUSING
BUILDING C
FIRE ALARM SYSTEM

NFS
NELSON FIRE SYSTEMS
801-468-8300

DRAWN BY: BH
DESIGNED BY: XXXX
APPROVED BY: KK
DATE: 09/06/2023
SCALE: N.T.S.
PROJECT NO: XXXX
REVISION NO: XXXX
DRAWING NAME:
BUILDING C LEVEL 2 FM.DWG

NELSON FIRE SYSTEMS
LEVEL 2

PAGE:
FINAL MAP

U of U WEST VILLAGE HOUSING - BLDG 'C'
SECOND FLOOR




NODE 4 LOOP 1

NODE 4 LOOP 2

NODE 5
LOOP 1

SYMBOL	DESCRIPTION
	SMOKE DETECTOR
	SMOKE DETECTOR- AUDIBLE BASE
	PULL STATION
	WATER FLOW SWITCH MODULE
	TAMPER SWITCH MODULE
	CONTROL MODULE
	TRANSPONDER PANEL

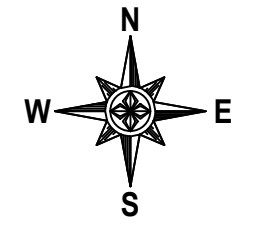

NOTE:
NFS DRAWINGS ARE BASED ON THE PROJECT
ARCHITECTURE/ENGINEER (A/E) PLANS AND
SPECIFICATIONS FURNISHED TO NFS. A/E IS SOLELY
RESPONSIBLE (NOT NFS) FOR THE TYPE, SIZE, RGS,
LOCATION AND SUITABILITY OF ALL FIRE ALARMS,
CONTROL PANELS, AND OTHER DEVICES SHOWN ON
THE A/E PLANS. NFS DRAWINGS ARE TO SHOW ONLY
THE WIRING DIAGRAMS BETWEEN FIRE ALARM
DEVICES AND CONTROL PANELS. NFS IS NOT
RESPONSIBLE FOR THE INFORMATION SHOWN ON THE
A/E PLANS.

UNIVERSITY OF UTAH
WEST VILLAGE HOUSING
BUILDING C
FIRE ALARM SYSTEM

NFS

NELSON FIRE SYSTEMS
801-468-8300

DRAWN BY:	BH
DESIGNED BY:	XXXX
APPROVED BY:	KK
DATE:	09/06/2023
SCALE:	N.T.S.
PROJECT NO:	XXXX
REVISION NO:	XXXX
DRAWING NAME:	
BUILDING C LEVEL 3 FM.DWG	

NELSON FIRE SYSTEMS


FLOORPLAN LEVEL

PAGE:

FINAL MAP




KEY PLAN

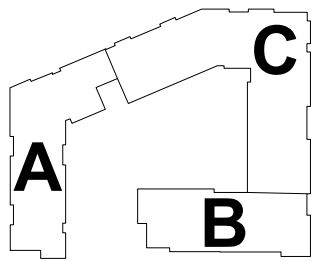


BLDG C

NODE 5
LOOP 2

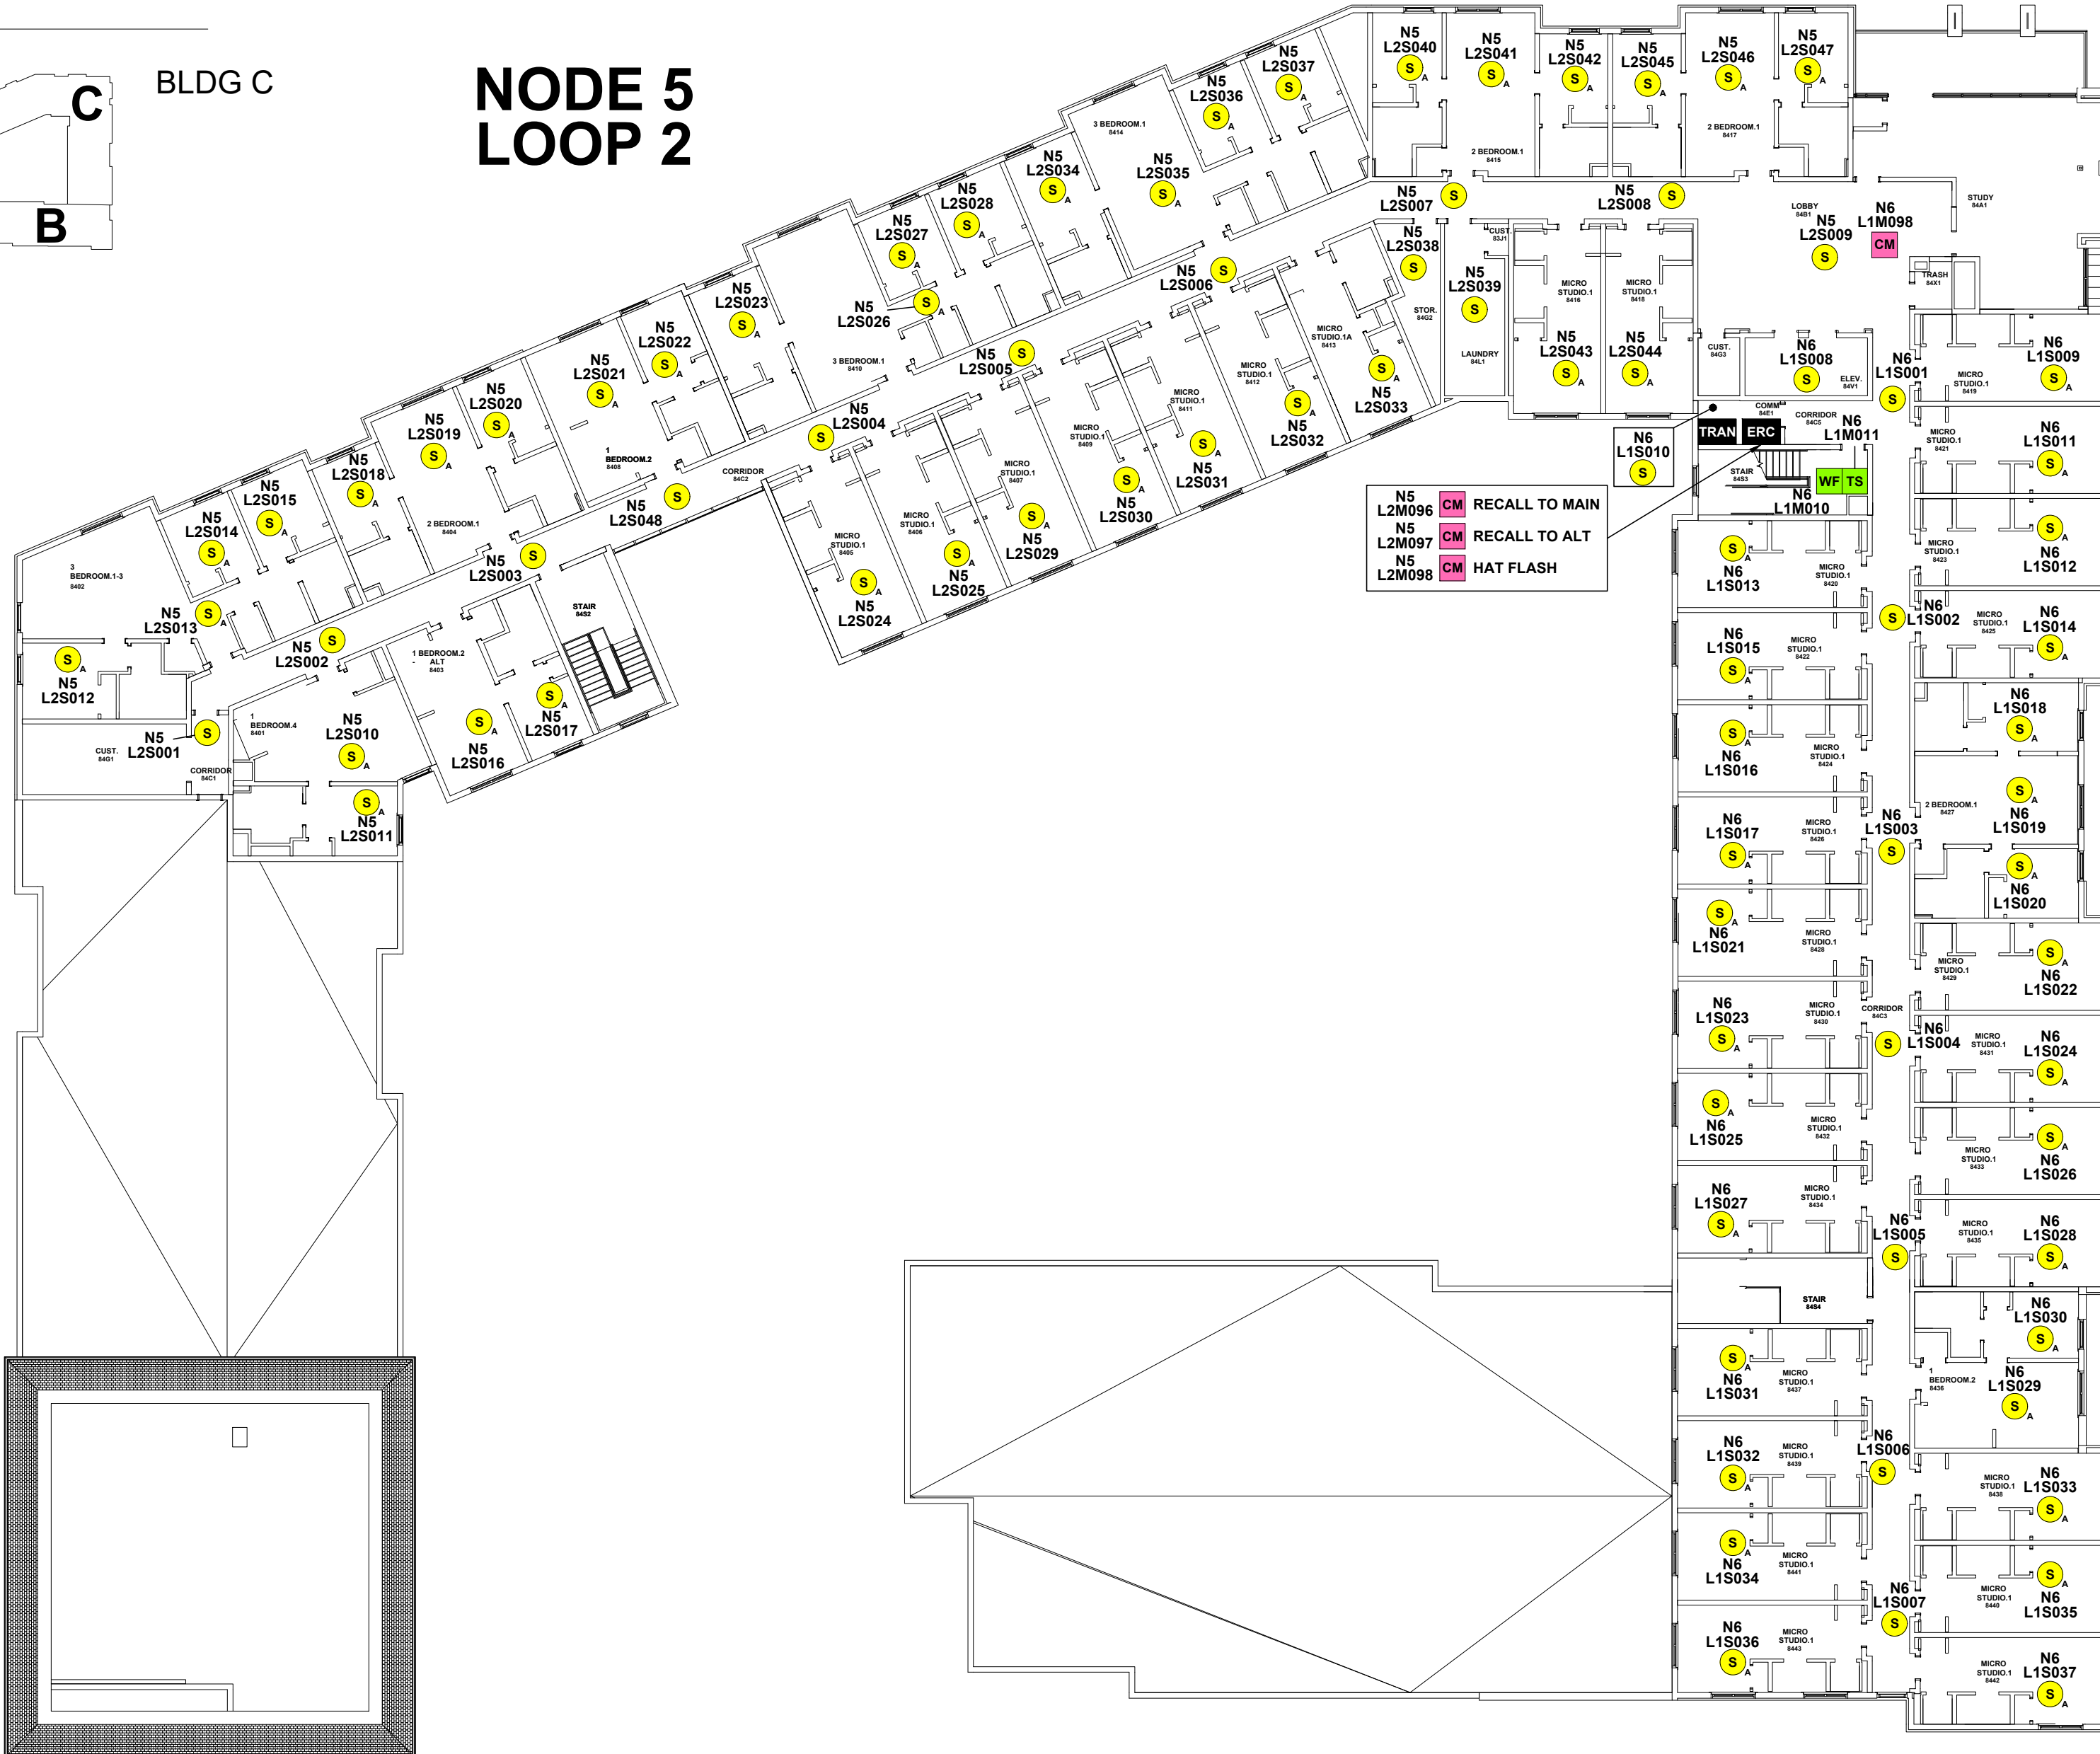

DEVICE LEGEND	
SYMBOL	DESCRIPTION
	SMOKE DETECTOR
	SMOKE DETECTOR- AUDIBLE BASE
	WATER FLOW SWITCH MODULE
	TAMPER SWITCH MODULE
	CONTROL MODULE
	TRANSPONDER PANEL
	ELEVATOR RECALL CABINET

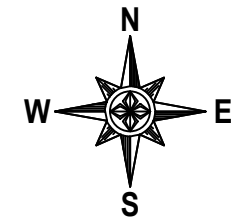

NOTE:
NFS DRAWINGS ARE BASED ON THE PROJECT ARCHITECTURE/ENGINEER (A/E) PLANS AND SPECIFICATIONS FURNISHED TO NFS. A/E IS SOLELY RESPONSIBLE (NOT NFS) FOR THE TYPE, SIZE, LOCATION, AND SUITABILITY OF ALL FIRE ALARMS, CONTROL PANELS, AND OTHER DEVICES SHOWN ON THE A/E PLANS. NFS DRAWINGS ARE TO SHOW ONLY THE WIRING DIAGRAMS BETWEEN FIRE ALARM DEVICES AND CONTROL PANELS. NFS IS NOT RESPONSIBLE FOR THE INFORMATION SHOWN ON THE A/E PLANS.

UNIVERSITY OF UTAH
WEST VILLAGE HOUSING
BUILDING C
FIRE ALARM SYSTEM

NODE 6
LOOP 1

NFS

NELSON FIRE SYSTEMS
801-468-8300

DRAWN BY: BH
DESIGNED BY: XXXX
APPROVED BY: KK
DATE: 09/06/2023
SCALE: N.T.S.
PROJECT NO: XXXX
REVISION NO: XXXX
DRAWING NAME:
BUILDING C LEVEL 4 FM.DWG

NELSON FIRE SYSTEMS
FLOORPLAN LEVEL

PAGE:
FINAL MAP

U of U WEST VILLAGE HOUSING - BLDG 'C'
FOURTH FLOOR

