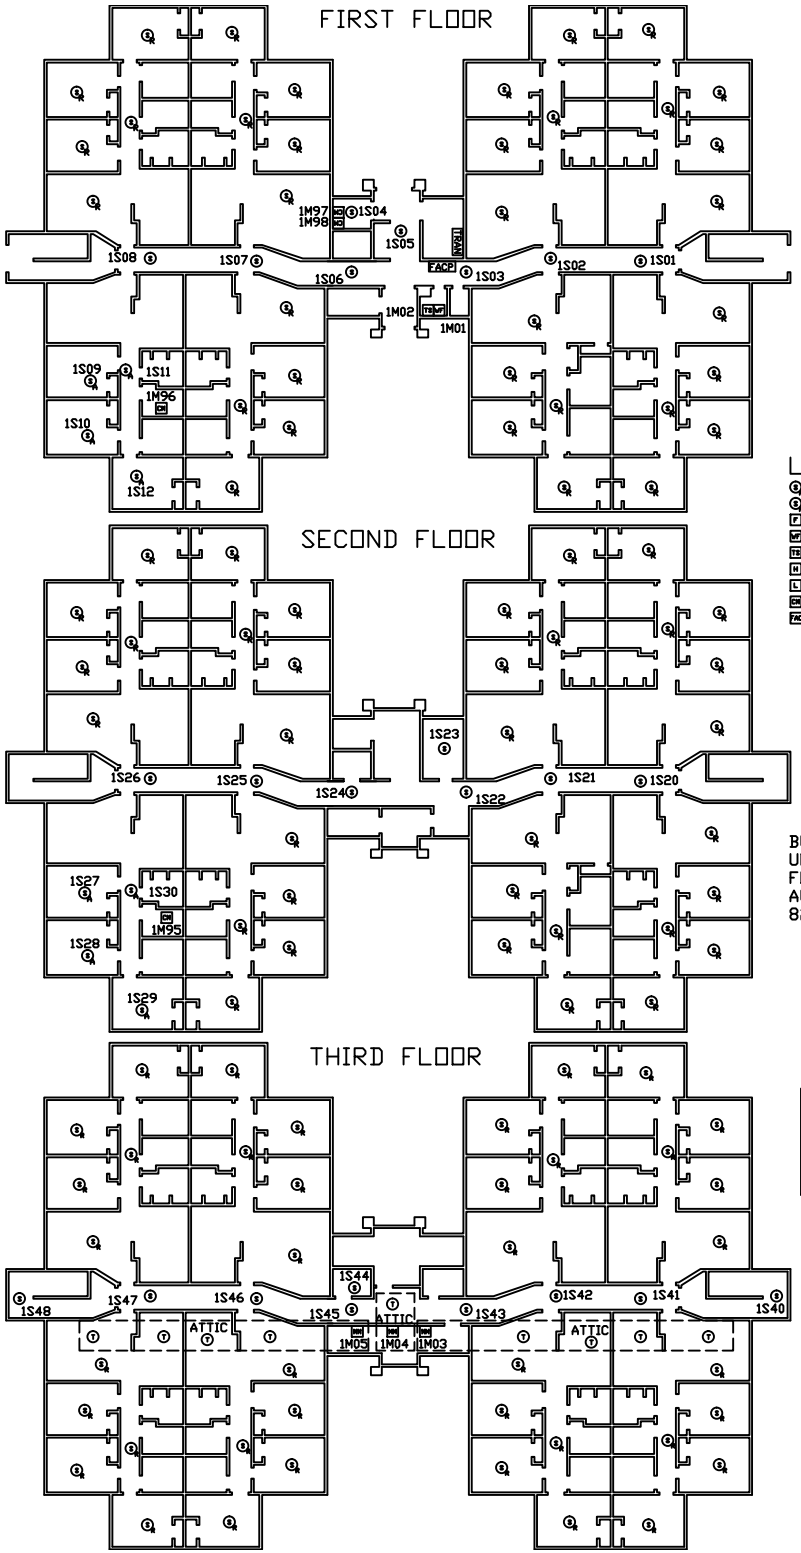

LEGEND

- AUDIBLE SMOKE DETECTOR
- RESIDENTIAL SMOKE DETECTOR
- MANUAL PULL STATION
- WATERFLOW SWITCH
- TAMPER SWITCH
- STROBE/HORN
- STROBE
- CONTROL MODULE
- FIRE ALARM CONTROL PANEL

BUILDING 827
UNIVERSITY OF UTAH
FORT DOUGLAS STUDENT HOUSING
AUGUST 31, 1999
827.DWG

NFS
NELSON FIRE SYSTEMS
801-288-9905