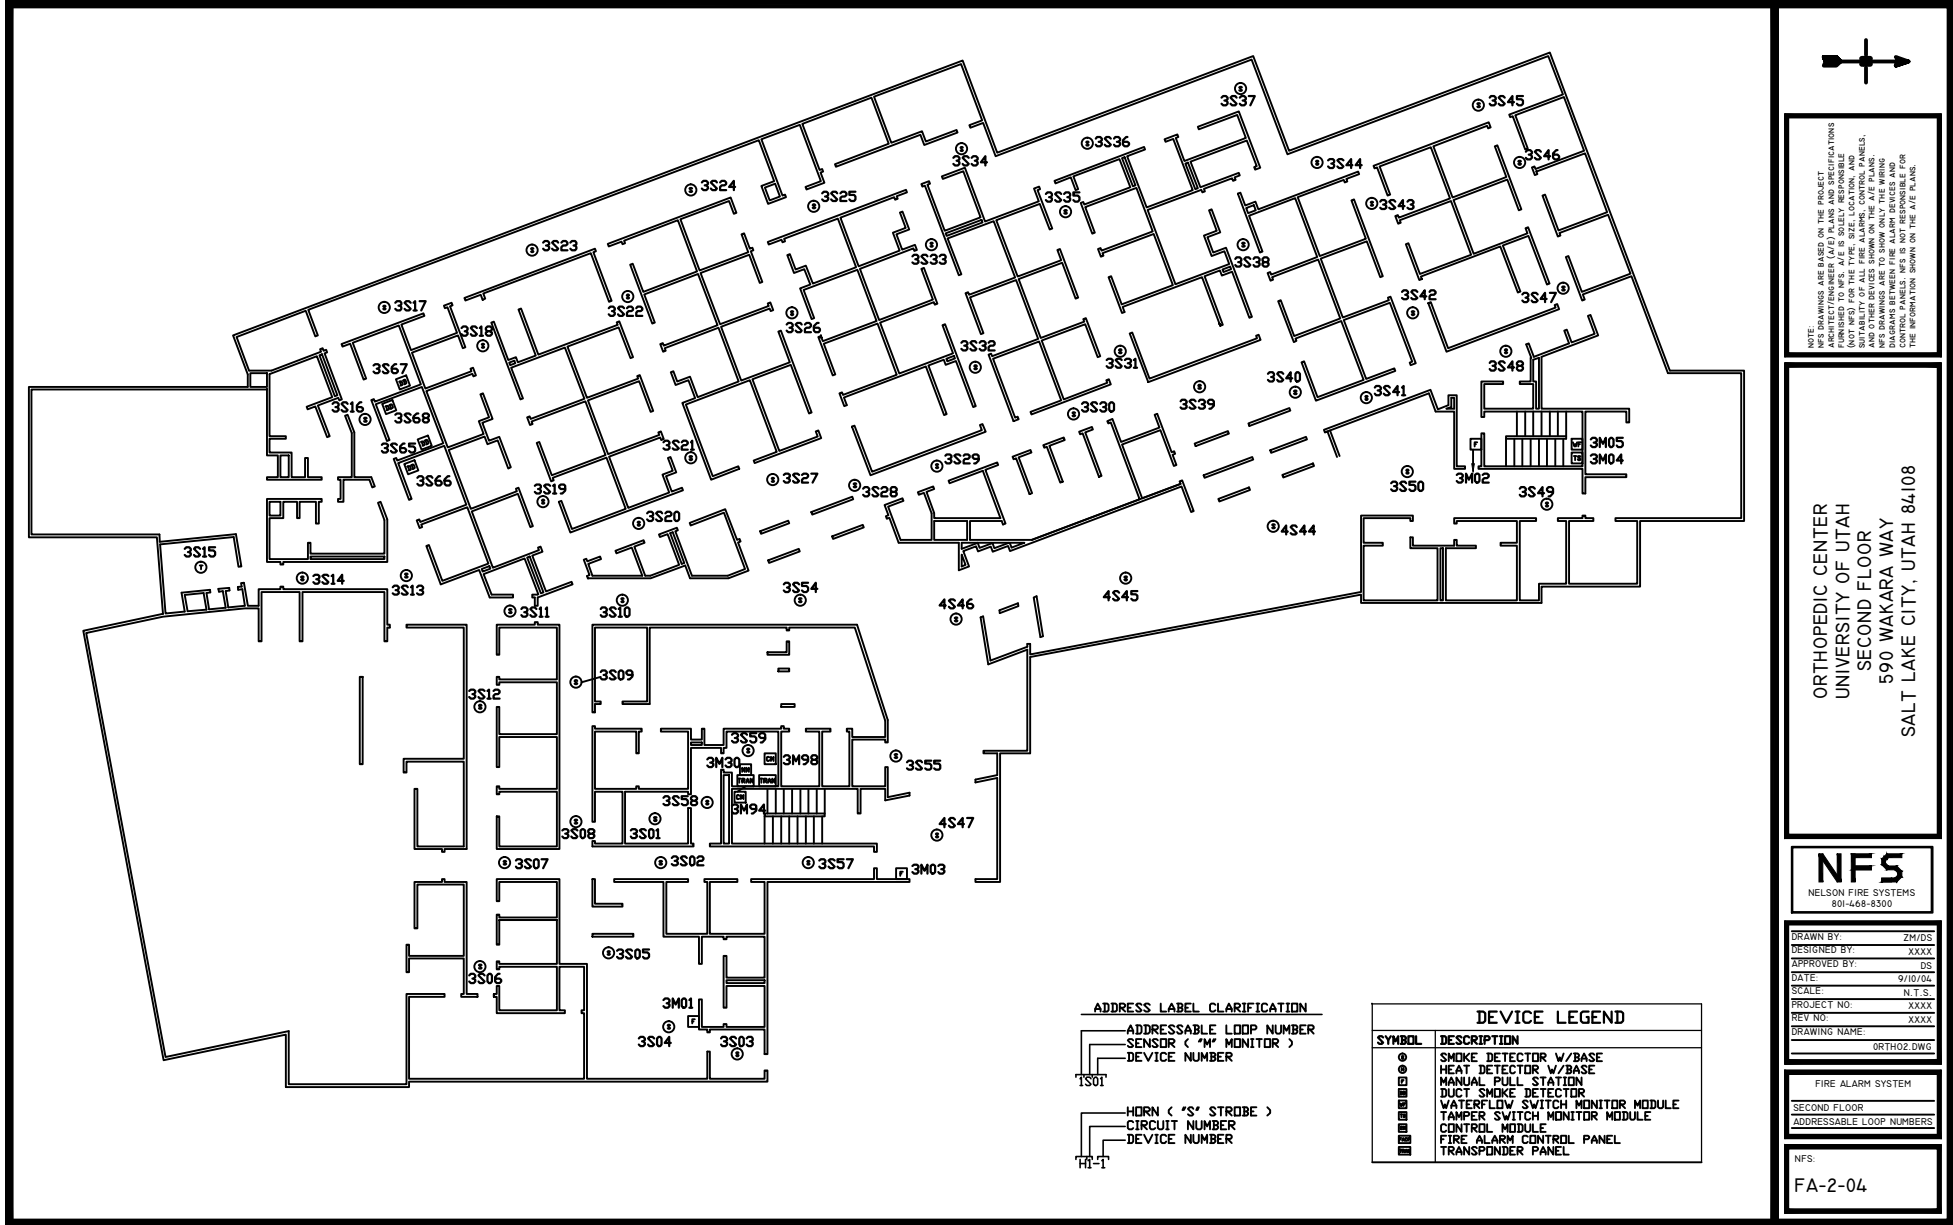


NOTE:
NFS DRAWINGS ARE BASED ON THE PROJECT INFORMATION PROVIDED BY THE USER. THE USER IS RESPONSIBLE FOR VERIFYING THE INFORMATION AND FOR PROVIDING THE NECESSARY INFORMATION FOR THE USER TO BE RESPONSIBLE FOR THE INFORMATION SHOWN ON THE A/E PLANS. NFS DRAWINGS ARE TO SHOW ONLY THE WIRING AND OTHER DEVICES SHOWN ON THE A/E PLANS. NFS IS NOT RESPONSIBLE FOR THE INFORMATION SHOWN ON THE A/E PLANS.

ORTHOPEDIC CENTER
UNIVERSITY OF UTAH
SECOND FLOOR
590 WAKARA WAY
SALT LAKE CITY, UTAH 84108

NFS
NELSON FIRE SYSTEMS
801-468-8300

DRAWN BY: ZM/GS
DESIGNED BY: XXXX
APPROVED BY: DS
DATE: 9/10/04
SCALE: N.T.S.
PROJECT NO: XXXX
REV NO: XXXX
DRAWING NAME: ORTHOZ DWC

FIRE ALARM SYSTEM
SECOND FLOOR
ADDRESSABLE LOOP NUMBERS


NFS:
FA-2-04

ADDRESS LABEL CLARIFICATION

ADDRESSABLE LOOP NUMBER
SENSOR ("M" MONITOR)
DEVICE NUMBER
HORN ("S" STROBE)
CIRCUIT NUMBER
DEVICE NUMBER

DEVICE LEGEND

SYMBOL	DESCRIPTION
⊙	SMOKE DETECTOR W/BASE
⊙	HEAT DETECTOR W/BASE
⊙	MANUAL PULL STATION
⊙	DUCT SMOKE DETECTOR
⊙	WATERFLOW SWITCH MONITOR MODULE
⊙	TAMPER SWITCH MONITOR MODULE
⊙	CONTROL MODULE
⊙	FIRE ALARM CONTROL PANEL
⊙	TRANSPONDER PANEL

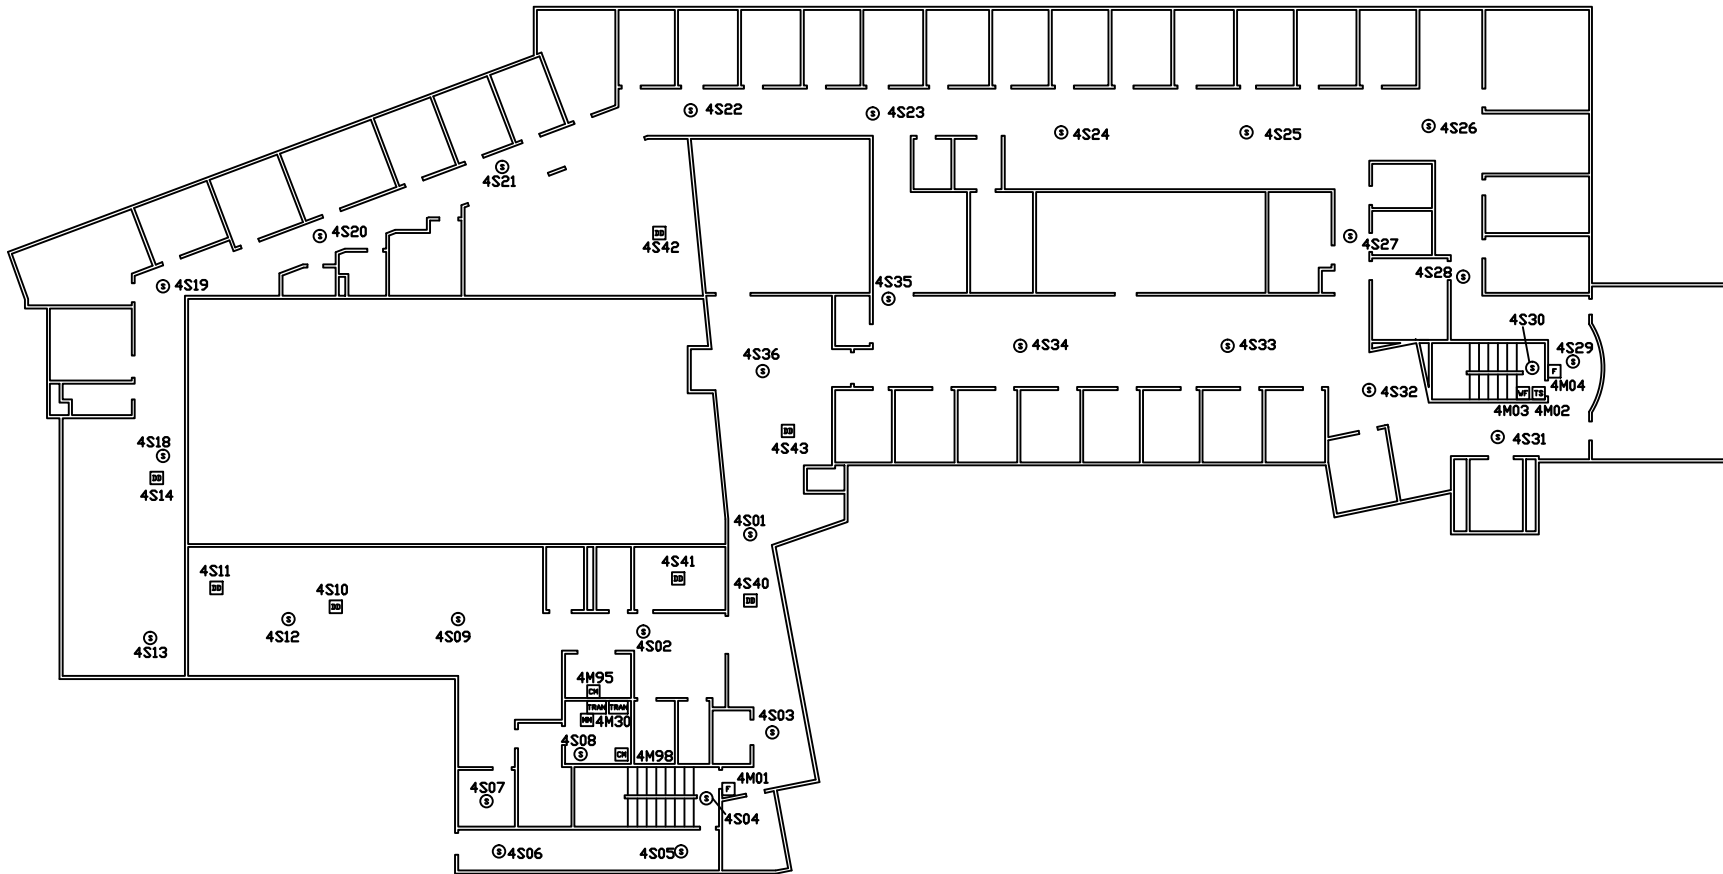

NOTE:
NFS DRAWINGS ARE BASED ON THE PROJECT
NFS HAS CONDUCTED VISUAL VERIFICATION
AND CONFIRMED THE LOCATION OF THE
(NOT NFS) FOR THE TYPE, SIZE, LOCATION, AND
FUNCTION OF THE DEVICES SHOWN ON THE A/E PLANS.
NFS DRAWINGS ARE TO SHOW ONLY THE WIRING
AND OTHER DEVICES SHOWN ON THE A/E PLANS.
NFS IS NOT RESPONSIBLE FOR THE
CONTROL PANELS. NFS IS NOT RESPONSIBLE FOR
THE INFORMATION SHOWN ON THE A/E PLANS.

ORTHOPEDIC CENTER
UNIVERSITY OF UTAH
THIRD FLOOR
590 WAKARA WAY
SALT LAKE CITY, UTAH 84108

NFS
NELSON FIRE SYSTEMS
801-468-8300

DRAWN BY: ZM/GS
DESIGNED BY: XXXX
APPROVED BY: GS
DATE: 9/10/04
SCALE: N.T.S.
PROJECT NO: XXXX
REV NO: XXXX
DRAWING NAME: ORTHO3.DWG

FIRE ALARM SYSTEM
THIRD FLOOR
ADDRESSABLE LOOP NUMBERS

NFS
FA-3-04

DEVICE LEGEND	
SYMBOL	DESCRIPTION
Ⓢ	SMOKE DETECTOR W/BASE
Ⓜ	MANUAL PULL STATION
Ⓢ	DUCT SMOKE DETECTOR
Ⓜ	WATERFLOW SWITCH MONITOR MODULE
Ⓢ	TAMPER SWITCH MONITOR MODULE
Ⓜ	CONTROL MODULE
Ⓜ	TRANSPONDER PANEL

ADDRESS LABEL CLARIFICATION

— ADDRESSABLE LOOP NUMBER
— SENSOR < 'M' MONITOR >
— DEVICE NUMBER

4S01

— HORN < 'S' STROBE >
— CIRCUIT NUMBER
— DEVICE NUMBER

4M01