


LEGEND


- Ⓢ SMOKE DETECTOR
- Ⓜ MANUAL PULL STATION
- Ⓛ DUCT DETECTOR
- Ⓜ STROBE/HORN
- Ⓢ CHIME STROBE
- Ⓡ RELAY
- Ⓜ DOORHOLDER



HEARTPORT RESEARCH FACILITY
RESEARCH PARK
UNIVERSITY OF UTAH
FIRST FLOOR
FIRE ALARM SYSTEM
HEART1.DWG
SEPTEMBER 4, 1997

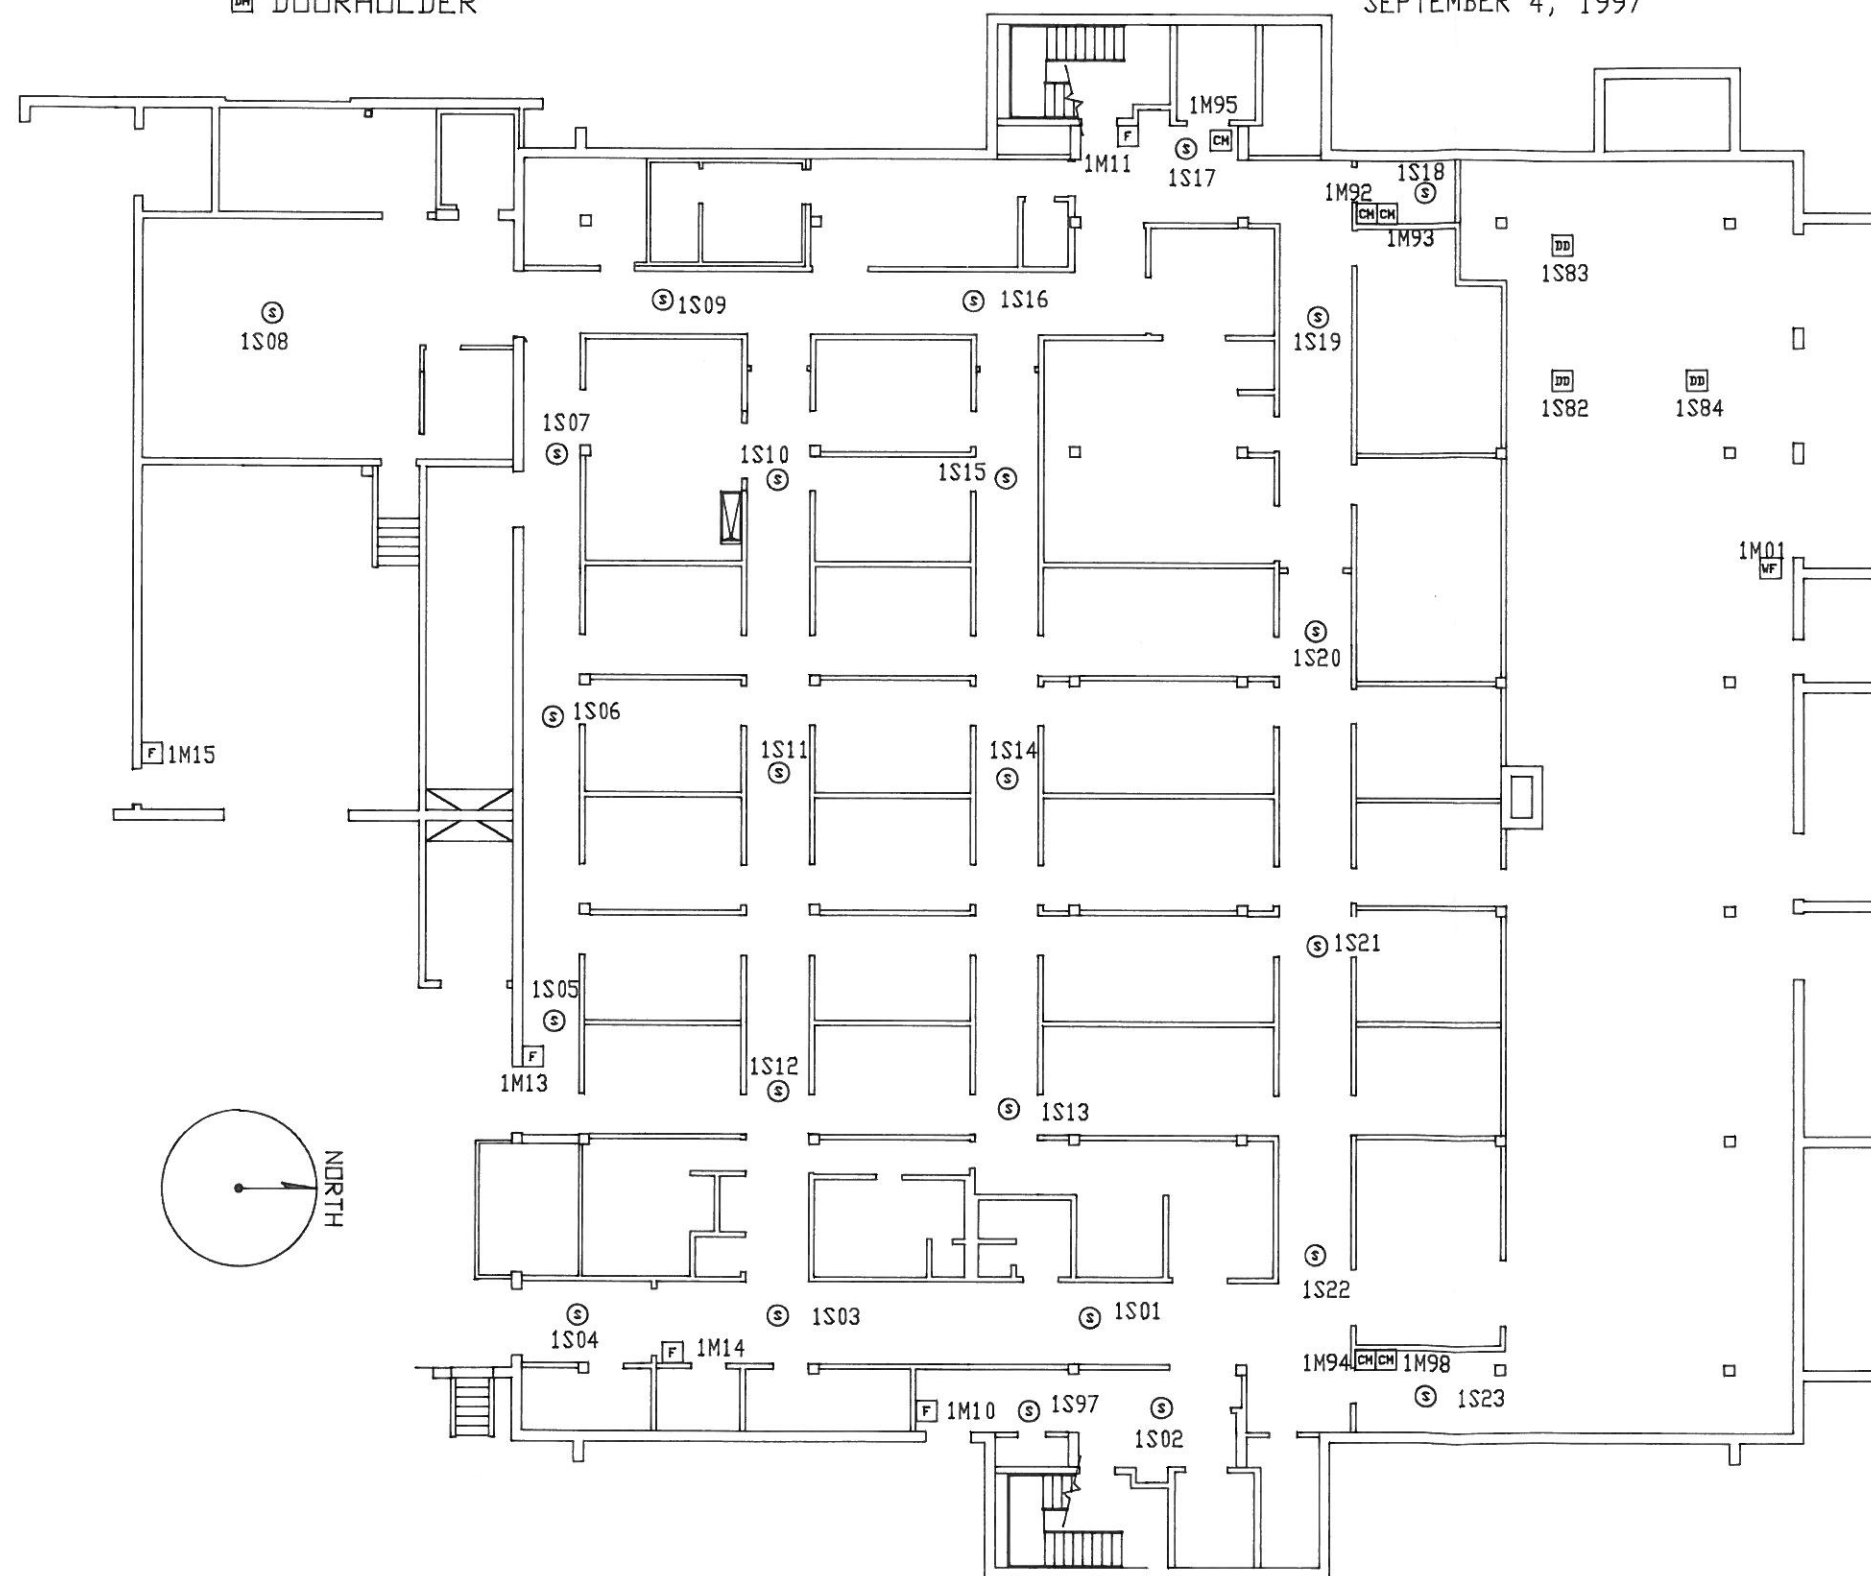

FIRST FLOOR

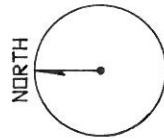


HEARTPORT RESEARCH FACILITY
RESEARCH PARK
UNIVERSITY OF UTAH
2ND & 3RD FLOOR
FIRE ALARM SYSTEM
HEART2.DWG
SEPTEMBER 4, 1997


LEGEND

- ⊙ SMOKE DETECTOR
- ⌘ MANUAL PULL STATION
- ⌘ DUCT DETECTOR
- ⌘ WATERFLOW SWITCH
- ⌘ TAMPER SWITCH

NFS
NELSON FIRE SYSTEMS
288-9905

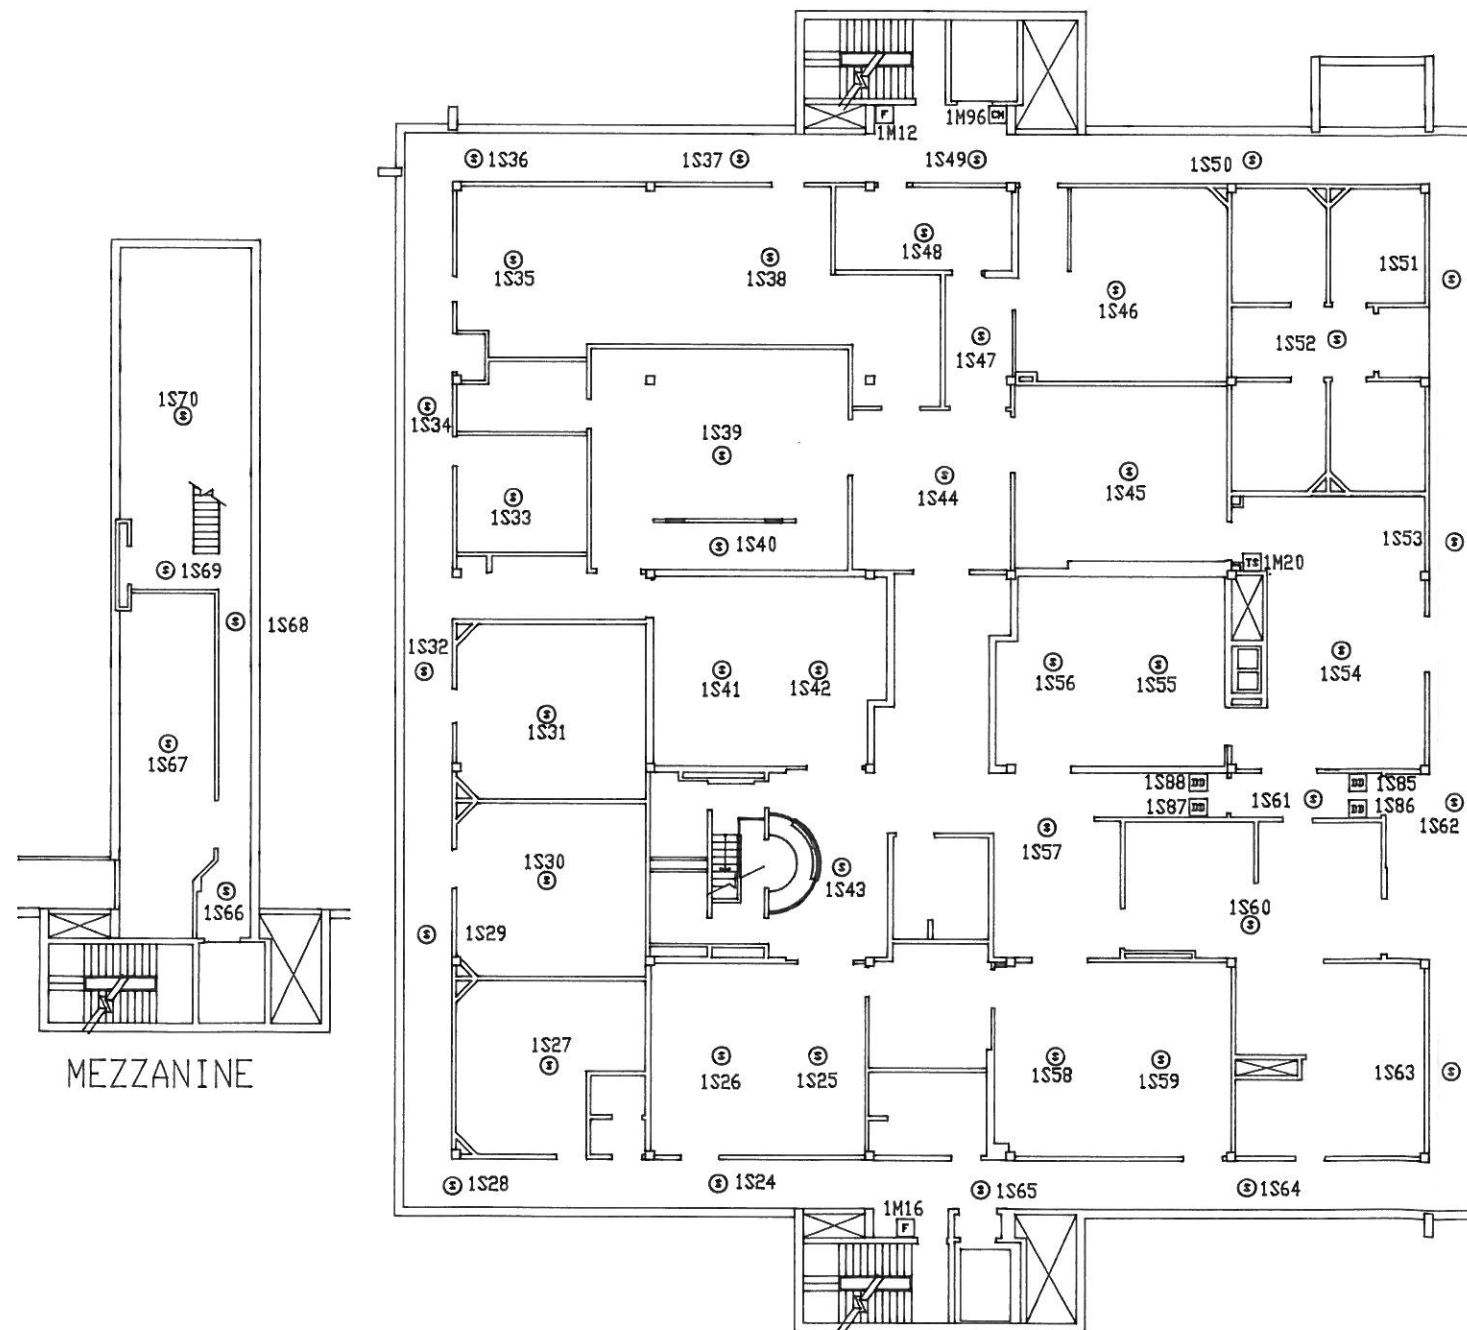

SECOND FLOOR

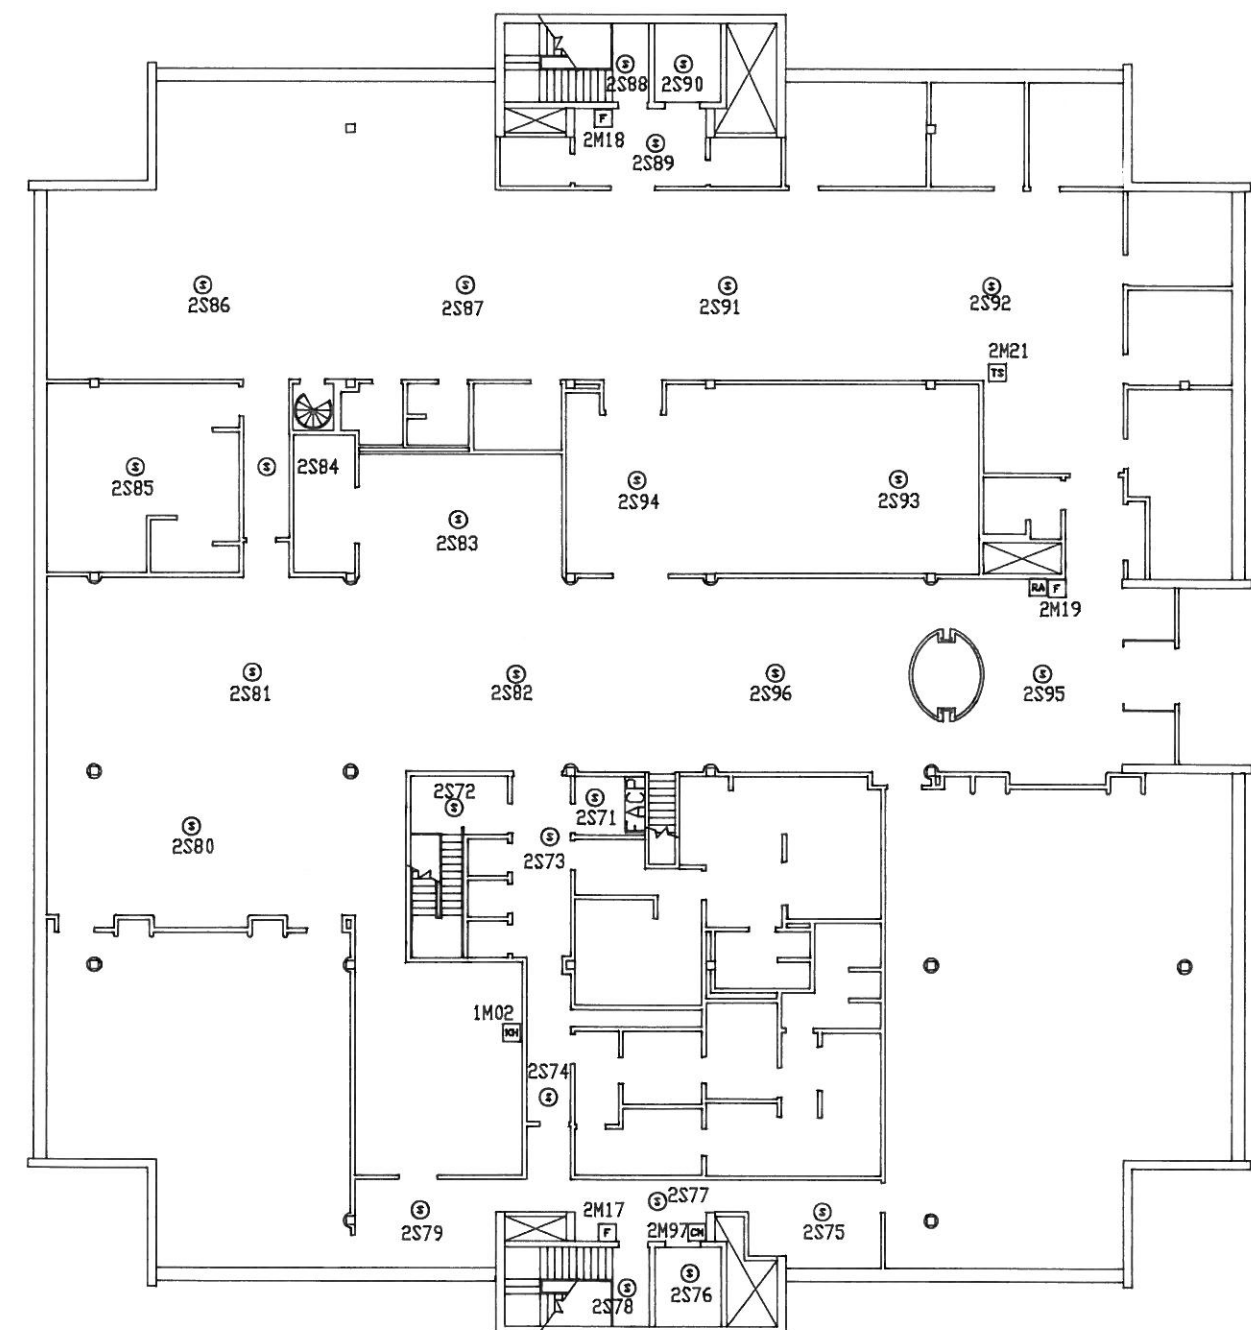

THIRD FLOOR